圖號	圖名	張號
A1.1	圖號索引表	1 / 40
A1.2	配置平面圖	2 / 40
A1.3	整備平面圖	3 / 40
A2.1	一層平面圖	4 / 40
A2.2	二層平面圖	5 / 40
A2.3	三層平面圖	6 / 40
A2.4	屋頂平面圖	7 / 40
A3.1	東向立面	8 / 40
A3.2	西向立面	9 / 40
A3.3	南向立面	10 / 40
A3.4	北向立面	11 / 40
A4.1	S1縱向剖面	12 / 40
A4.2	S2縱向剖面	13 / 40
A4.3	S3縱向剖面	14 / 40
A4.4	S4縱向剖面	15 / 40
A4.5	S5縱向剖面	16 / 40
D.1	欄杆詳圖一	18 / 40
D.2	欄杆詳圖二	19 / 40
D.3	隱形鐵窗 詳圖	21 / 2 9
D.4	工程告示牌示意圖	20 / 40
E.1	照明回路單線圖	21 / 40
E.2	室外LED條燈 一層平面圖	22 / 40
E.3	室外LED條燈 二層平面圖	23 / 40
E.4	室外LED條燈 三層平面圖	24 / 40
F.1	壹層消防設備平面圖	25 / 40
F.2	貳層消防設備平面圖	26 / 40
F.3	參層消防設備平面圖	27 / 40
P.1	透視圖	

學校環境設施無障礙逃生坡道增建工程



位置圖 1

施工說明

1.本工程為既有校舍之增建工程，圖示尺寸若與現場有出入時以現場實測為準。若因現場施工之需要，得於徵得業主與設計單位核可後適當調整細部尺寸，以利配合現況施作。本工程採總價決標責任施工，標單內所列之項目及數量僅供承包人參考，投標前承包人須自行實地勘察，按照圖說規定詳細對標單數量，並且詳細規劃所需安全防護設備，若有疑異可於單價中自行調整或併於其他相關項目內估計，不得以圖說欠詳之理由要求辦理追加。工程總包價須包括所有人工、材料、機具、運輸、安全防護設備、保險及稅捐等費用，如標單圖樣及施工說明均為工程慣例上所有或不可缺少者，承包人不得藉此推諉及要求加價。

2.本工程圖樣說明書及標單所指定之材料及規格，承包人投標前均須確實瞭解，投標前需確實詢價，得標後不得以標價過低要求變更材料，或要求材料商低價供應而影響工程品質，如有進口材料，須視工程進度提前採購，以免延誤工期，所有材料皆須先將樣品送請業主及建築師核准，同意後使用；如提送材料樣品過程遲延而延誤工期，概由承包人自行負責。

3.標單所列之廠牌均僅供參考，承商得選用同品質，性能相同或較優之建材或設備，經業主及建築師審核完成後，方可使用。所有材料、色樣、規格型號等施工廠商須於該項施工前送樣，經業主及使用單位核准選色後方可施工。

4.本工程所規定之材料及規格，如市場無法供給時，承包人須於決標後二週內向業主提出，否則仍須設法採購，不得要求變更設計或延長工期，若確因市面缺貨不能辦理，承包人得提出同等品，經建築師及業主審核同意後方可使用，但承包人不得以此要求加價。如因而減省履約費用，應自契約價金中扣除。

5.承包商或施工單位應於施工前提送施工細部詳圖，經業主或設計單位核可後方得施作。施工詳圖應考量構造之安全強度，並指明材料、固定方法、接合細節、塗裝及附件尺寸等說明。


6.承包人必須切實按照核定圖樣施工，如原計畫有未理想之處，欲于變更原設計時，須事先提出檢核或辦理變更手續，經核准後再行施工以符程序以及可能關聯到的法令規定，切勿擅自變更。

7.所有新工程若與現有水電等設施相衝突，應先與建築師討論後再行處置，不得擅自將其滅失。

8.各項工程於施工中，因拆除導致破壞到原建物之設備或美觀時，承商應予修繕復原.施工期間因配合不當，致影響或破壞已完成裝修之工程部分承商應無條件以相同品質及規格予以修復。

9.注意鄰房及學生之安全，不可將建築材料堆置於道路上防礙交通，建築工地需做安全圍籬，不得讓非工程人員進入。


10.承包廠商請於開工前提送各項計畫書至監造單位處審查，並完成環保單位之空污費及營造業應否檢具事業廢棄物清理計劃書及上網申報判定表等事項申報，以免延誤工期。

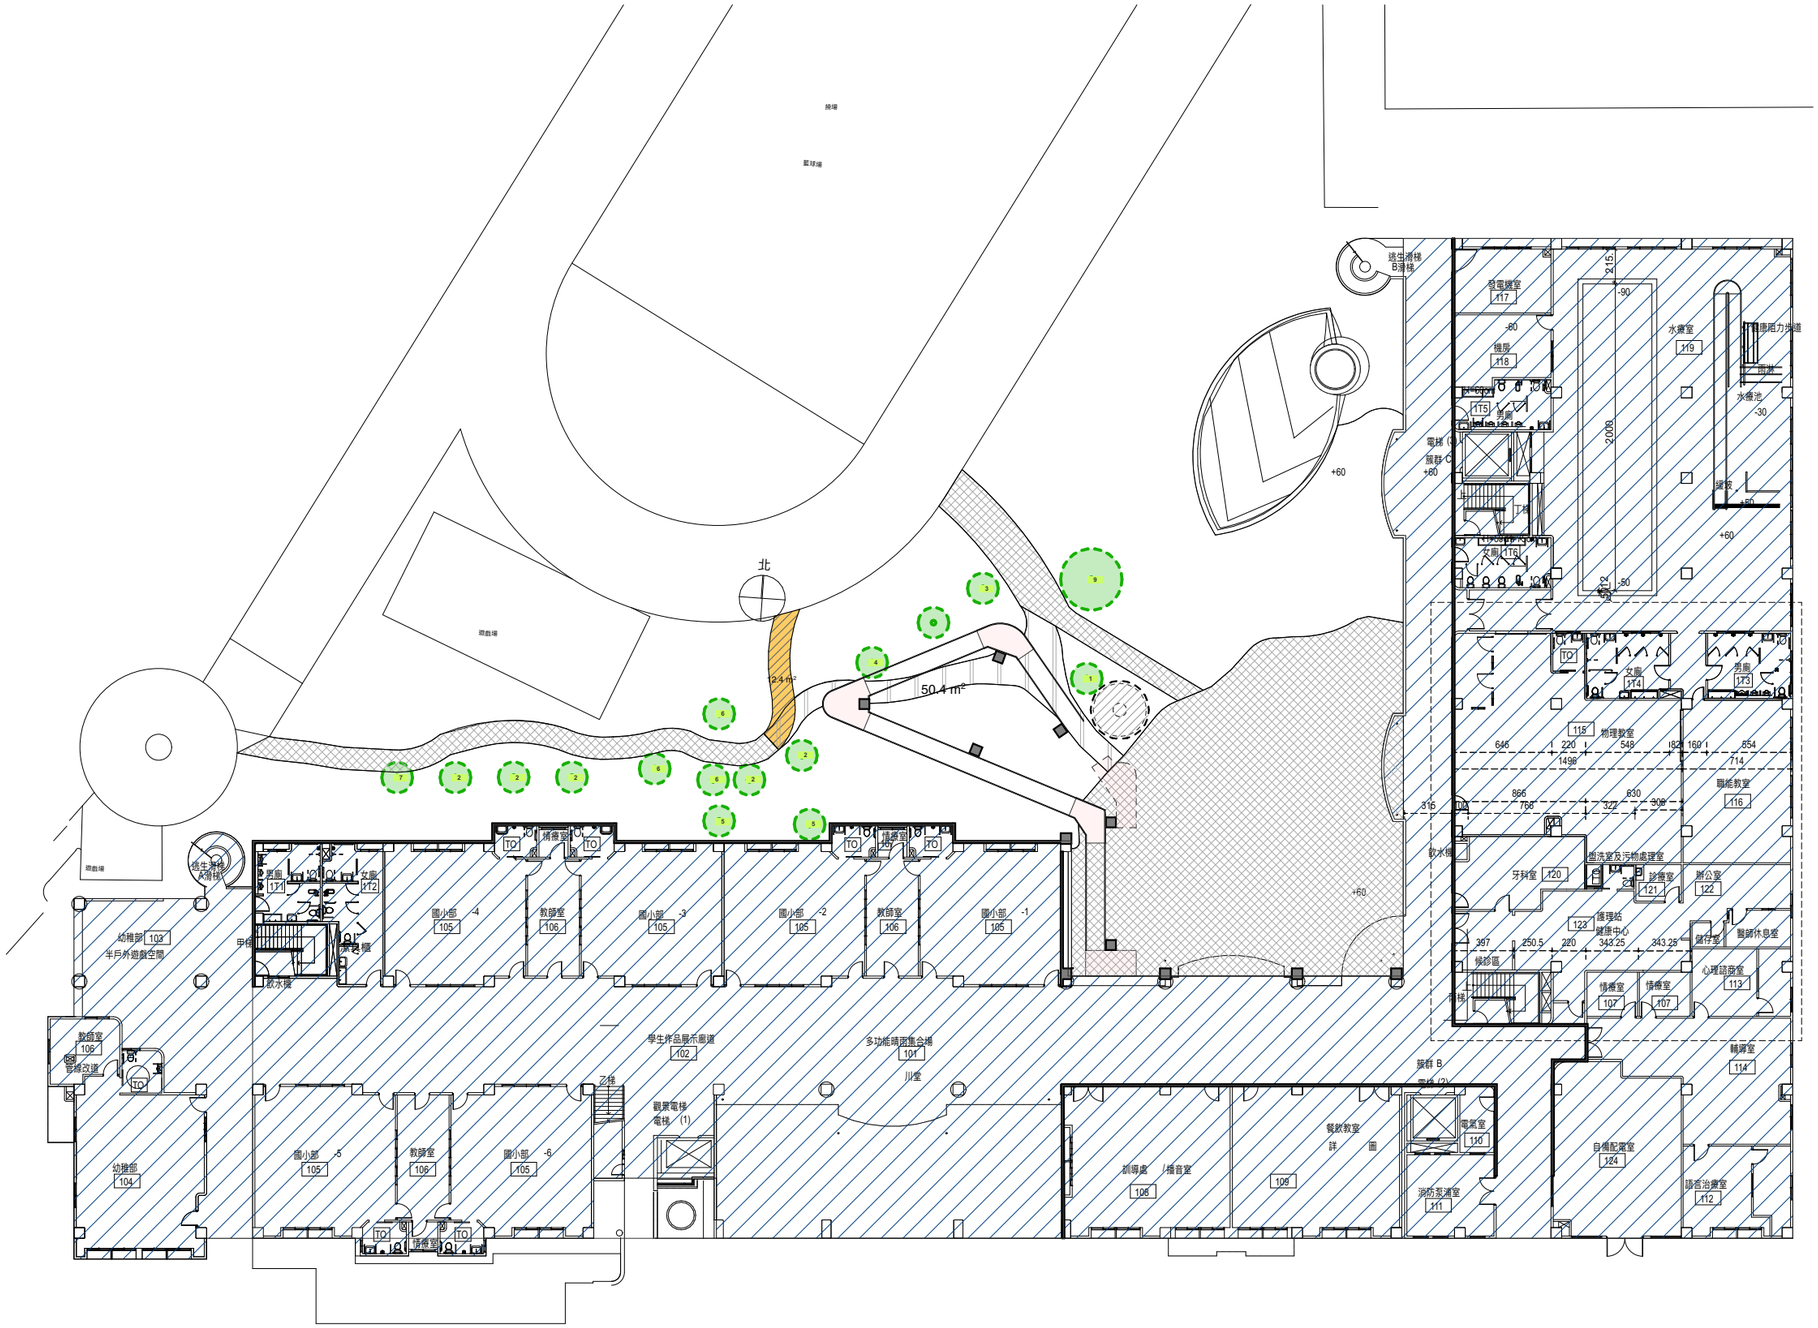

配置平面圖
S=1:400

1

ATELIER	notes 細部設計圖	Project 學校環境設施無障礙逃生坡道增建工程	Scale	Title 配置平面圖	Layout ID A1.2	2/28 Date 2026/10/2

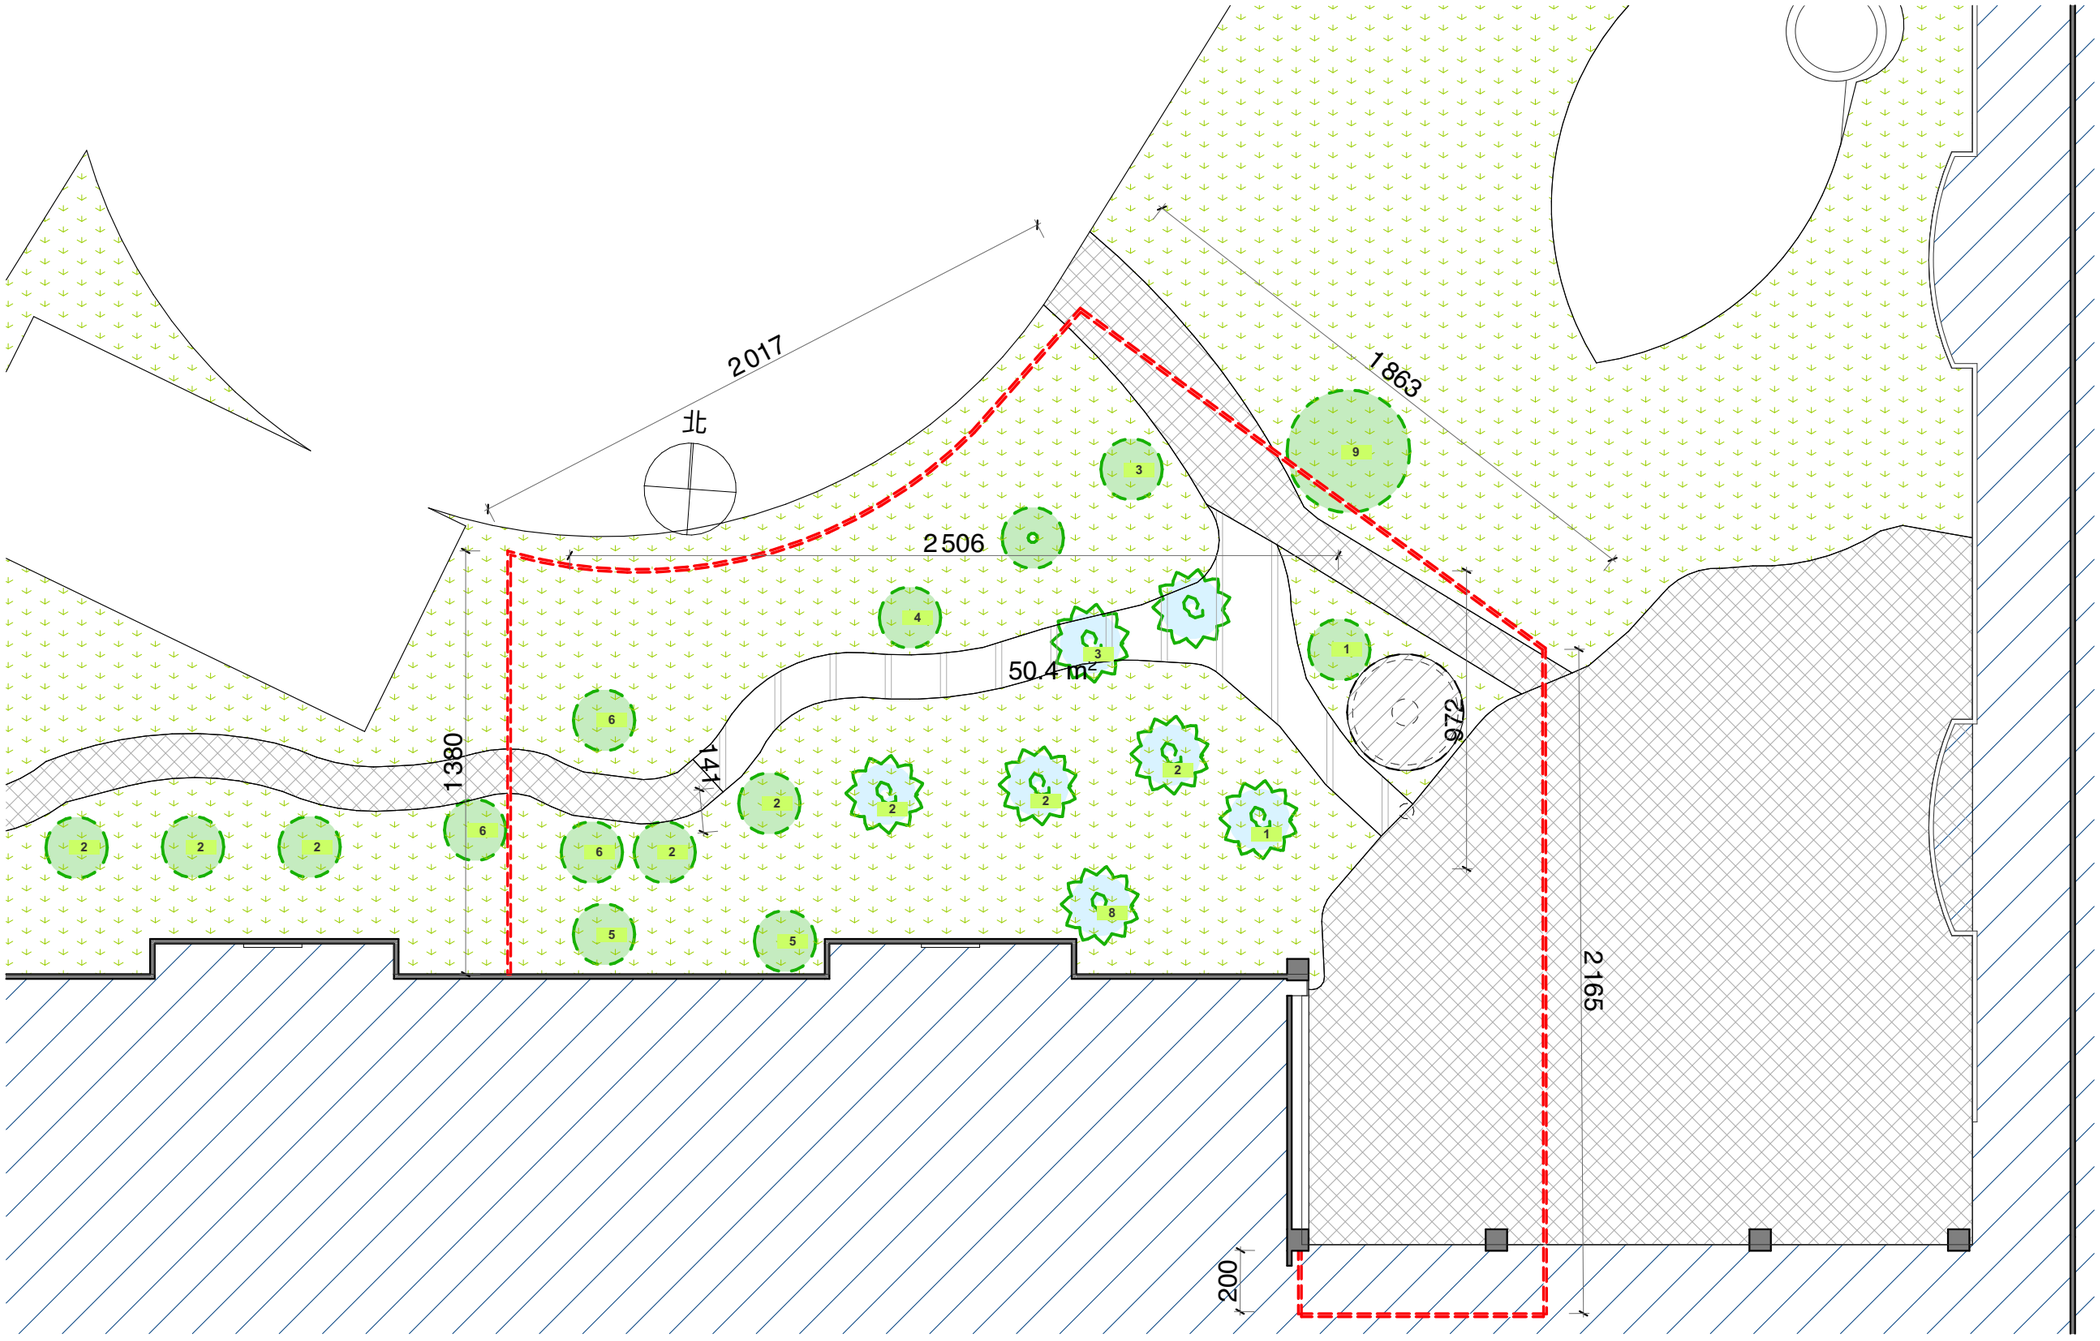

圖例

- 原有連鎖磚挖除轉用補植草皮
- 原有連鎖磚保留
- 原有喬木移植(業主另行處理)
- 原有喬木保留
- 甲種工地圍籬


原有喬木

1. 印度紫檀
2. 水黃皮
3. 黃槿
4. 阿勃勒
5. 台灣山欖
6. 無患子
7. 琴葉榕
8. 大葉山欖
9. 雨豆樹

整備平面圖
S=1:200

1

ATELIER	notes 細部設計圖	Project 學校環境設施無障礙逃生坡道增建工程	Scale	Title 整備平面圖	Layout ID A1.3	3/28	Date 2026/10/2

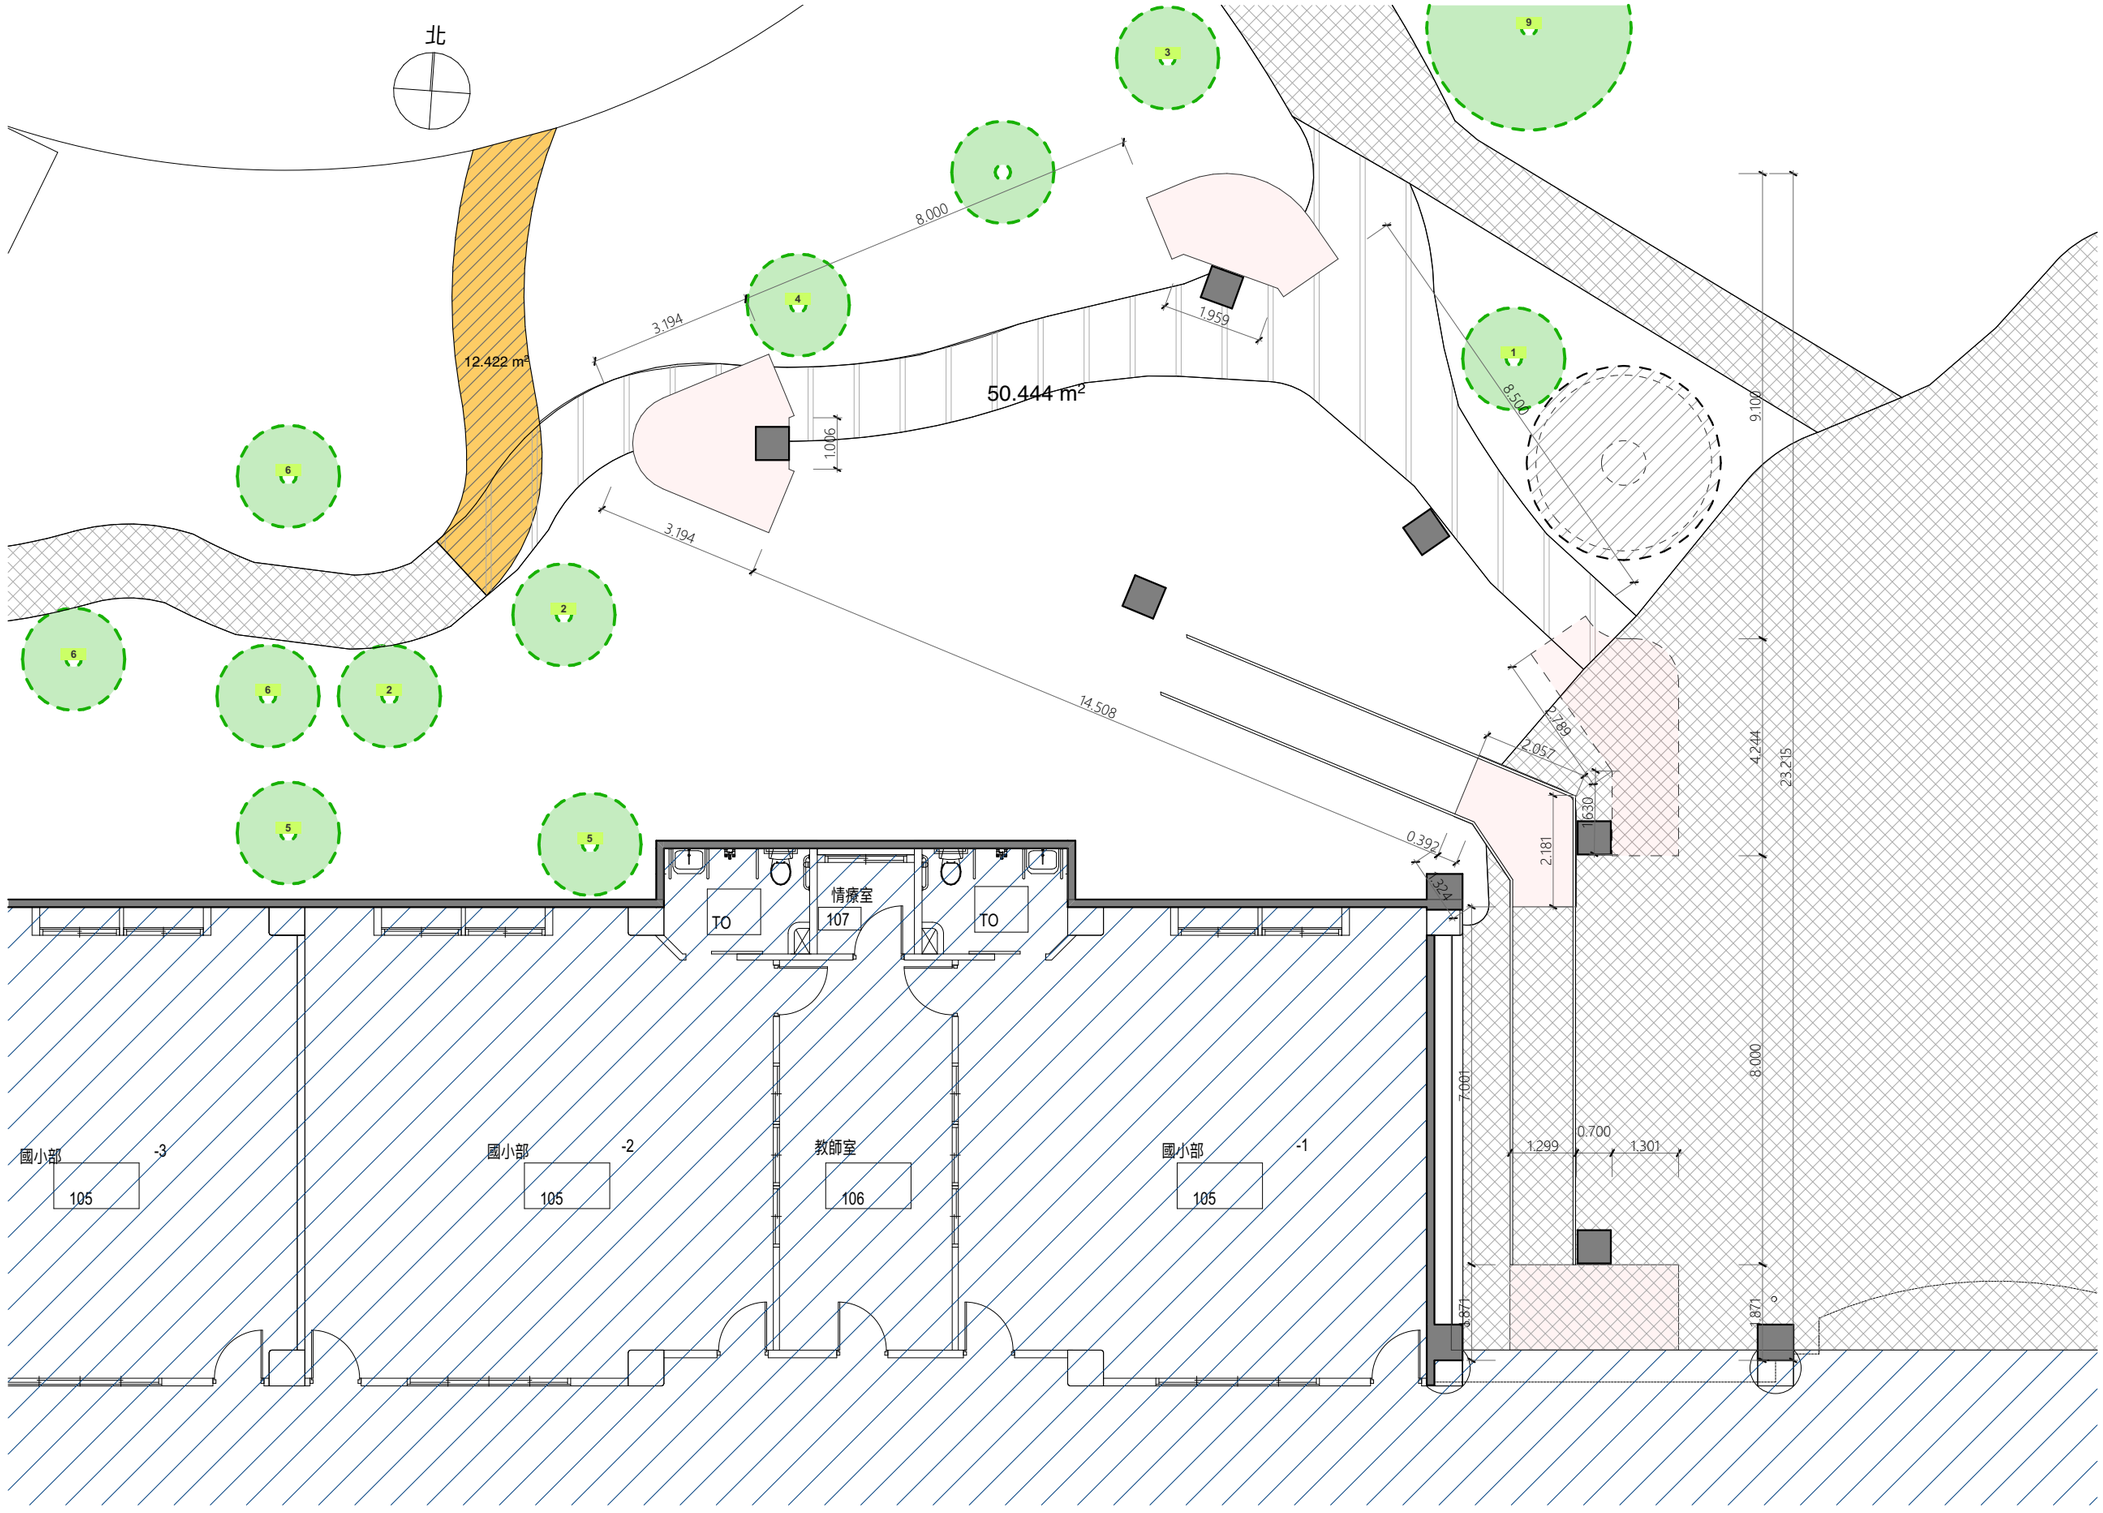


一層平面圖

S=1:120.00

1

ATELIER	notes 細部設計圖	Project 學校環境設施無障礙逃生坡道增建工程	Scale	Title 一層平面圖	Layout ID A2.1	4/28	Date 2026/10/2

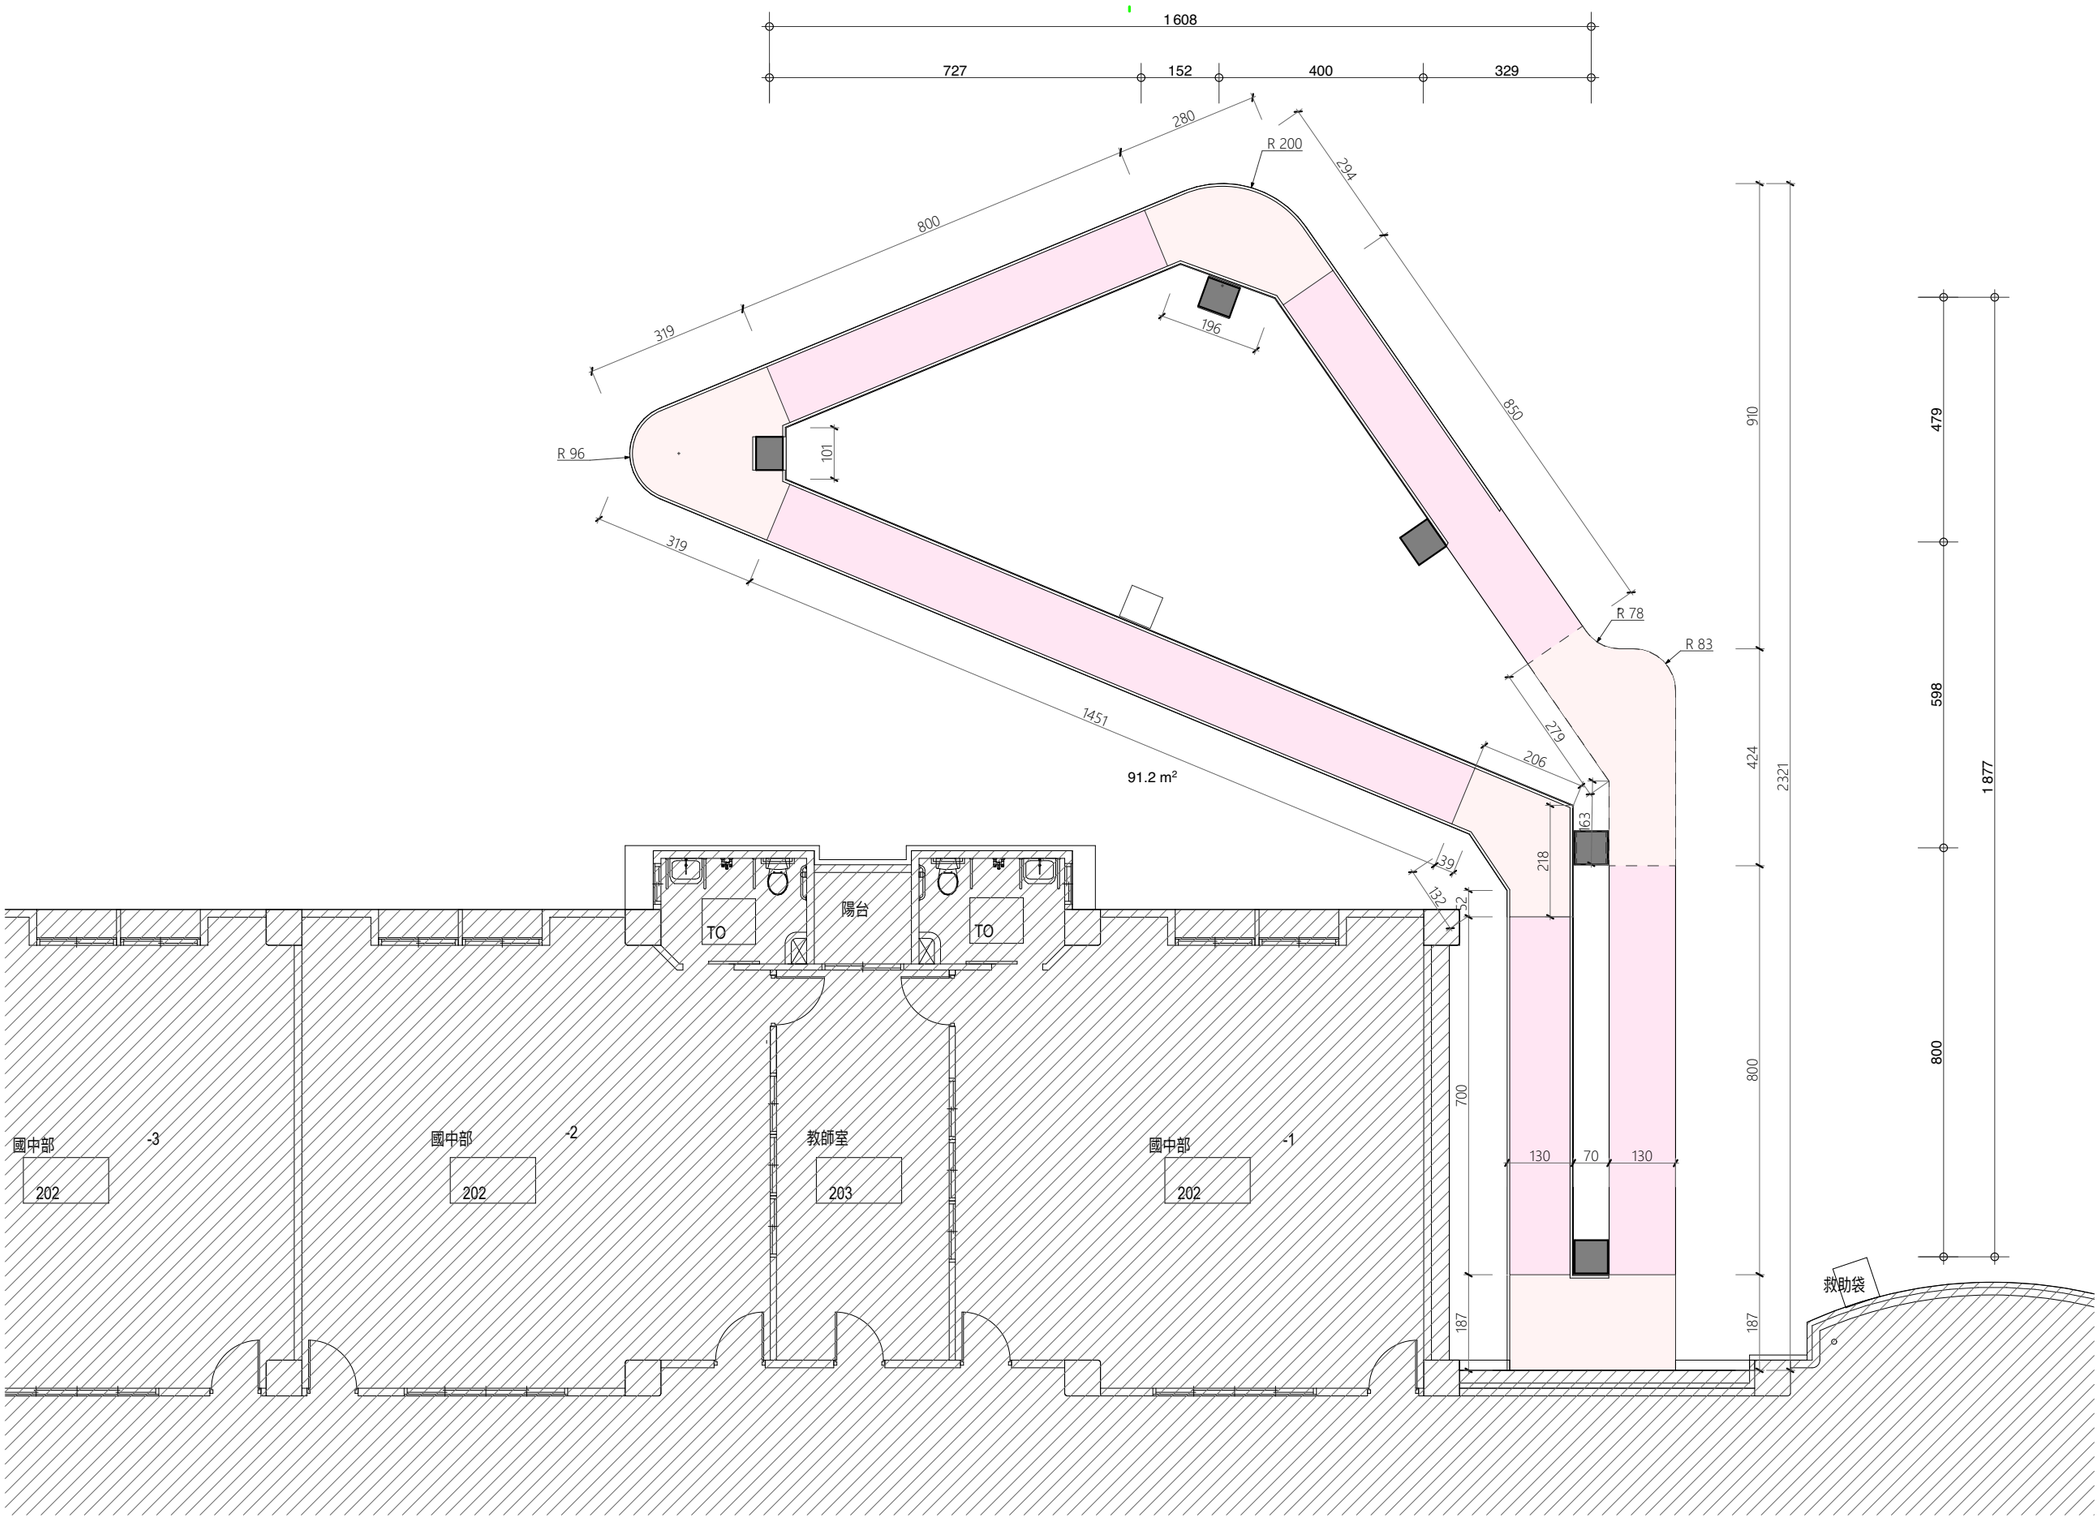


二層平面圖

S=1:120.00

1

ATELIER	notes 細部設計圖	Project 學校環境設施無障礙逃生坡道增建工程	Scale	Title 二層平面圖	Layout ID A2.2	5/28	Date 2026/10/2

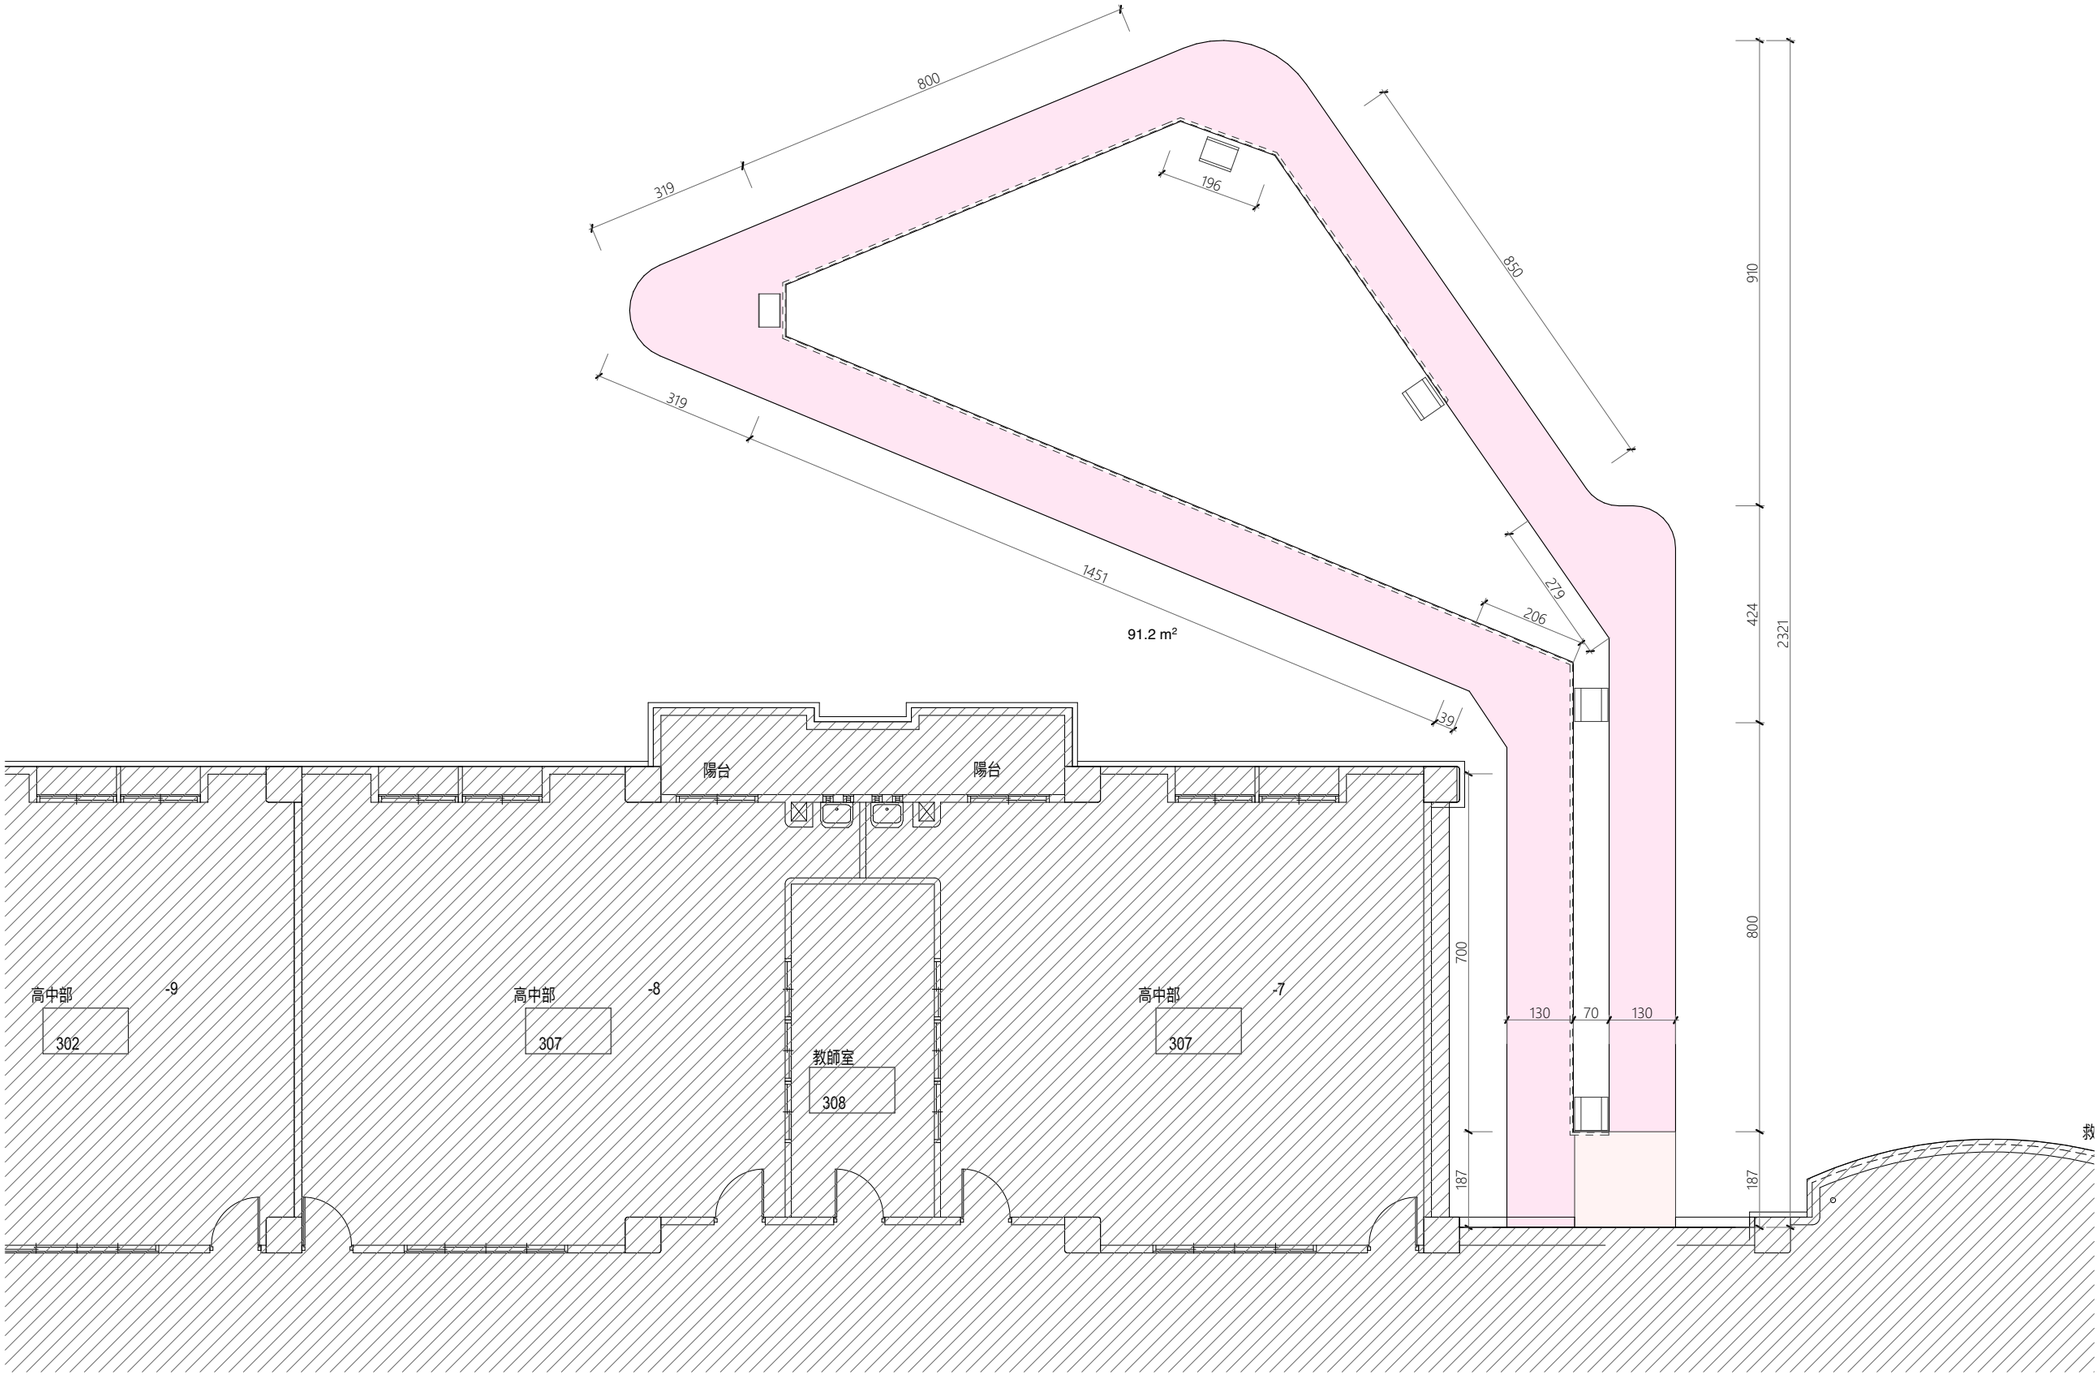


三層平面圖

S=1:120.00

1


ATELIER	notes 細部設計圖	Project 學校環境設施無障礙逃生坡道增建工程	Scale	Title 三層平面圖	Layout ID A2.3	6/28	Date 2026/10/2

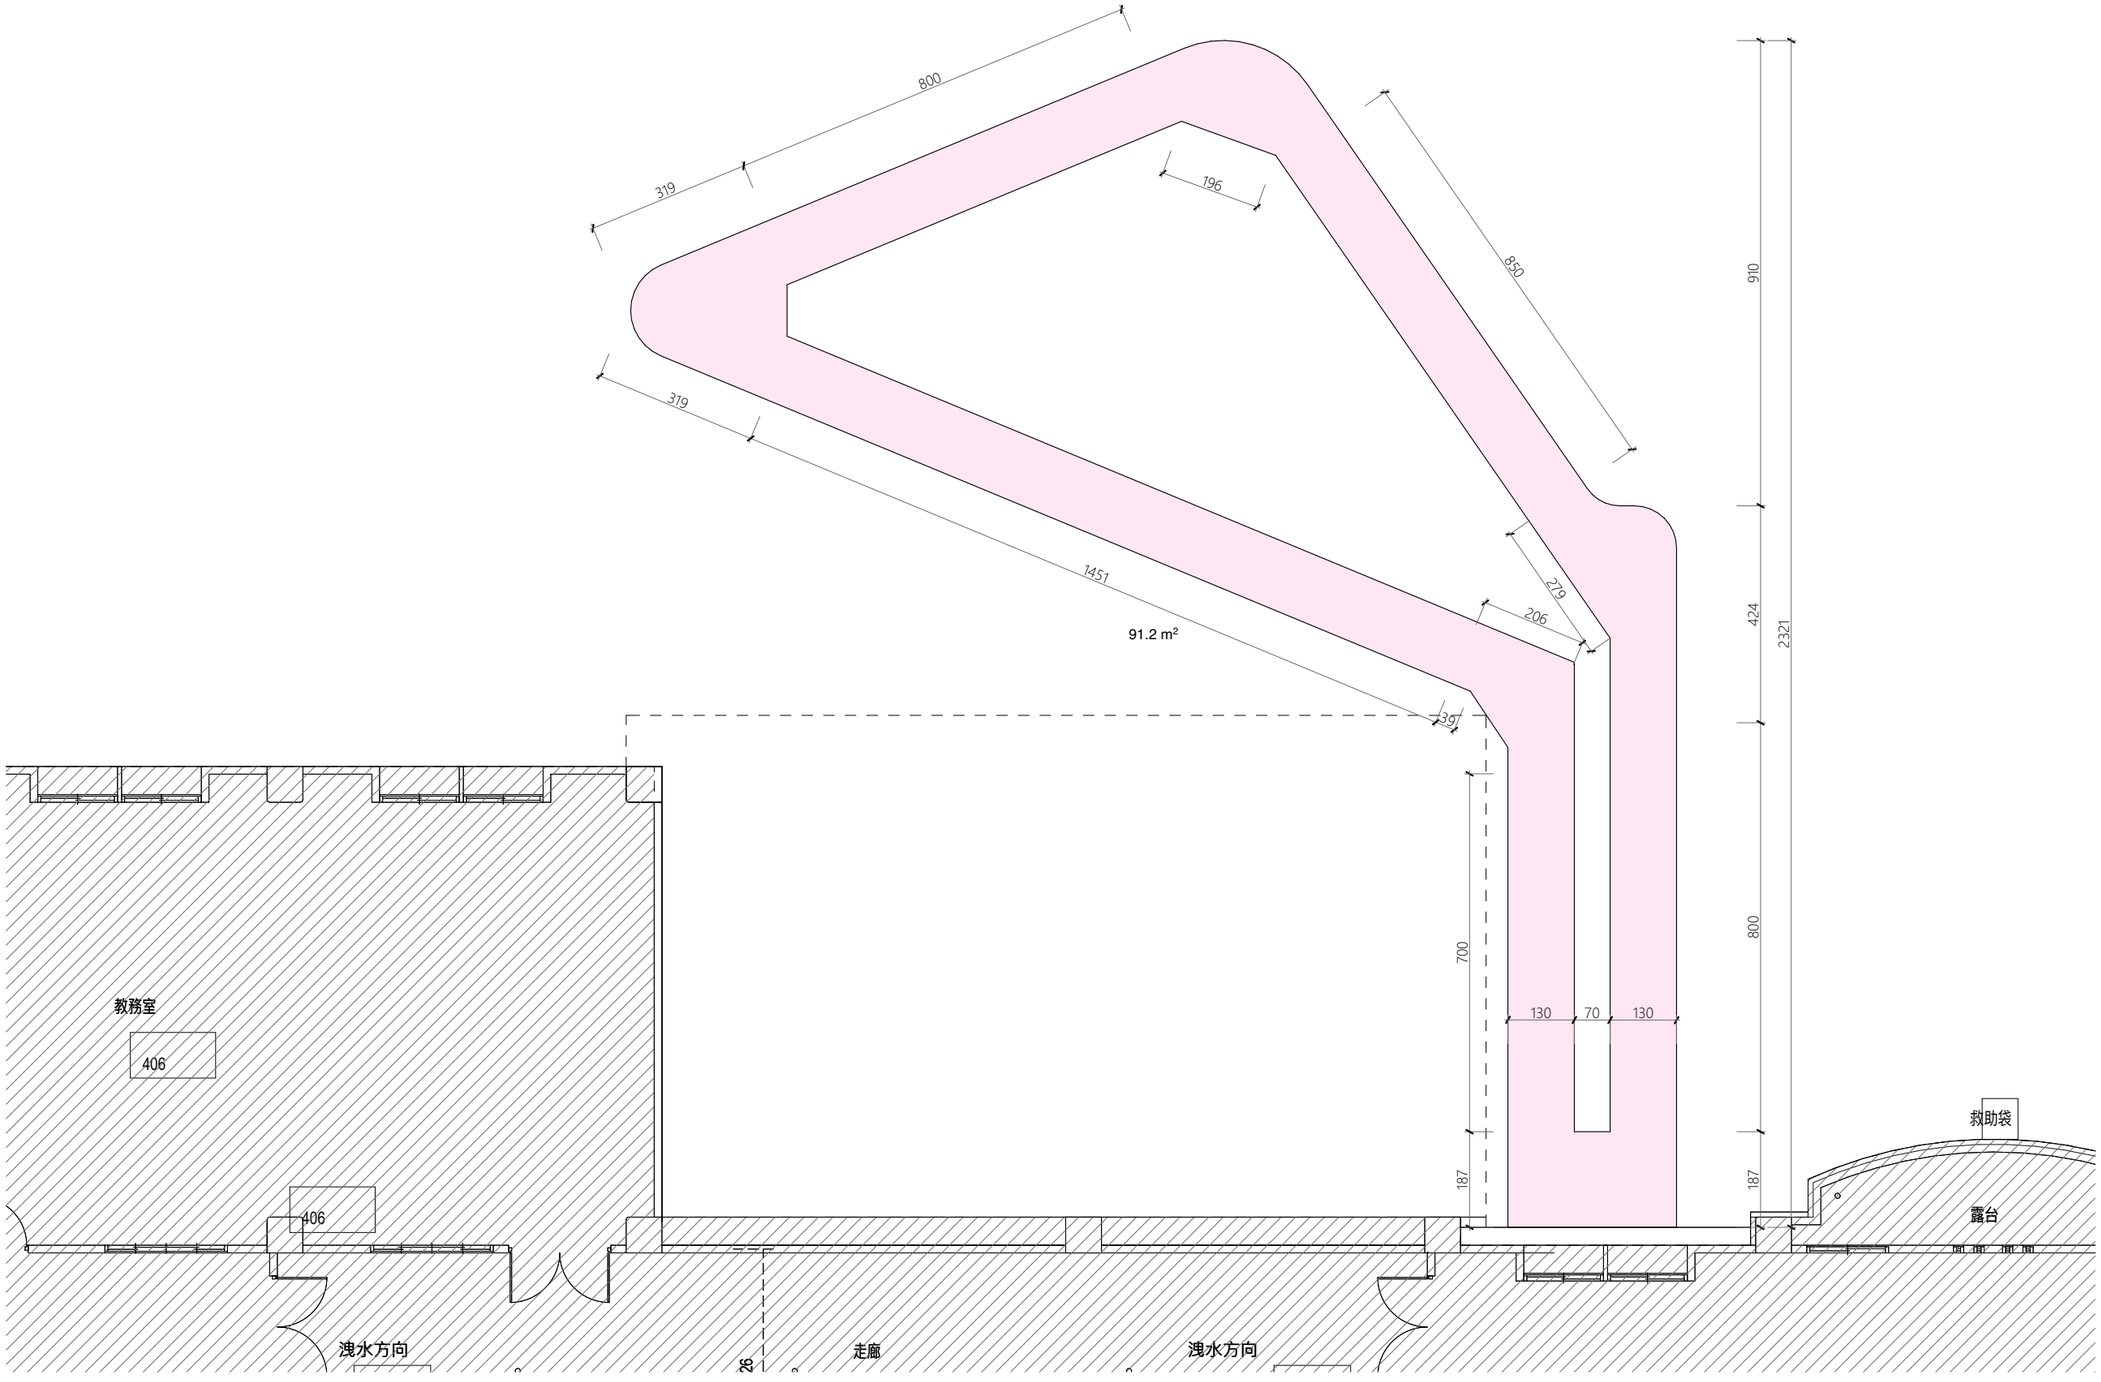

屋頂平面圖
S=1:120.00

1


ATELIER	notes 細部設計圖	Project 學校環境設施無障礙逃生坡道增建工程	Scale	Title 屋頂平面圖	Layout ID A2.4	7/28	Date 2026/10/2

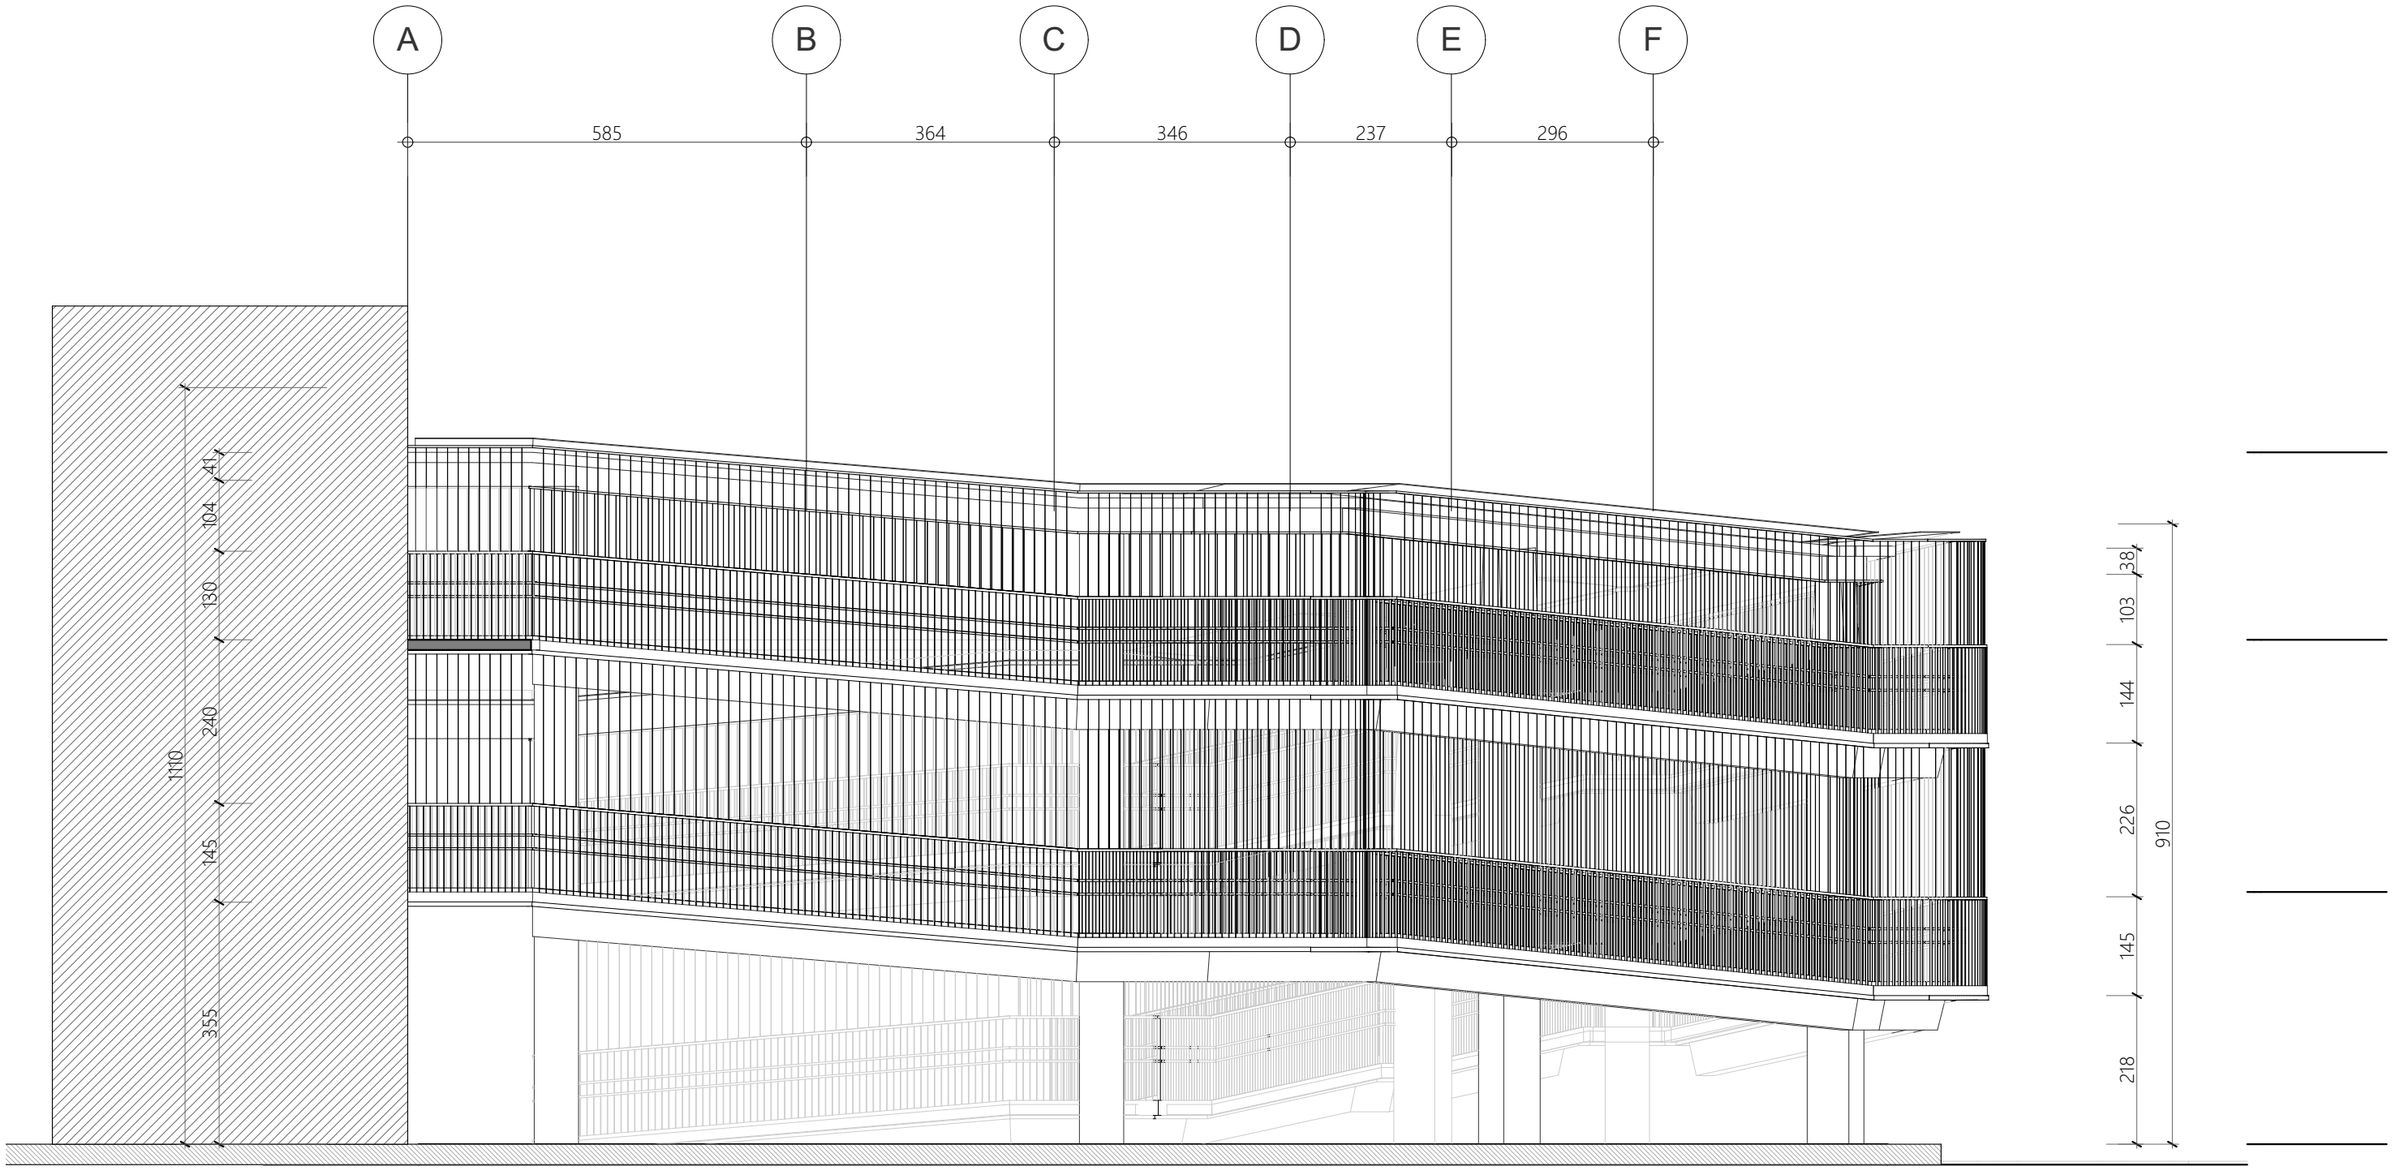

東向立面
S=1:90.00

1

ATELIER	notes 細部設計圖	Project 學校環境設施無障礙逃生坡道增建工程	Scale	Title 東向立面	Layout ID A3.1	8/28	Date 2026/10/2

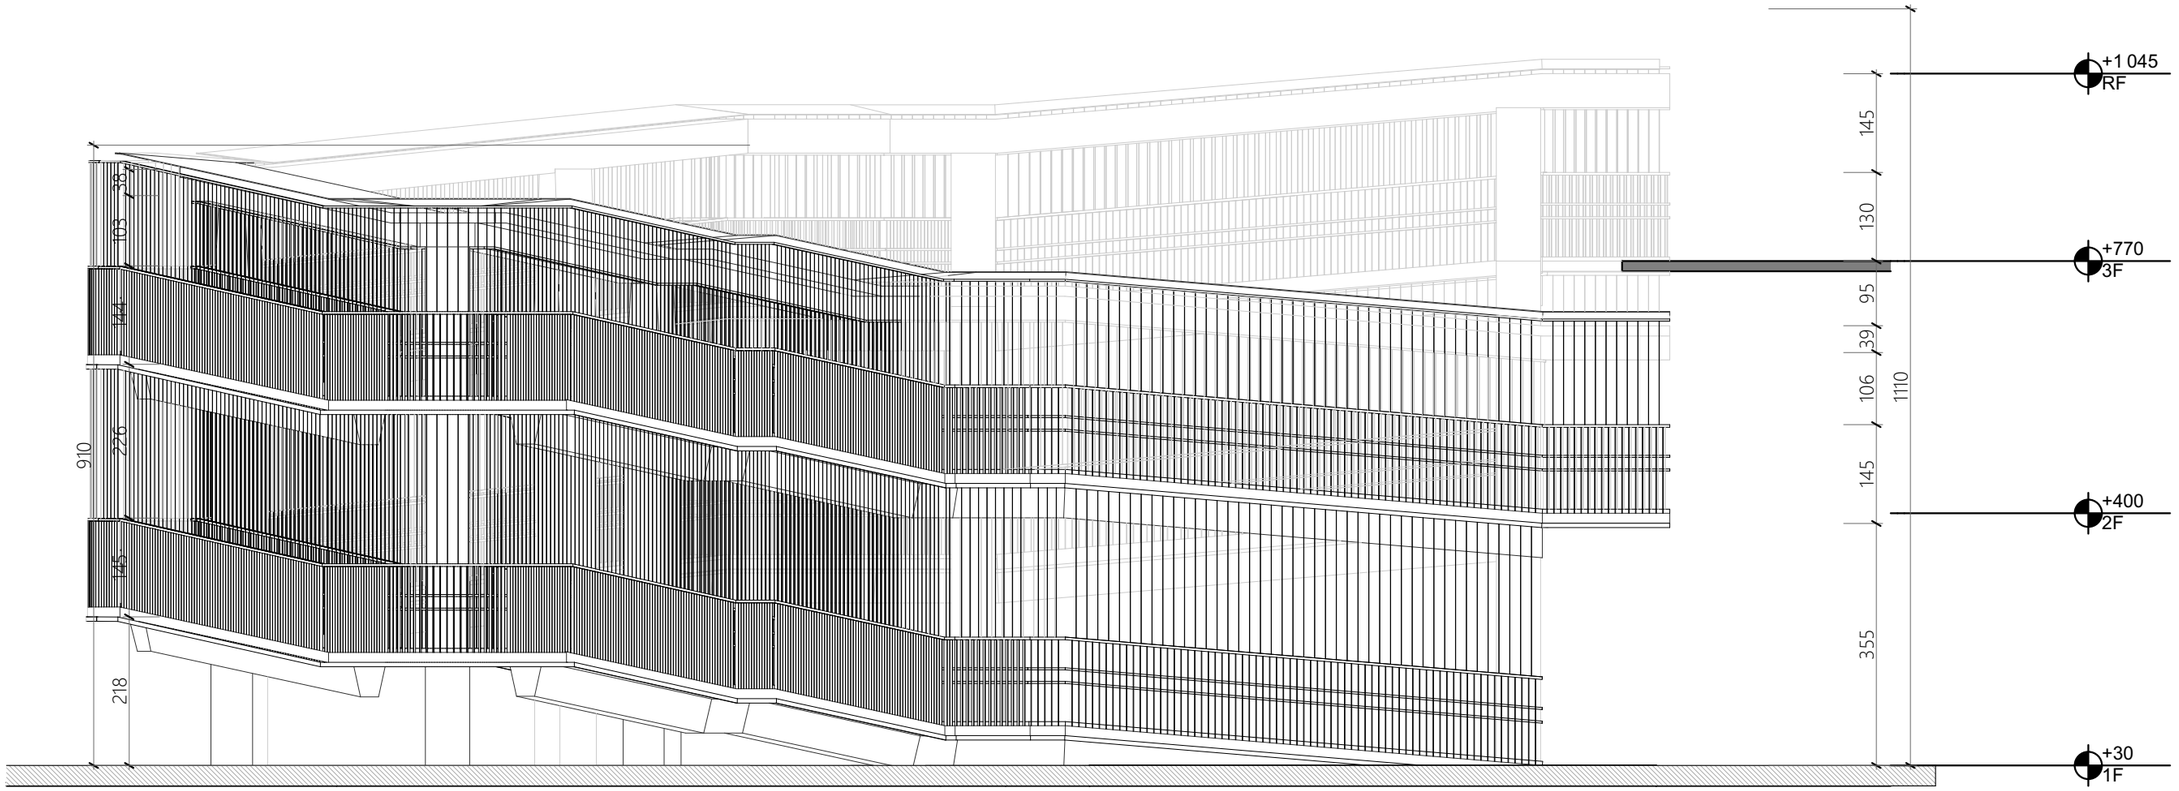


西向立面

S=1:90.00

1

ATELIER	notes 細部設計圖	Project 學校環境設施無障礙逃生坡道增建工程	Scale	Title 西向立面	Layout ID A3.2	9/28	Date 2026/10/2

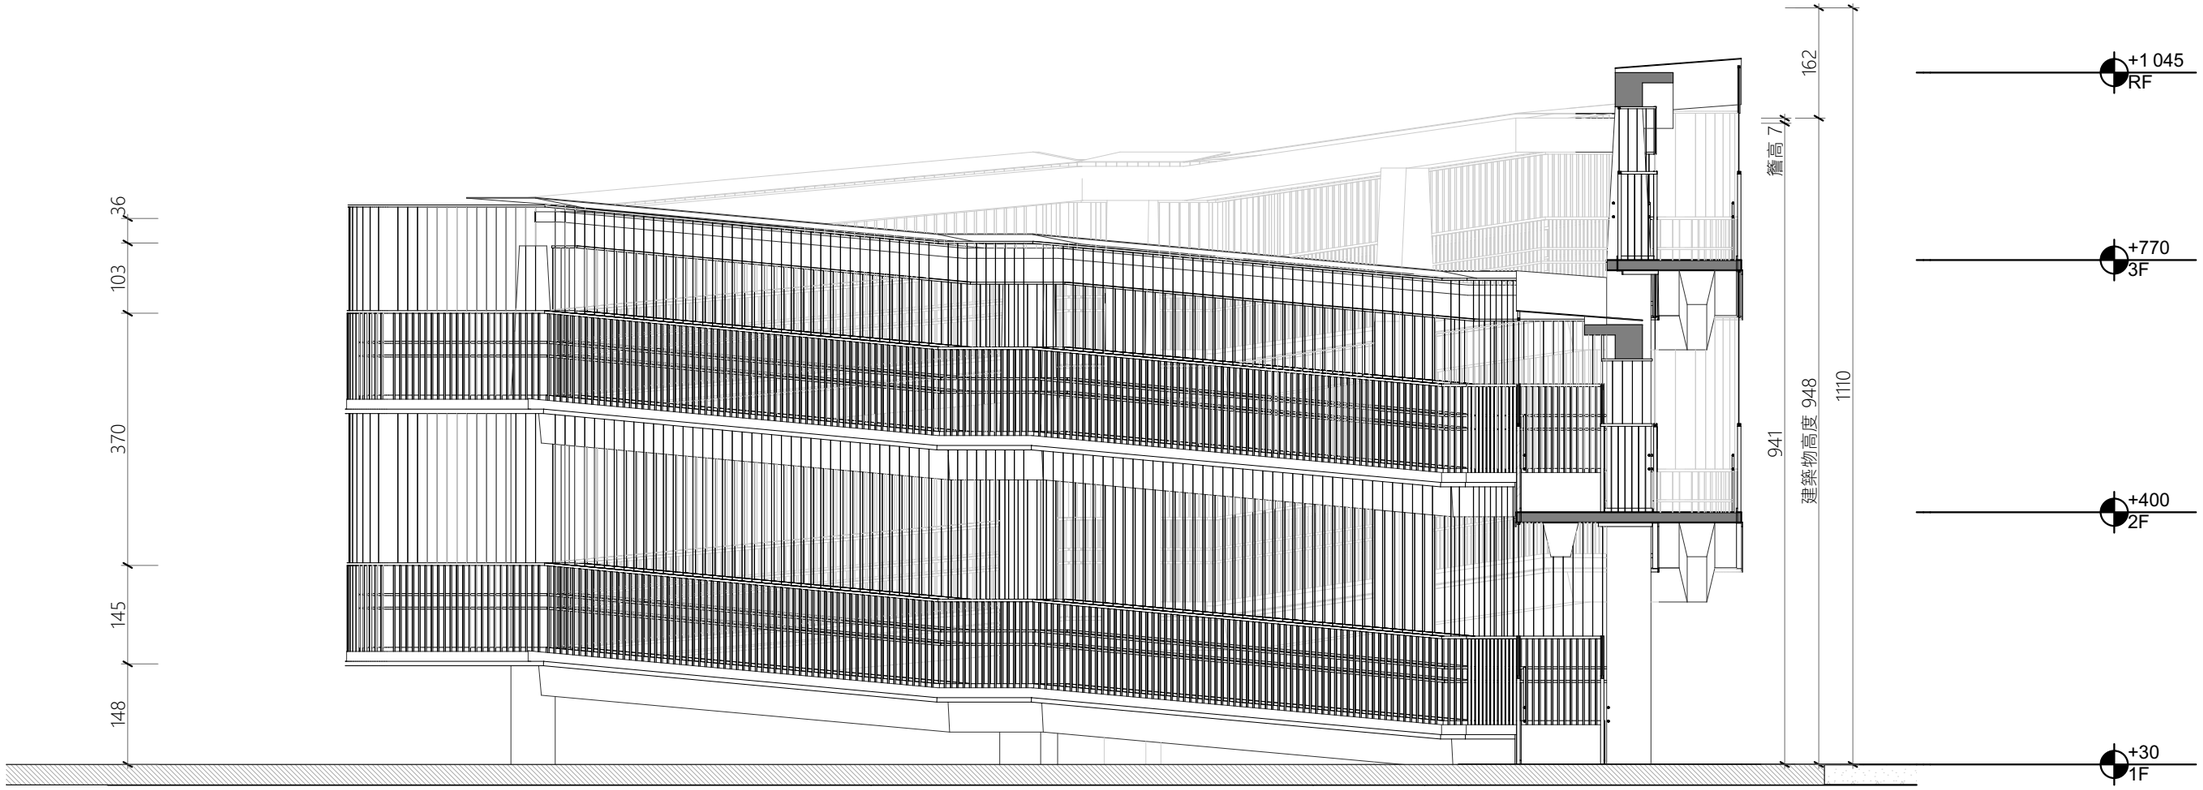


南向立面
S=1:90.00

1

ATELIER	notes 細部設計圖	Project 學校環境設施無障礙逃生坡道增建工程	Scale	Title 南向立面	Layout ID A3.3	10/28	Date 2026/10/2


1 2 3 4 5

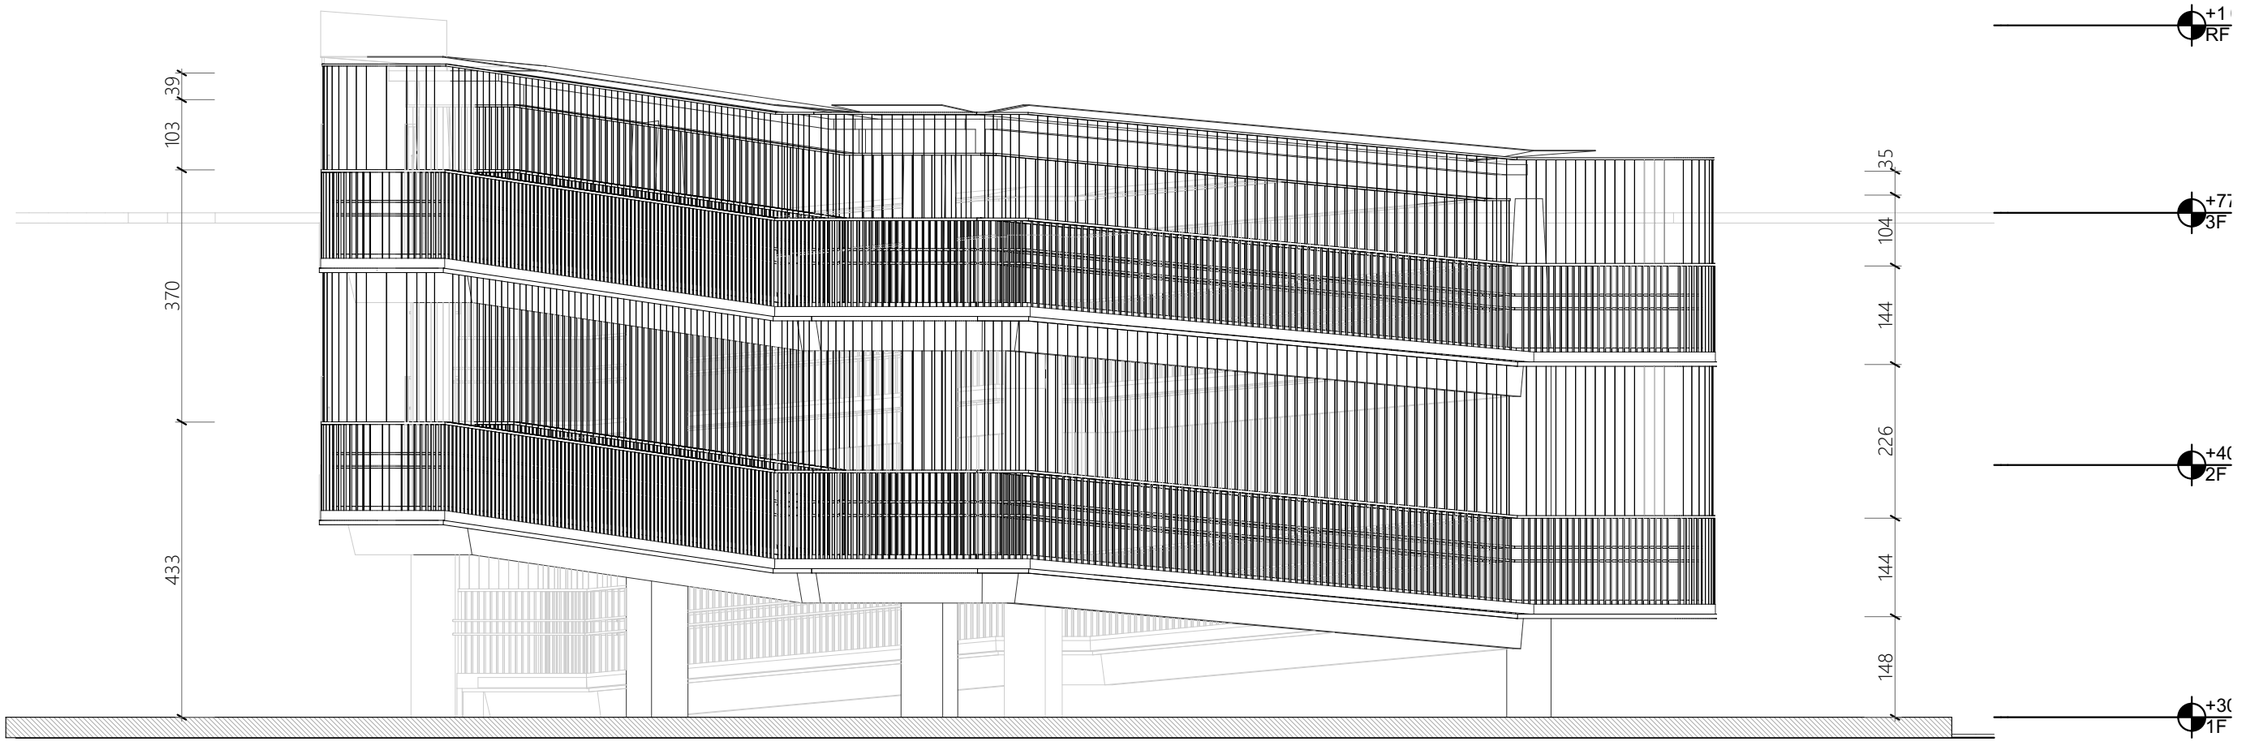

北向立面
S=1:90.00

1


ATELIER	notes 細部設計圖	Project 學校環境設施無障礙逃生坡道增建工程	Scale	Title 北向立面	Layout ID A3.4	11/28	Date 2026/10/2

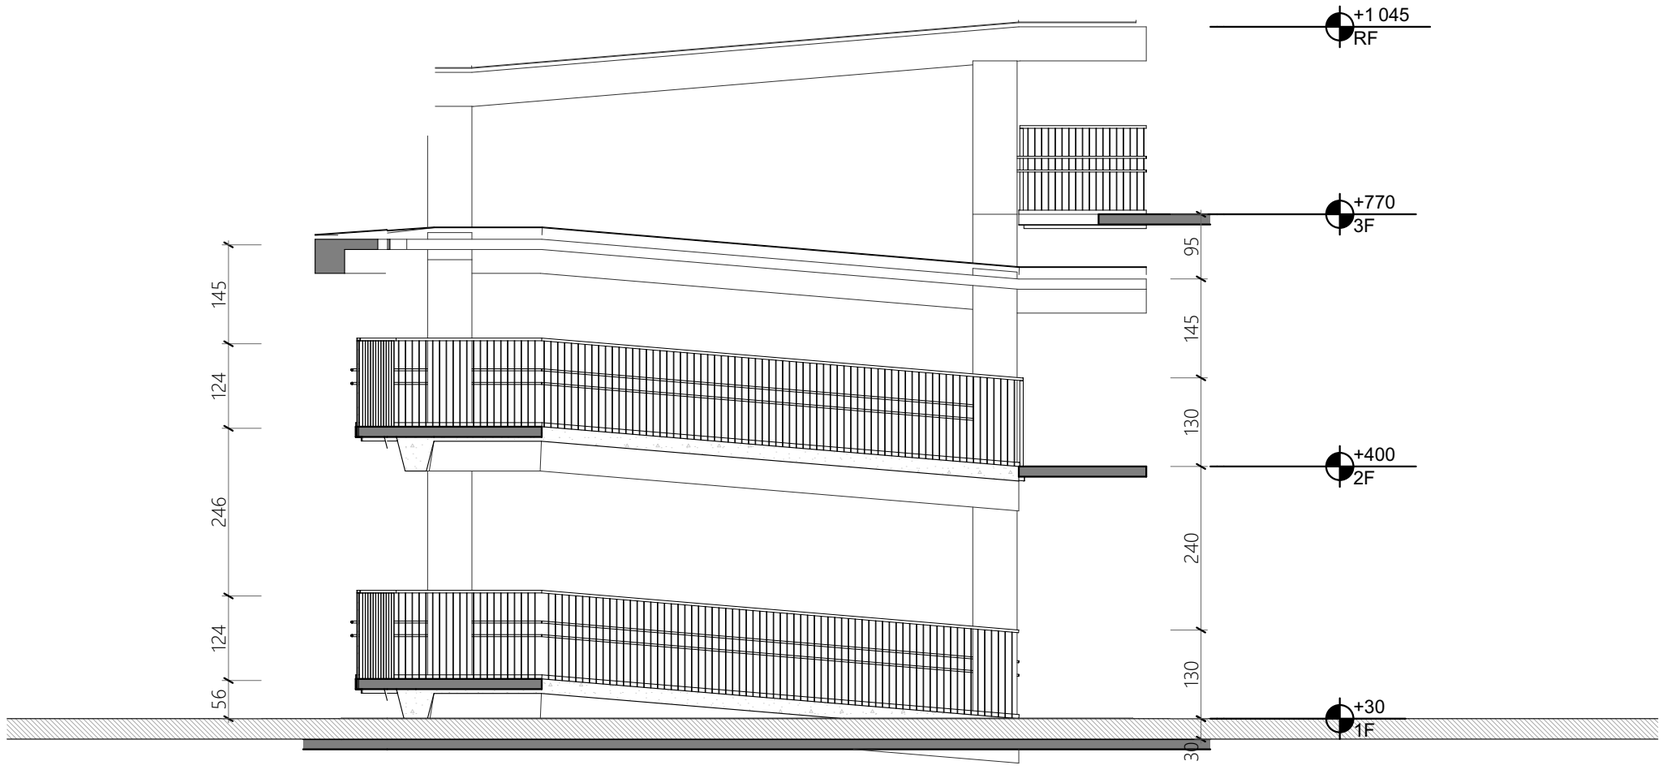

S1 縱向剖面
S=1:90.00

1


ATELIER	notes 細部設計圖	Project 學校環境設施無障礙逃生坡道增建工程	Scale	Title S1縱向剖面	Layout ID A4.1	12/28	Date 2026/10/2

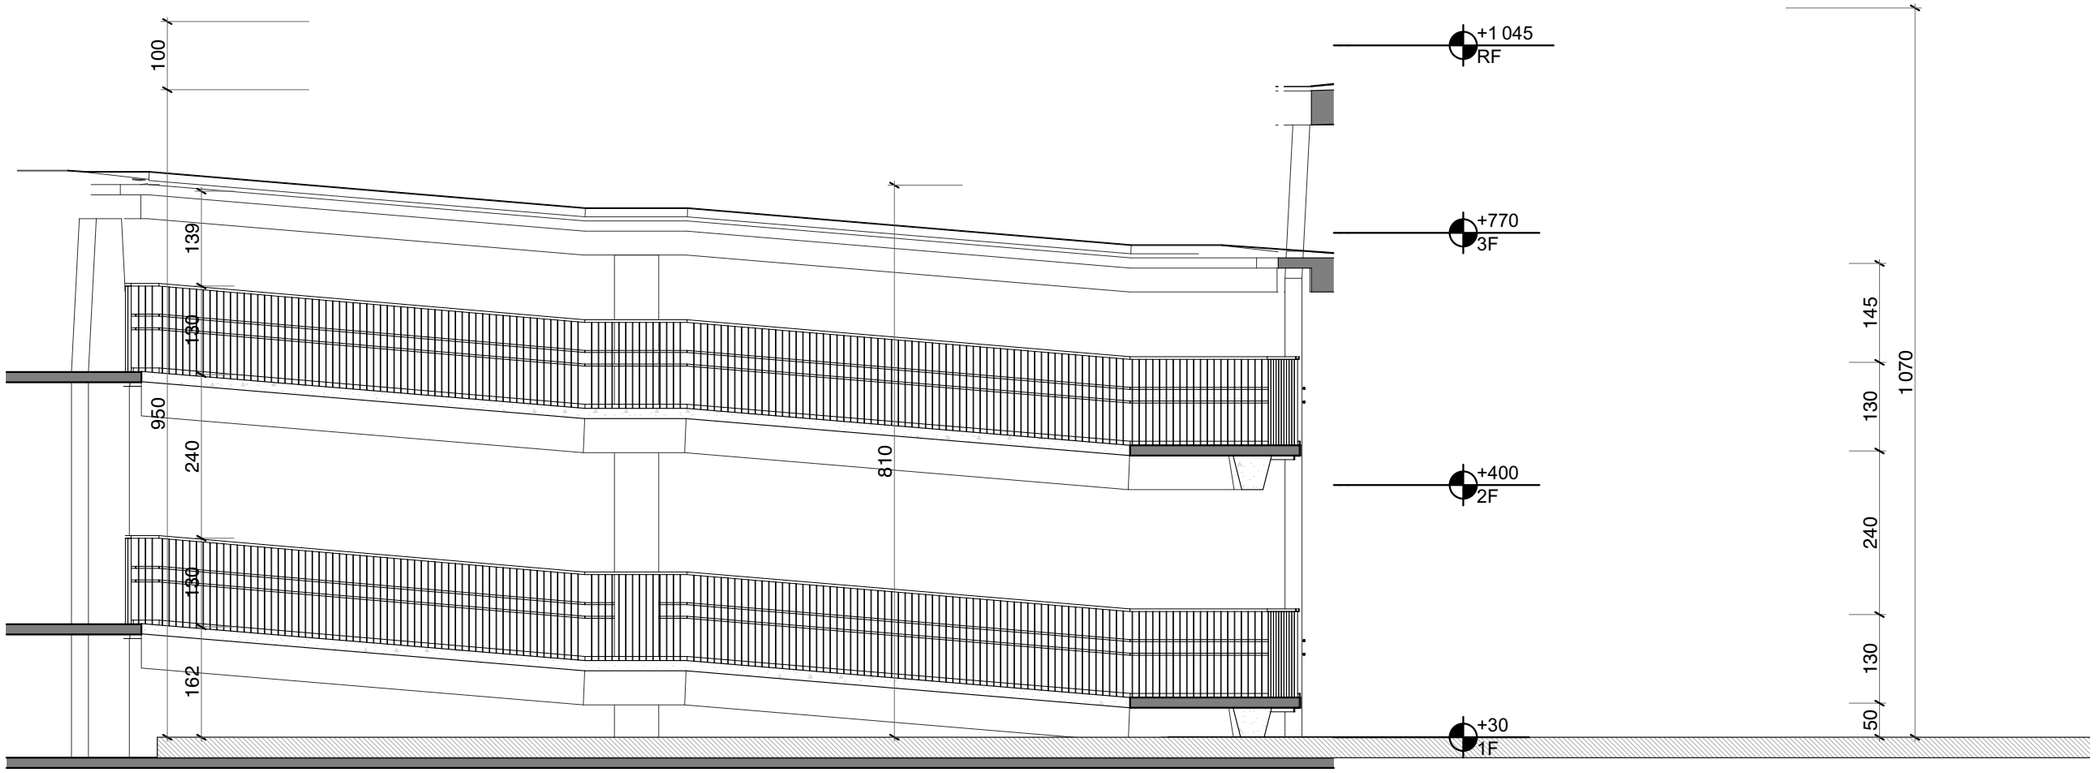

S2 縱向剖面
S=1:90.00

1


ATELIER	notes 細部設計圖	Project 學校環境設施無障礙逃生坡道增建工程	Scale	Title S2縱向剖面	Layout ID A4.2	13/28	Date 2026/10/2

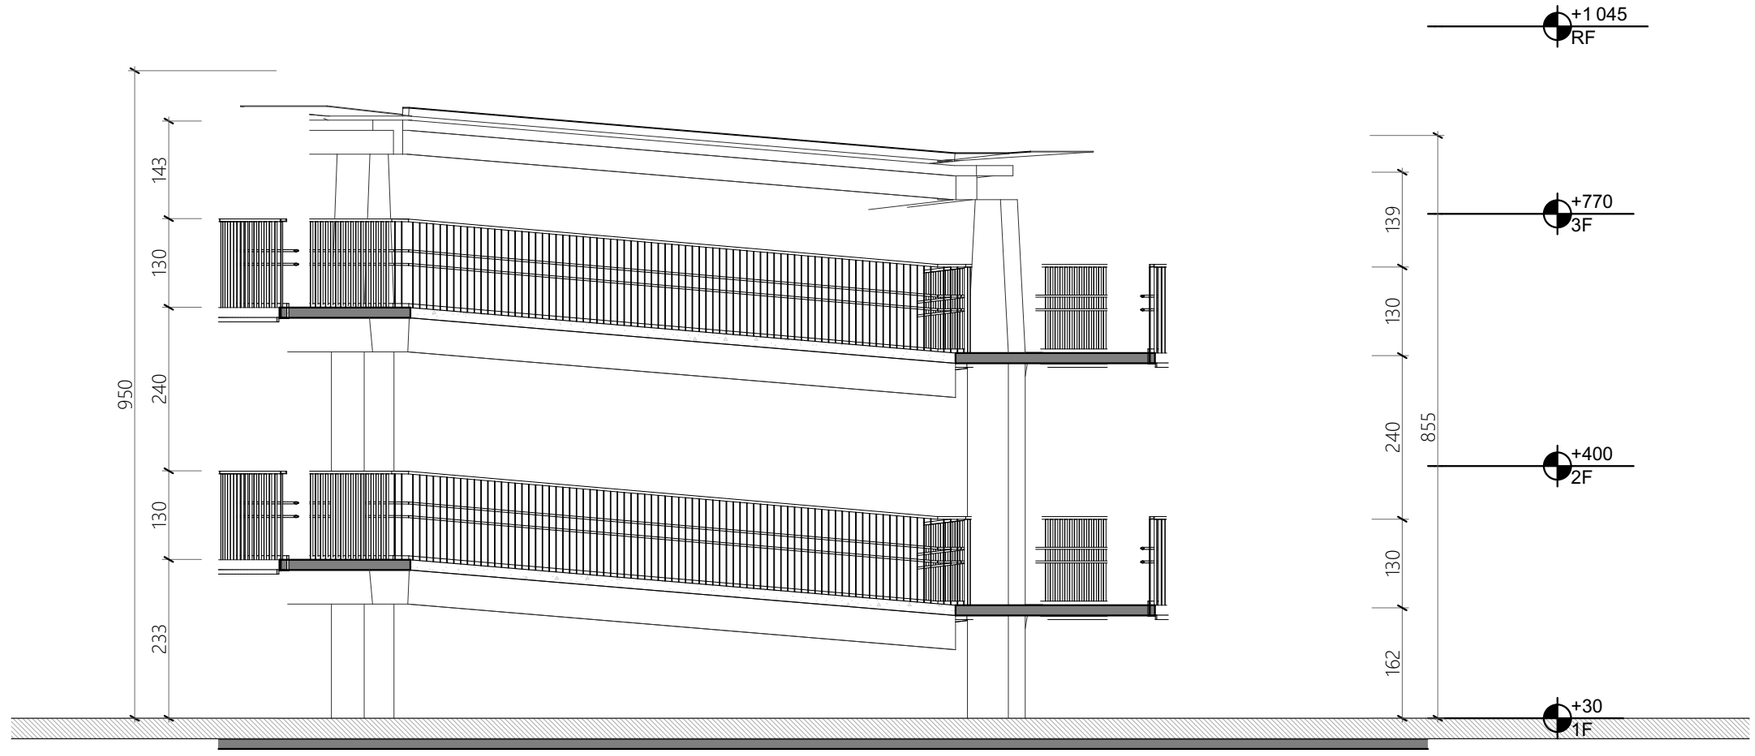

S3 縱向剖面
S=1:90.00

1


ATELIER	notes 細部設計圖	Project 學校環境設施無障礙逃生坡道增建工程	Scale	Title S3縱向剖面	Layout ID A4.3	14/28	Date 2026/10/2

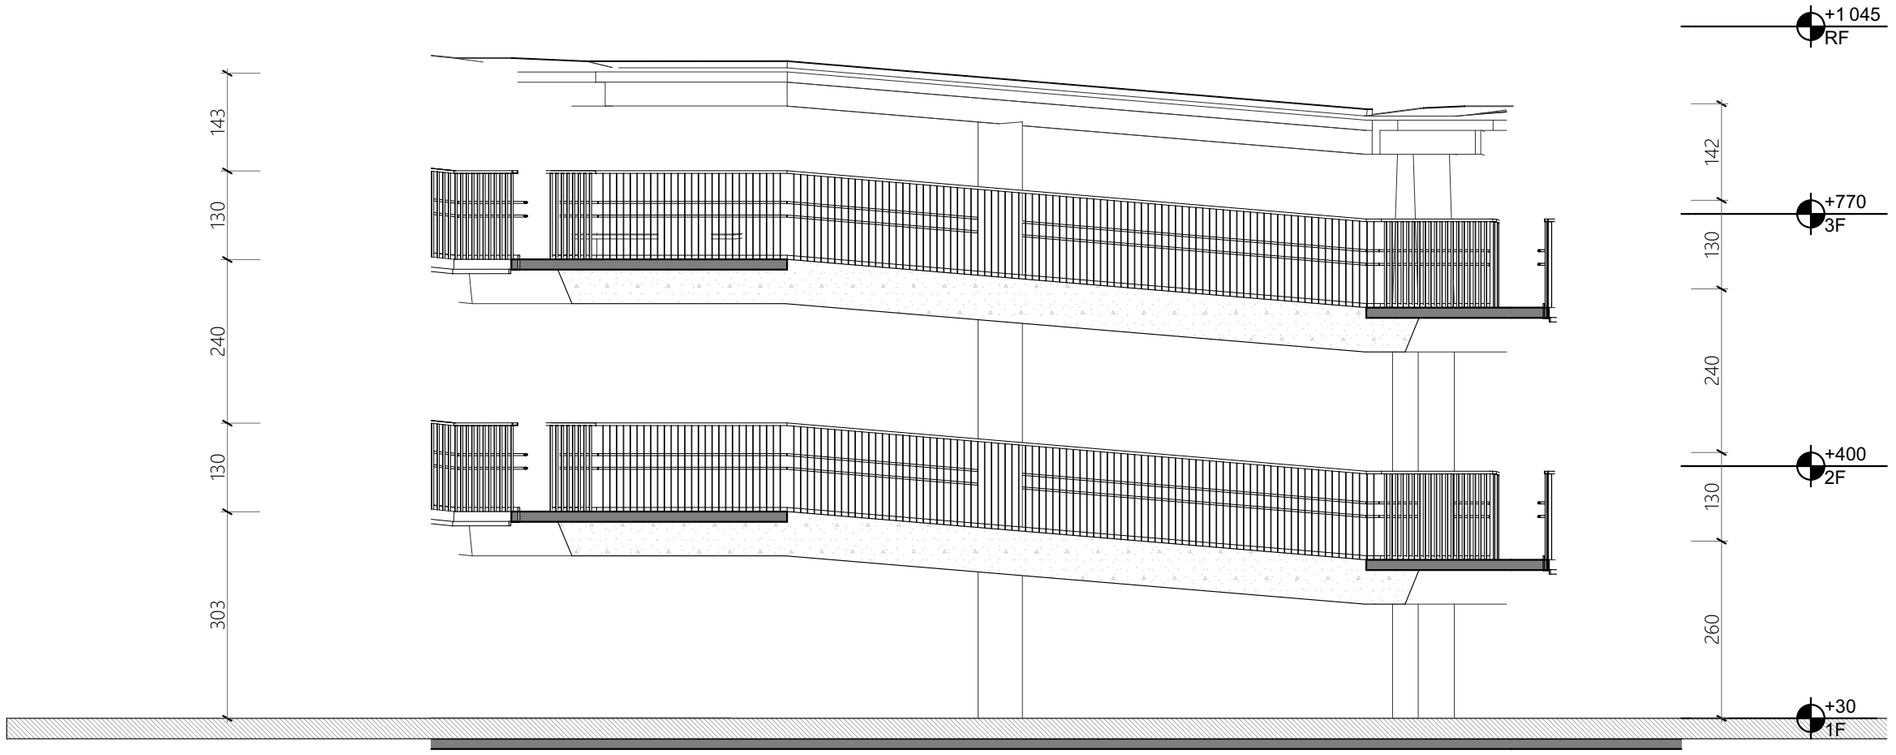

S4 縱向剖面
S=1:90.00

1


ATELIER	notes 細部設計圖	Project 學校環境設施無障礙逃生坡道增建工程	Scale	Title S4縱向剖面	Layout ID A4.4	15/28	Date 2026/10/2

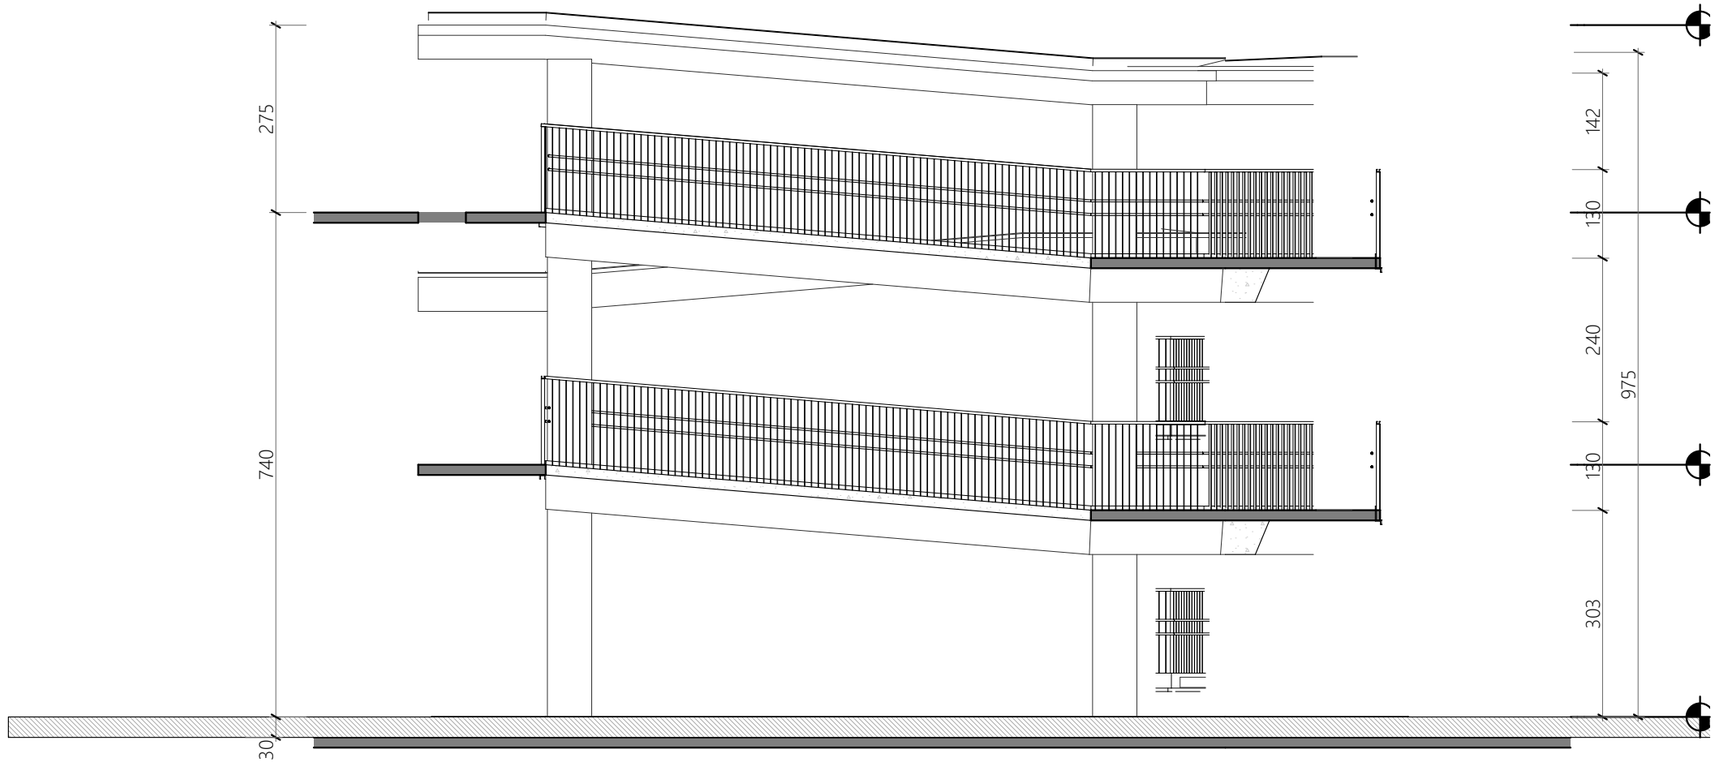


S5 縱向剖面
S=1:90.00

1


ATELIER	notes 細部設計圖	Project 學校環境設施無障礙逃生坡道增建工程	Scale	Title S5縱向剖面	Layout ID A4.5	16/28	Date 2026/10/2

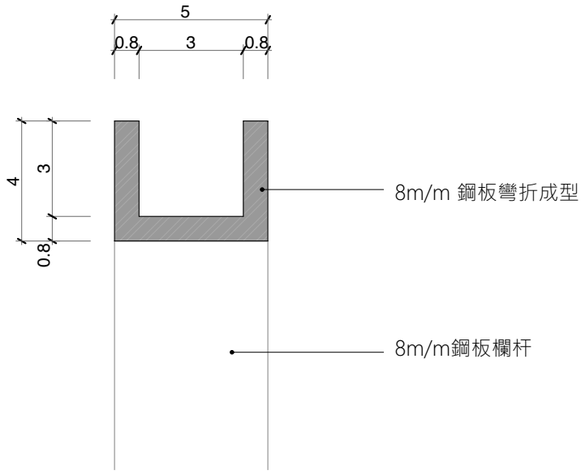

欄杆內側頂端詳圖 2
S=1:2

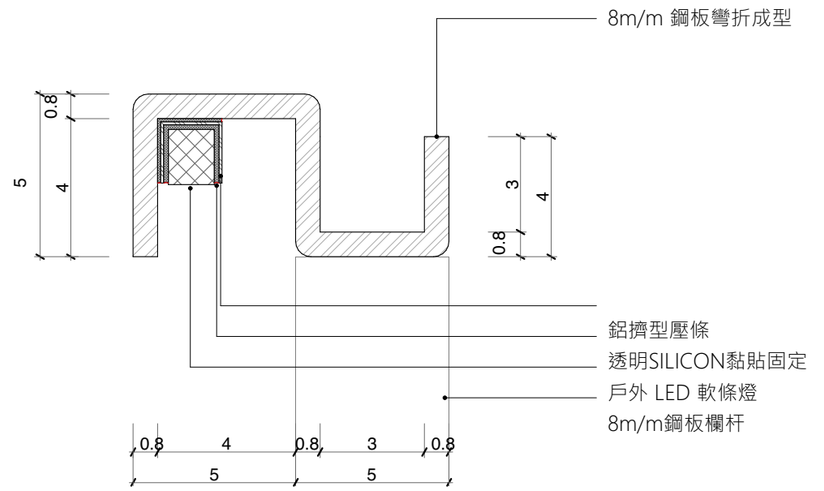


欄杆外側頂端詳圖 1
S=1:2

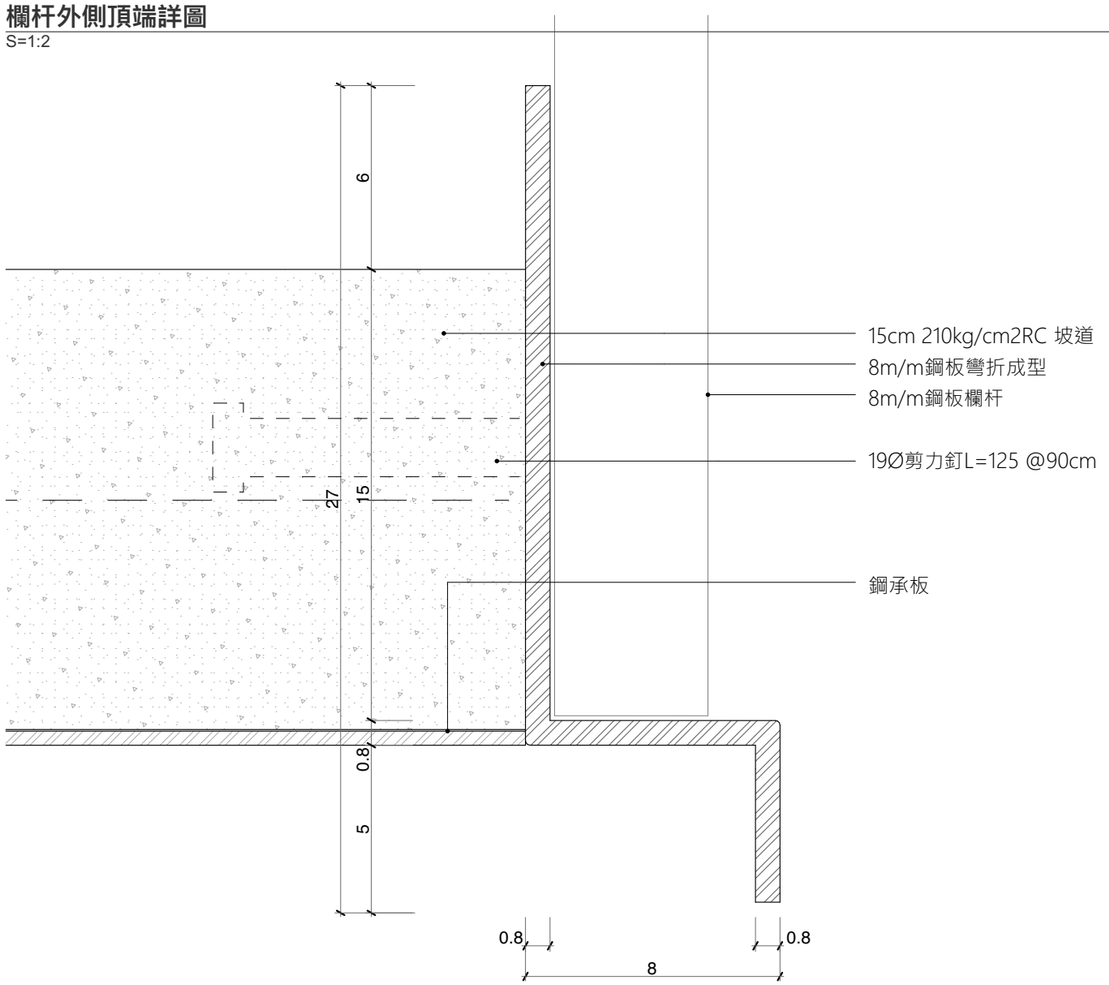


扶手底部坡道收邊詳圖 1
S=1:2

ATELIER	notes 細部設計圖	Project 學校環境設施無障礙逃生坡道增建工程	Scale	Title 欄杆詳圖一	Layout ID D.1	17/28	Date 2026/10/2

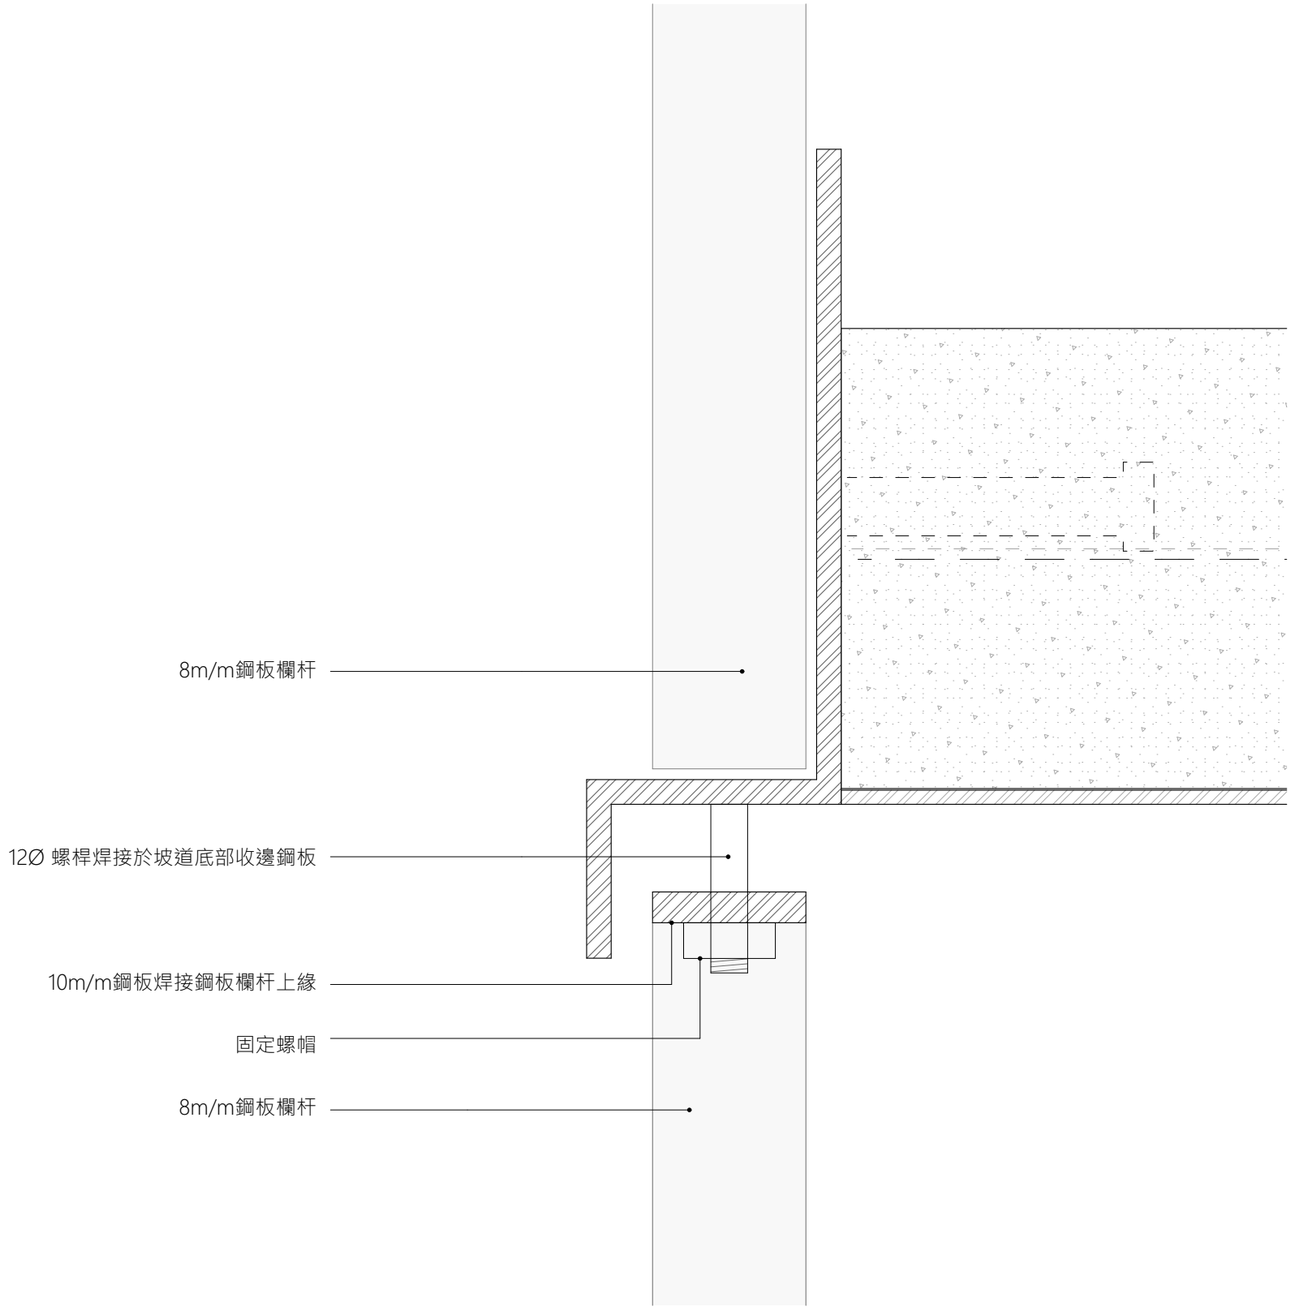

鋼板欄杆上緣固定件
S=1:2


2

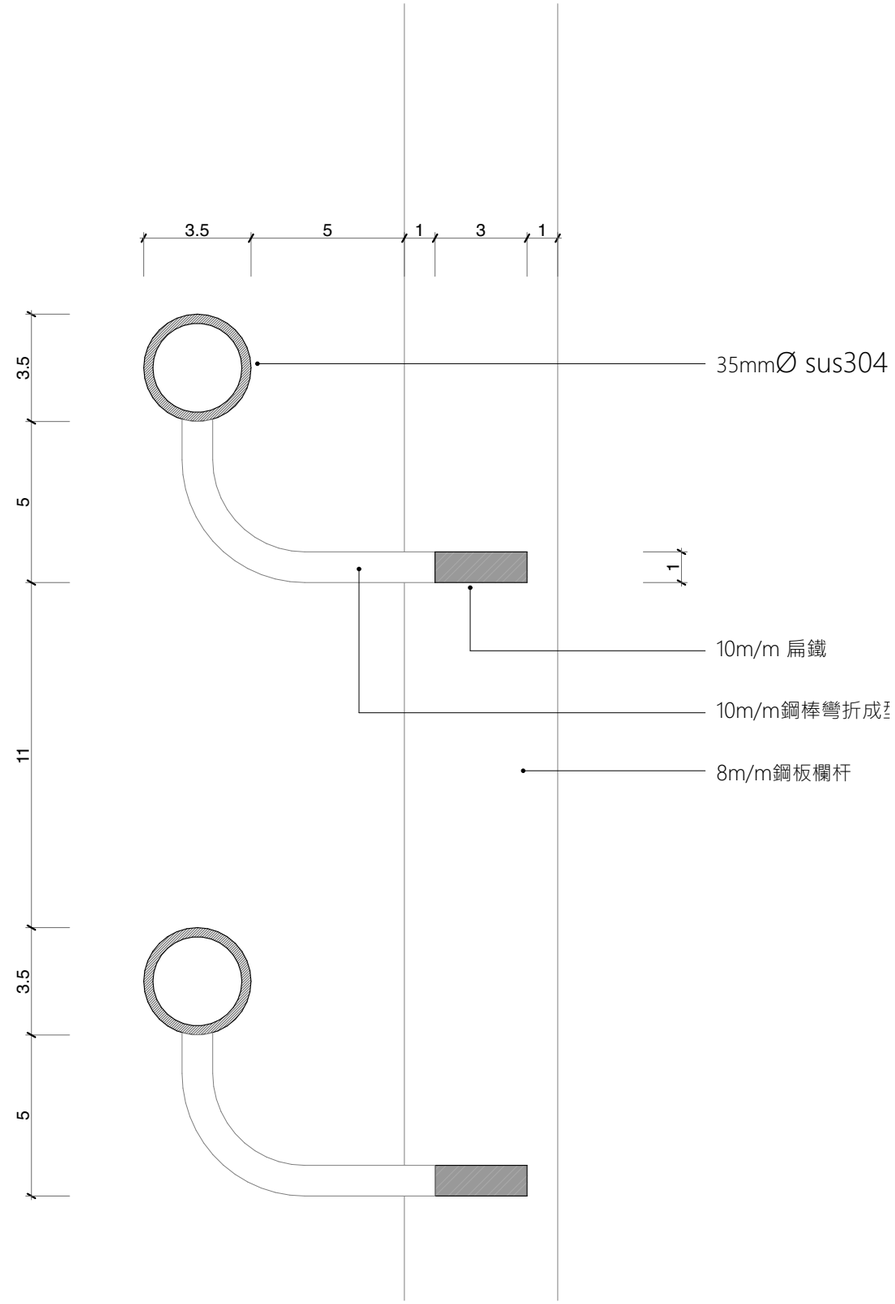


無障礙扶手詳圖
S=1:2

1

ATELIER	notes 細部設計圖	Project 學校環境設施無障礙逃生坡道增建工程	Scale	Title 欄杆詳圖二	Layout ID D.2	18/28	Date 2026/10/2

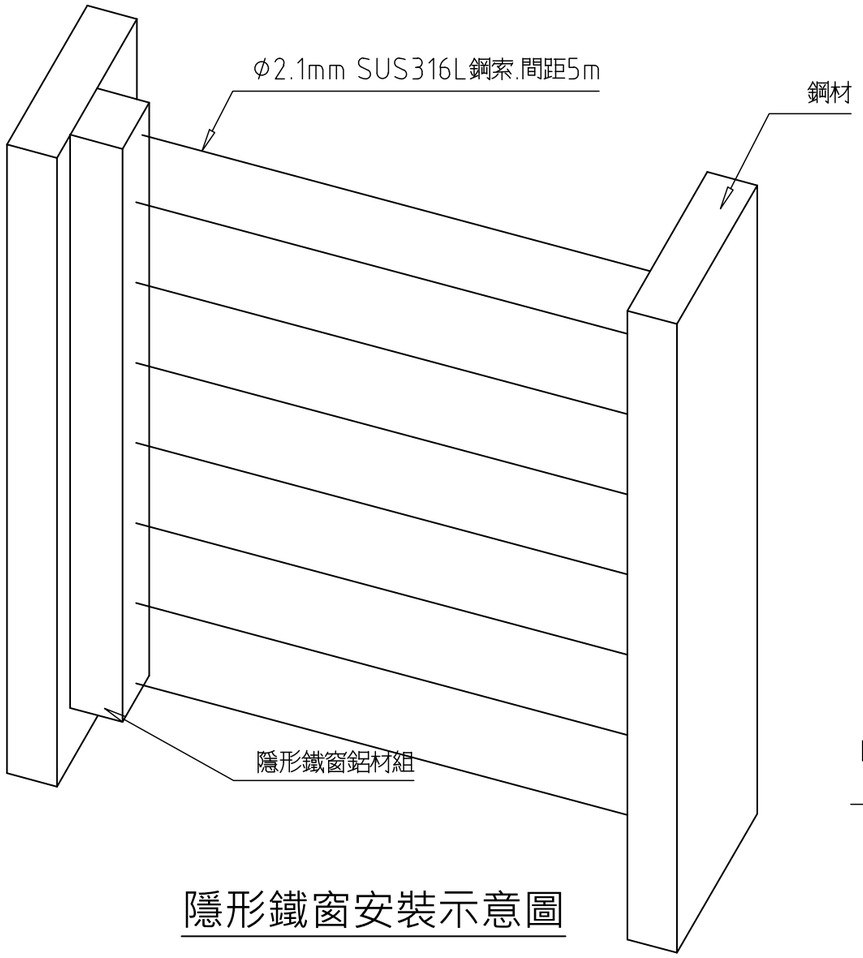

隱形鐵窗安裝示意圖

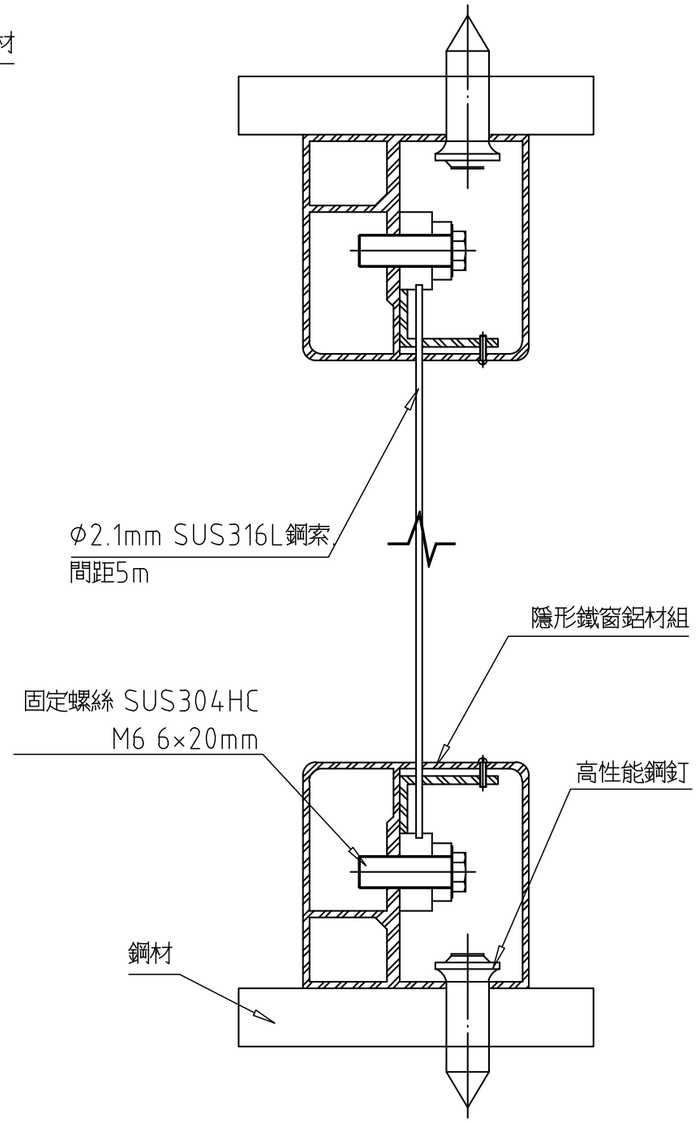

隱形鐵窗參考示意圖

隱形鐵窗產品規範	
鋁合金骨料	材質：鋁鎂合金6063 T5
	鋁合金尺寸：底座3.2CM×高3.0CM
	硬度：符合偉柏硬度12~16度以上要求
鋁合金骨料 封邊蓋	尼龍材質，寬3.2CM×高3.0CM×深0.5CM
	6063T5材質，寬3.2CM×高3.0CM×深0.5~1.5CM
	視環境需求擇一使用
鋼索線材	採用台灣製高品質SUS316L Ø2.1mm線徑
	外層採用工業等級尼龍12(NY12) 批覆膜防割手
	TAF認證實驗室 抗拉試驗：180kgf
	試驗速率20mm/mim
固定螺絲	SUS304HC M6×20
	不易斷裂，抗腐蝕性好
螺絲固定件	黑白墊片， P.O.M塑膠
	強化塑膠底座 W：2cm×2cm×H0.9cm
	N66 BK W：1.8cm×1.8cm×H0.7cm


施工規範：

一.隱形鐵窗(含工資及安裝)一式，隱形鐵窗尺寸(寬*高cm)樘。


二.廠商應先提供選材料樣品.型錄及測試報告，經業主或甲方認可後可後方可施作。

三.材料到達現場應與樣品相符，需經業主或甲方監造許可後方可施作。

高性能鋼釘	
基礎材料	鋼材
基材最小厚度	鋼材厚4 mm
腐蝕防護	鍍鋅塗層 < 20 μm
環境狀況	乾燥的室內
材料	碳鋼 鋅
緊固件柄	直徑 3 mm
定點類型	長錐形頭
認證	ICC-ES

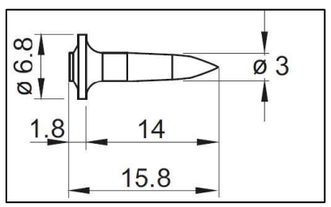


高性能鋼釘參考示意圖

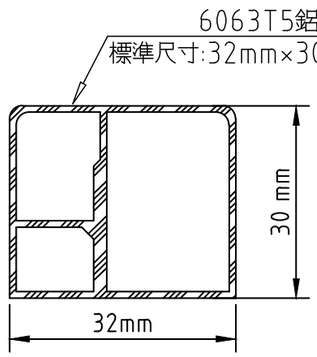


骨架鋁件參考示意圖

7*7(股數:7 每股數量7 鋼索數量合計49條)

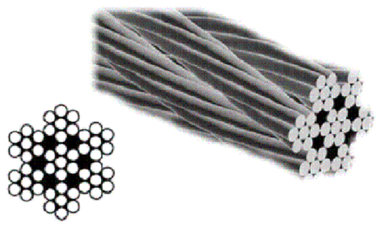

不鏽鋼索參考示意圖


ATELIER	notes 細部設計圖	Project 學校環境設施無障礙逃生坡道增建工程	Scale	Title 隱形鐵窗 詳圖	Layout ID D.3	19/28	Date 2026/10/2

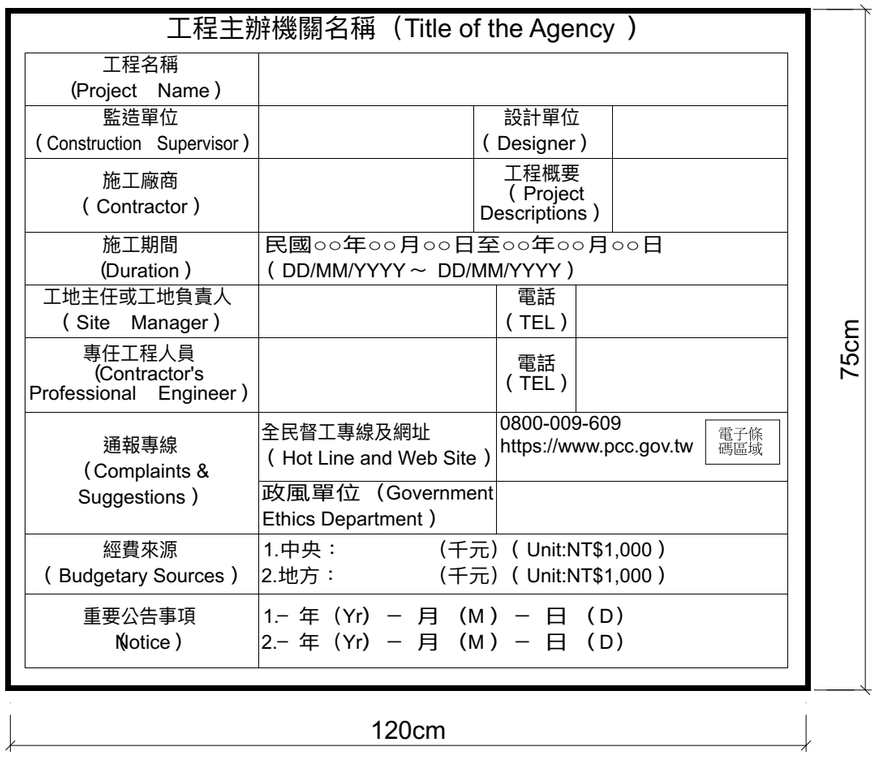

工程告示牌示意圖

S=1:100

1

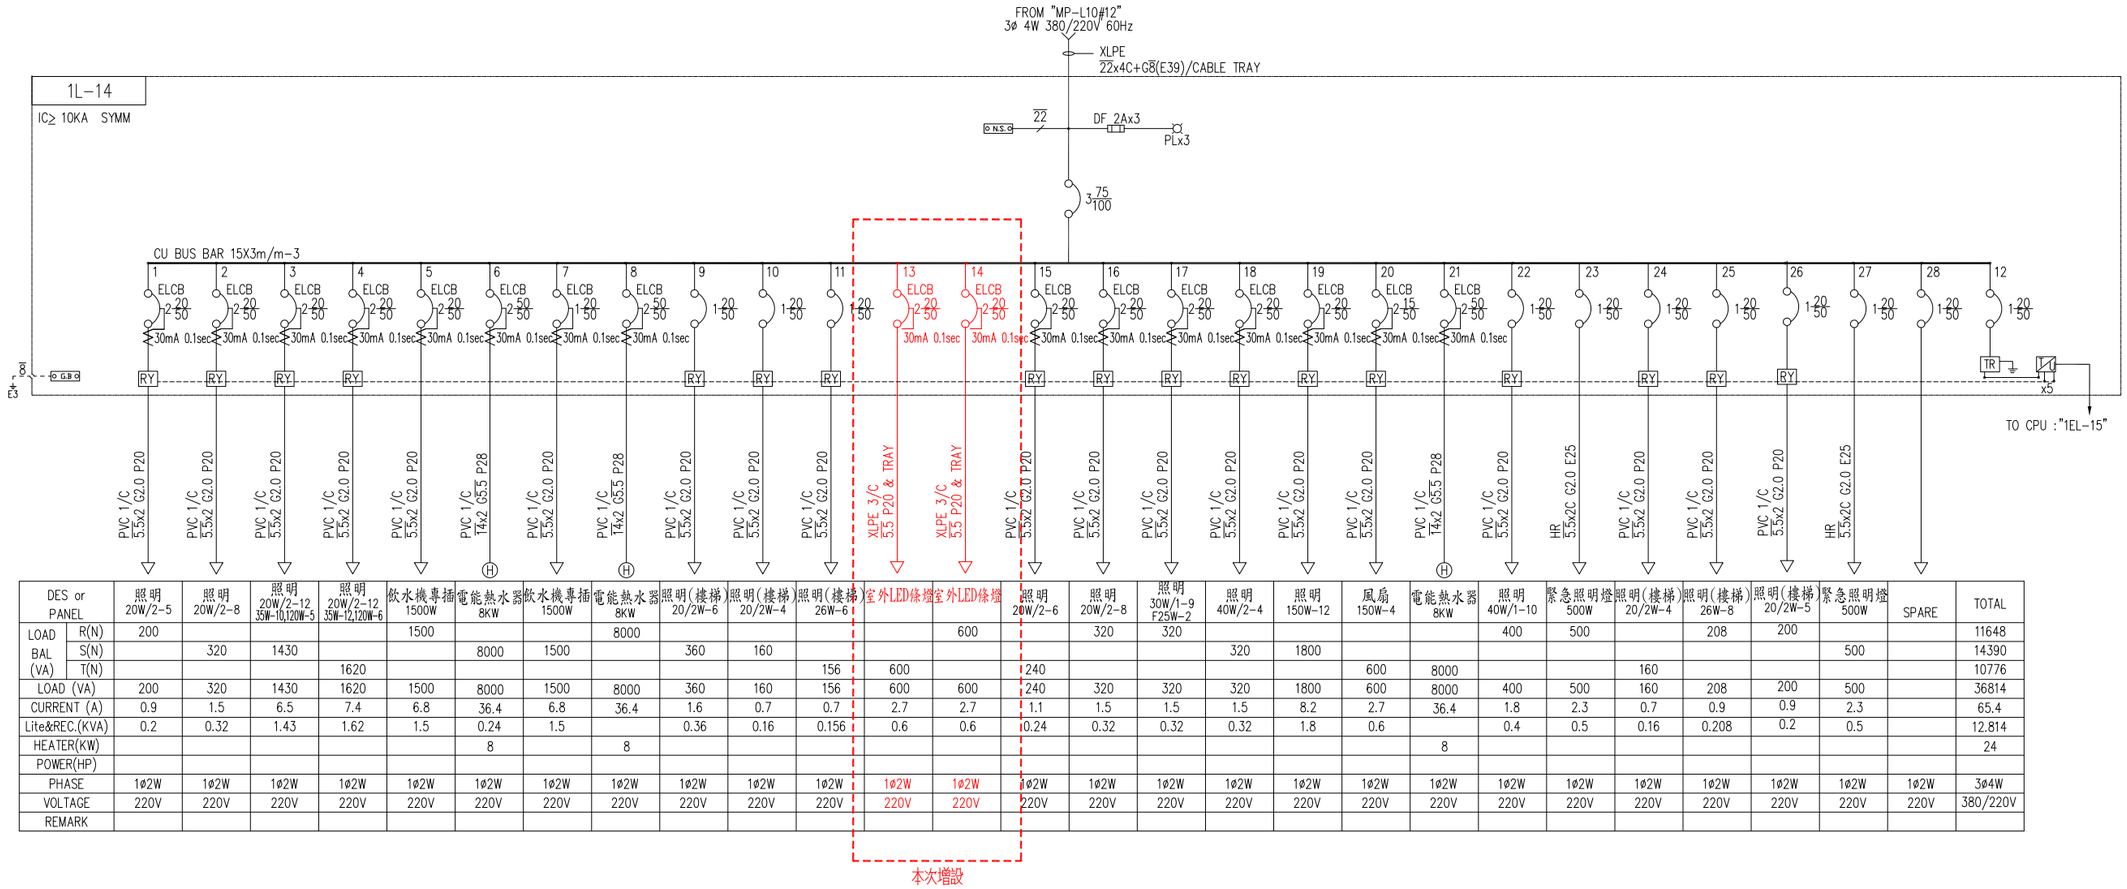


DES or PANEL		照明 20W/2-5	照明 20W/2-8	照明 20W/2-12 35W-10,12W-5	照明 20W/2-12 35W-12,12W-6	飲水機專插 1500W	電能熱水器 8KW	飲水機專插 1500W	電能熱水器 8KW	照明(樓梯) 20/2W-6	照明(樓梯) 20/2W-4	照明(樓梯) 26W-6	室外LED條燈	室外LED條燈	照明 20W/2-6	照明 20W/2-8	照明 30W/1-9 F25W-2	照明 40W/2-4	照明 150W-12	風扇 150W-4	電能熱水器 8KW	照明 40W/1-10	緊急照明燈 500W	照明(樓梯) 20/2W-4	照明(樓梯) 26W-8	照明(樓梯) 20/2W-5	緊急照明燈 500W	SPARE	TOTAL
LOAD BAL (VA)	R(N)	200				1500			8000					600		320	320					400	500		208	200			11648
	S(N)		320	1430			8000	1500		360	160							320	1800								500		14390
	T(N)				1620							156	600		240					600	8000			160					10776
LOAD (VA)		200	320	1430	1620	1500	8000	1500	8000	360	160	156	600	600	240	320	320	320	1800	600	8000	400	500	160	208	200	500		36814
CURRENT (A)		0.9	1.5	6.5	7.4	6.8	36.4	6.8	36.4	1.6	0.7	0.7	2.7	2.7	1.1	1.5	1.5	1.5	8.2	2.7	36.4	1.8	2.3	0.7	0.9	0.9	2.3		65.4
Lite&REC.(KVA)		0.2	0.32	1.43	1.62	1.5	0.24	1.5		0.36	0.16	0.156	0.6	0.6	0.24	0.32	0.32	0.32	1.8	0.6		0.4	0.5	0.16	0.208	0.2	0.5		12.814
HEATER(KW)							8		8												8								24
POWER(HP)																													
PHASE		1ø2W	1ø2W	1ø2W	1ø2W	1ø2W	1ø2W	1ø2W	1ø2W	1ø2W	1ø2W	1ø2W	1ø2W	1ø2W	1ø2W	1ø2W	1ø2W	1ø2W	1ø2W	1ø2W	1ø2W	1ø2W	1ø2W	1ø2W	1ø2W	1ø2W	1ø2W	1ø2W	3ø4W
VOLTAGE		220V	220V	220V	220V	220V	220V	220V	220V	220V	220V	220V	220V	220V	220V	220V	220V	220V	220V	220V	220V	220V	220V	220V	220V	220V	220V	220V	380/220V
REMARK																													

本次增設

單線圖


ATELIER	notes 細部設計圖	Project 學校環境設施無障礙逃生坡道增建工程	Scale	Title 照明回路單線圖	Layout ID E.1 / 21/28 / Date 2026/10/2

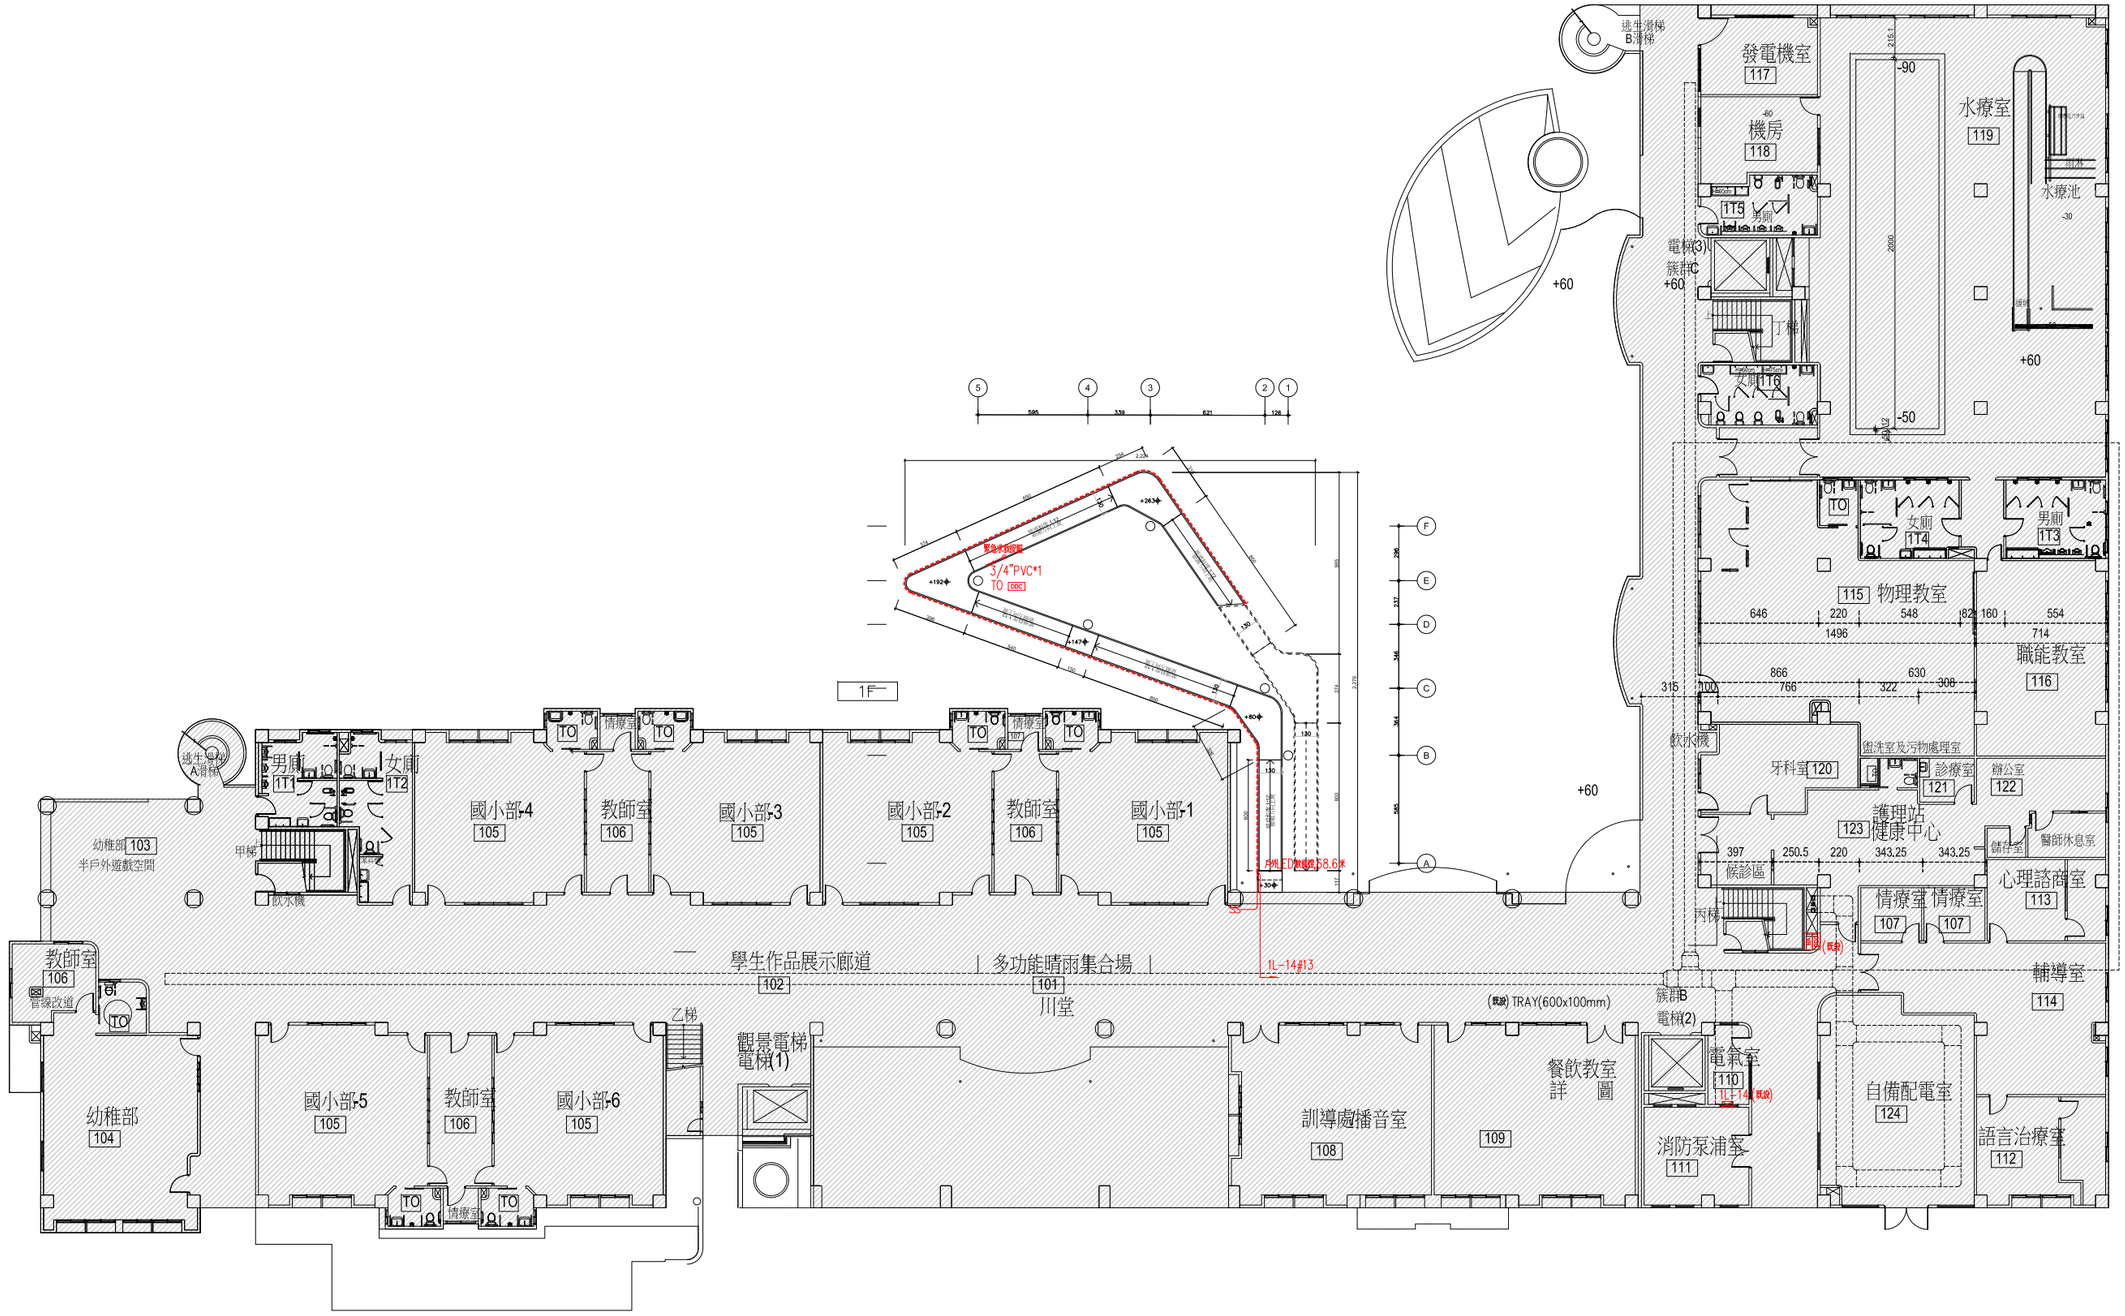

室外LED條燈 一層平面圖

S=1:1


ATELIER	notes 細部設計圖	Project 學校環境設施無障礙逃生坡道增建工程	Scale	Title 室外LED條燈 一層平面圖	Layout ID E.2	22/28	Date 2026/10/2

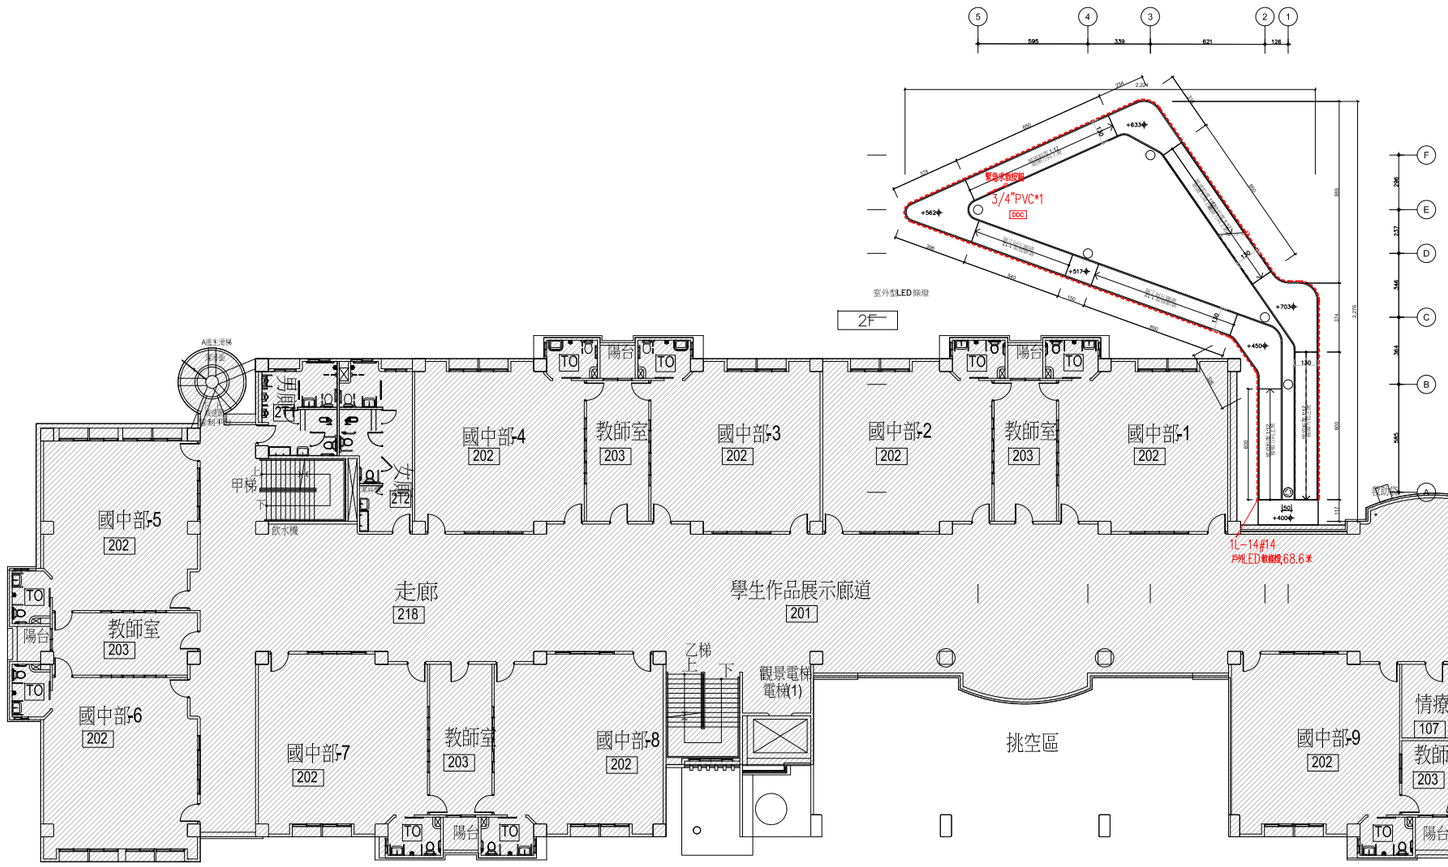

室外LED條燈 二層平面圖

S=1:1

ATELIER	notes 細部設計圖	Project 學校環境設施無障礙逃生坡道增建工程	Scale	Title 室外LED條燈 二層平面圖	Layout ID E.3	23/28	Date 2026/10/2

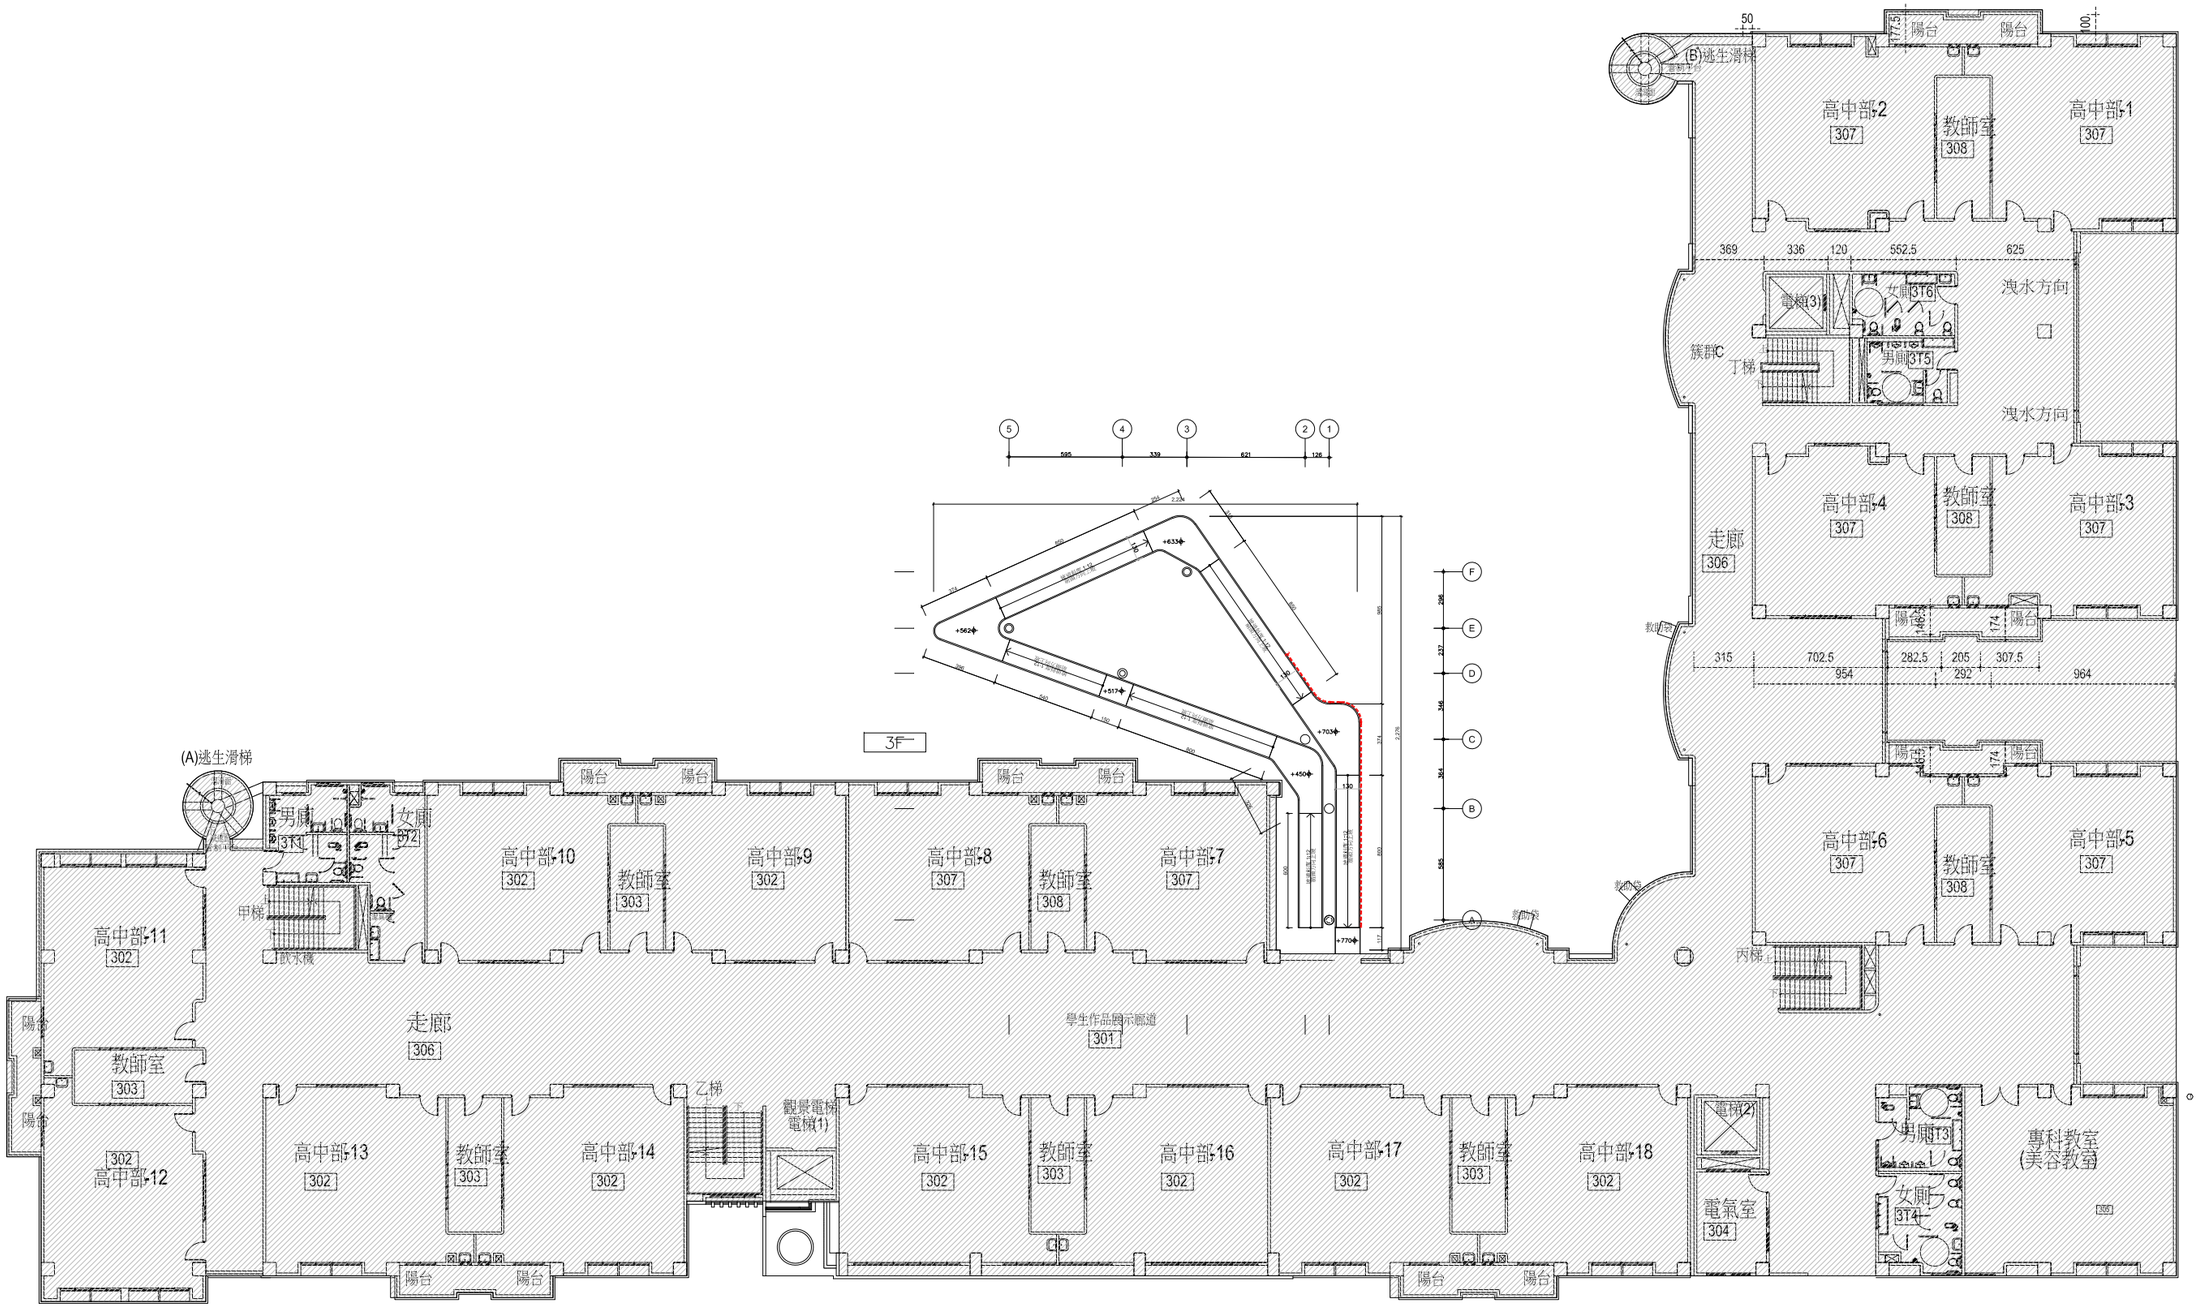


室外LED條燈 三層平面圖

S=1:1


ATELIER	notes 細部設計圖	Project 學校環境設施無障礙逃生坡道增建工程	Scale	Title 室外LED條燈 三層平面圖	Layout ID E.4	24/28	Date 2026/10/2

設備項目	種類系統	圖例	規格及說明	數量表 1F	2F	3F	合計	圖例
	滅火器	©	10型乾粉滅火器A-3 B-10 C 附[滅火器]標示牌及固定架					©
		Ⓢ	探警器5W I 級 壁掛式 92分貝以上					Ⓢ

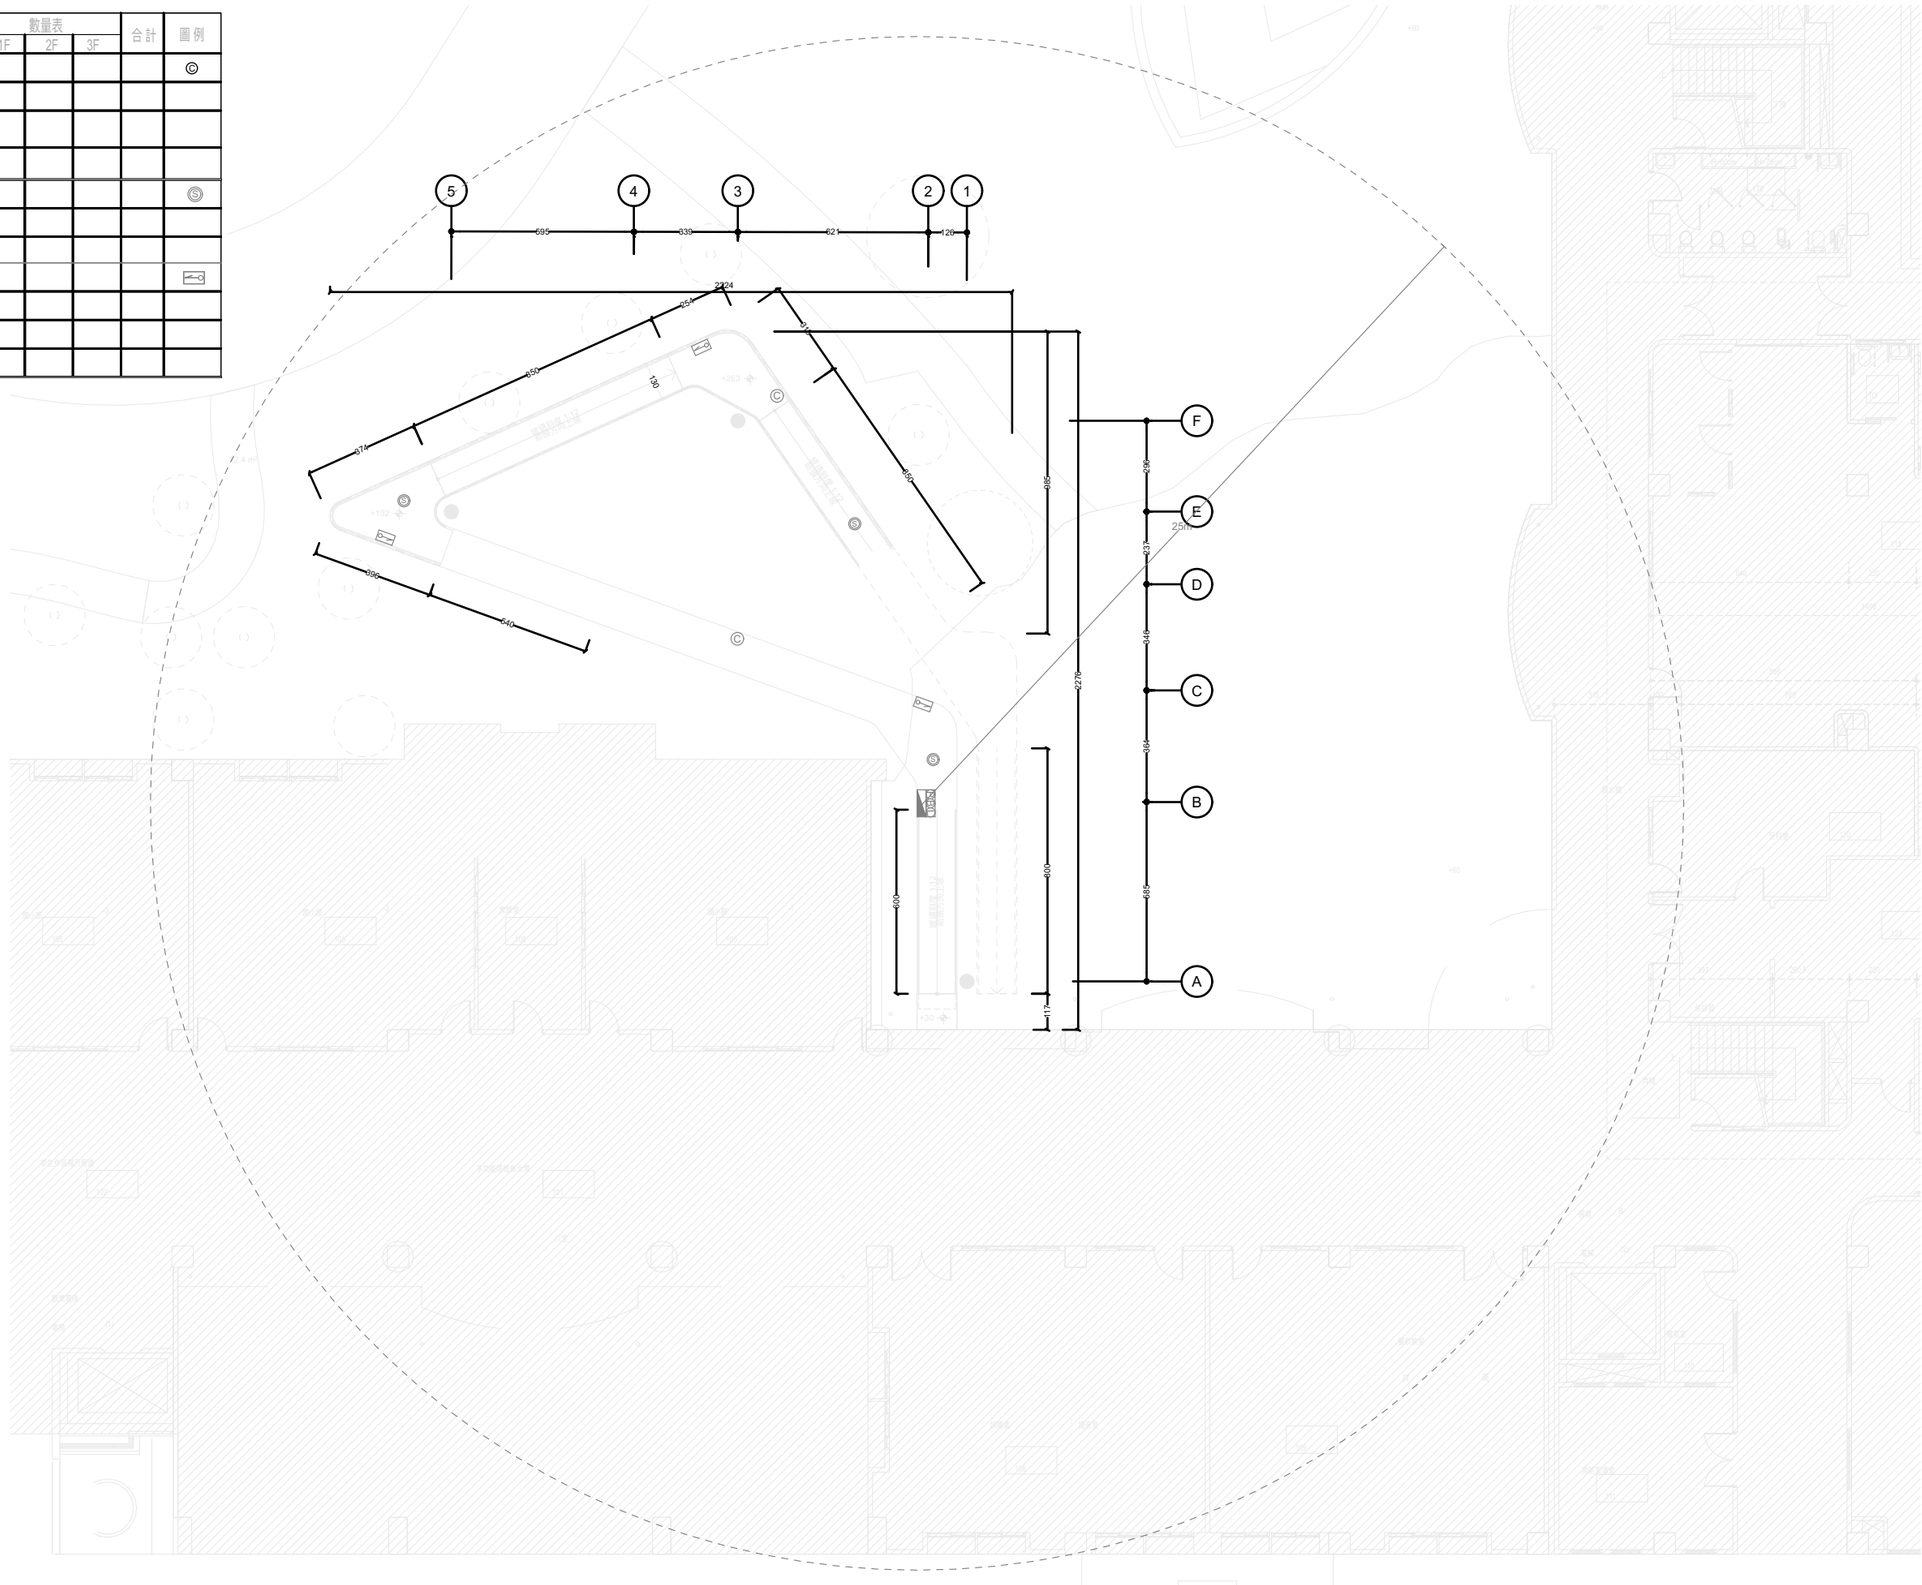


ATELIER H	notes 細部設計圖	Project 學校環境設施無障礙逃生坡道增建工程	Scale	Title 壹層消防設備平面圖	Layout ID F.1	25/28	Date 2026/10/2


設備項目	種類系統	圖例	規格及說明	數量表 1F	2F	3F	合計	圖例
	滅火器	©	10型乾粉滅火器A-3 B-10 C 附[滅火器]標示牌及固定架					©
		Ⓢ	探警器5W I 級 壁掛式 92分貝以上					Ⓢ

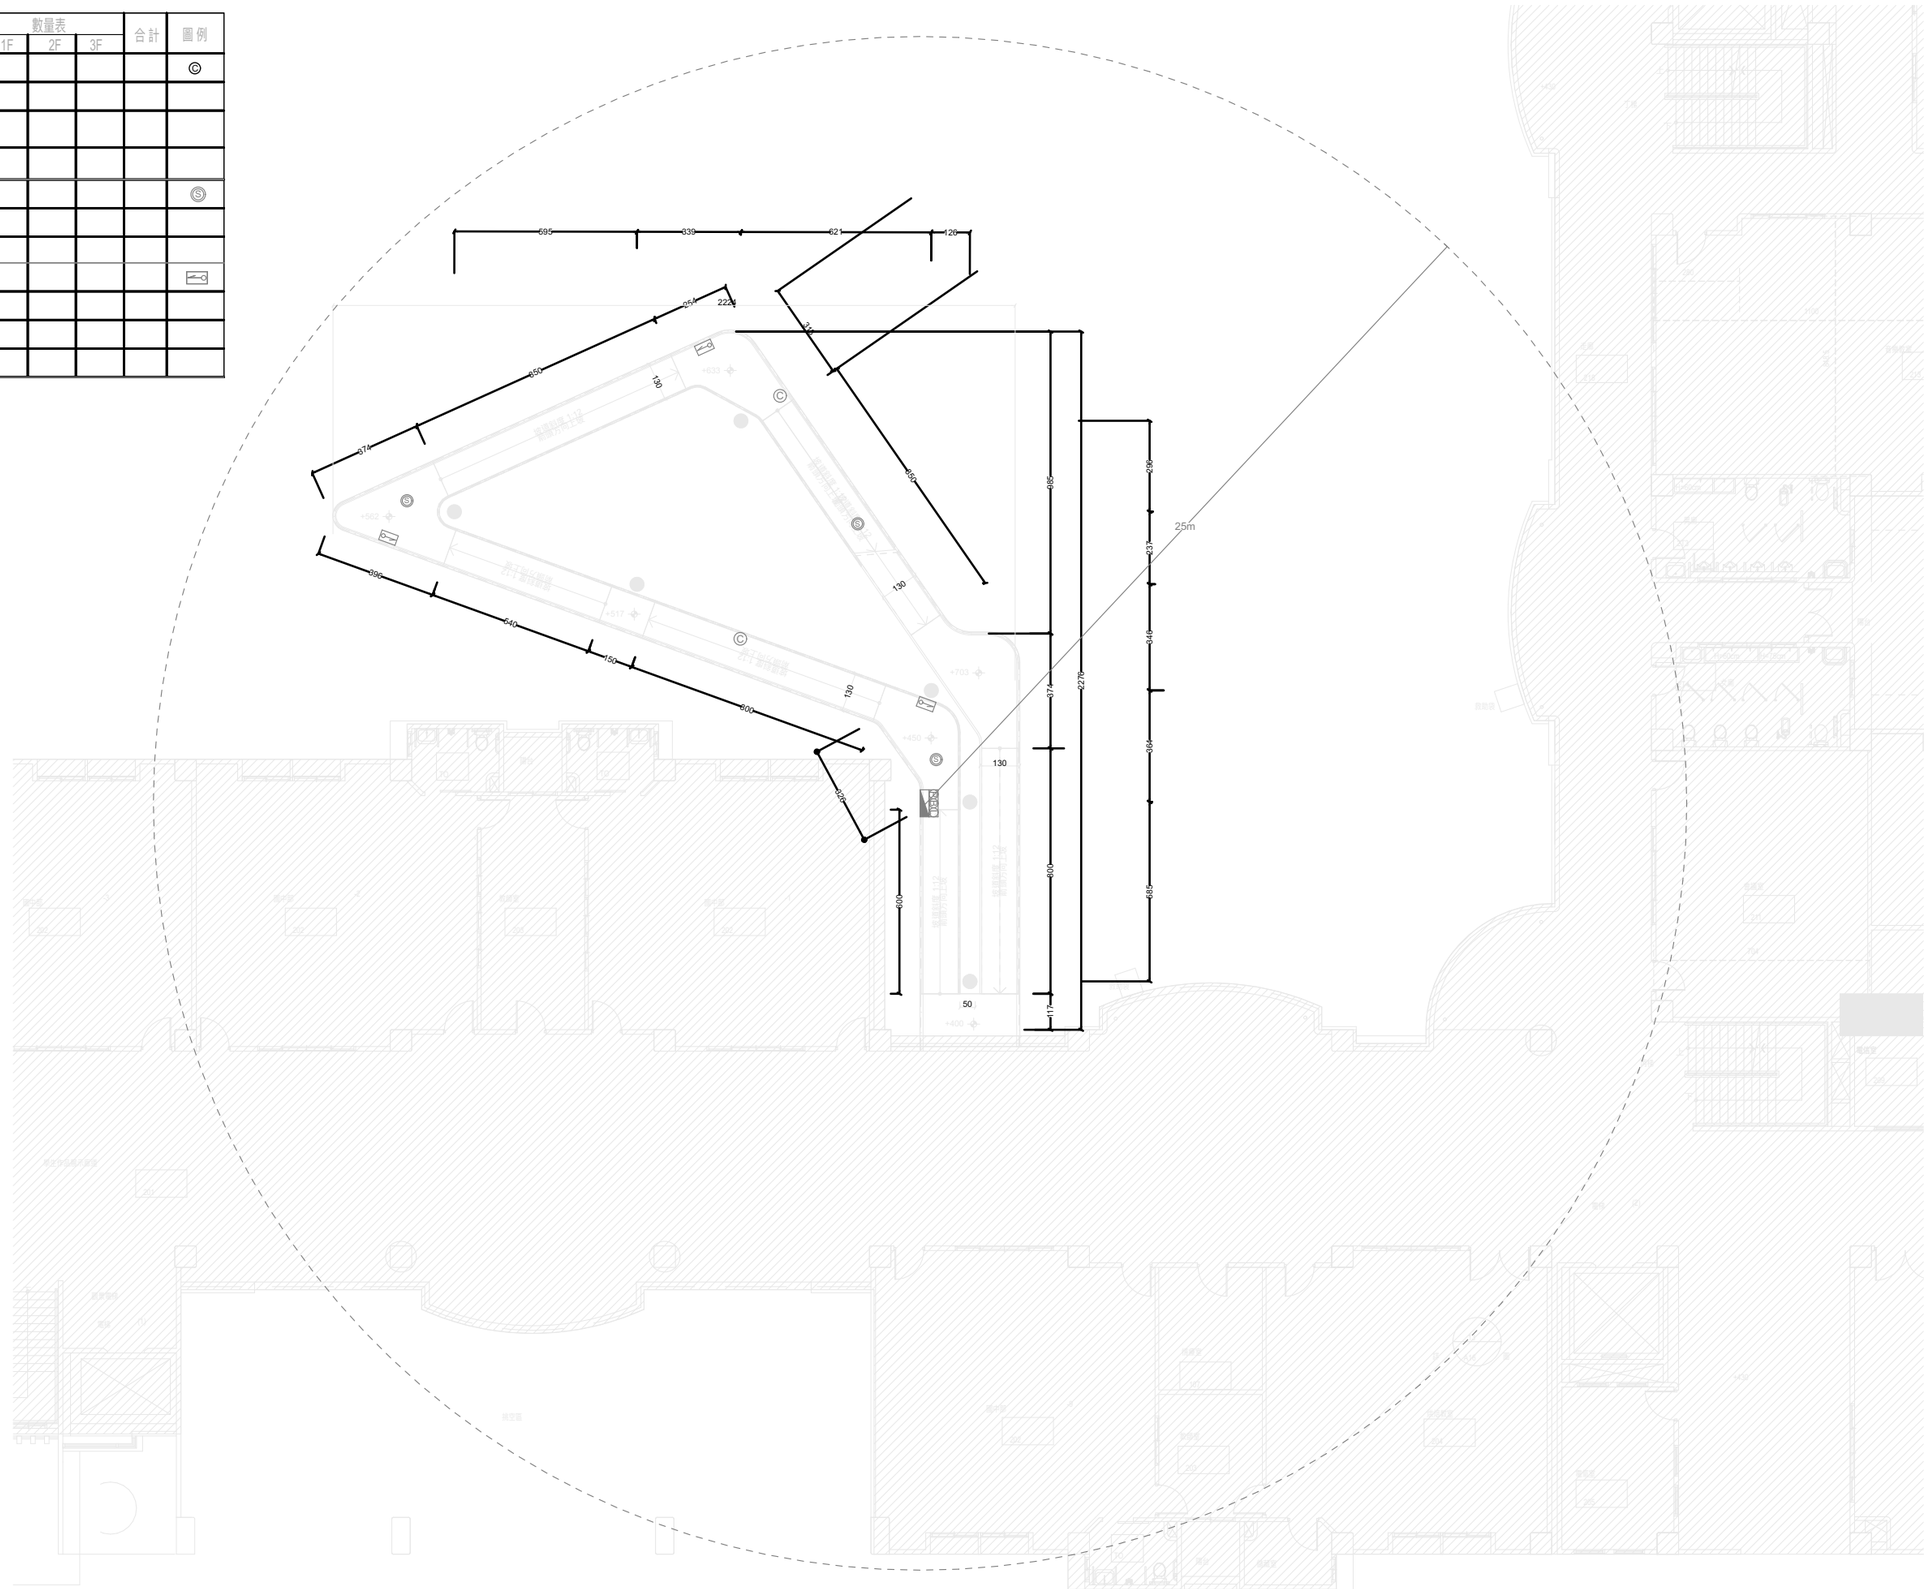

695
339
621
120
254
2224
450
130
674
396
540
150
600
130
130
130


設備項目	種類系統	圖例	規格及說明	數量表 1F	2F	3F	合計	圖例
	滅火器	©	10型乾粉滅火器A-3 B-10 C 附[滅火器]標示牌及固定架					©
		Ⓢ	探聲器5W I 級 壁掛式 92分貝以上					Ⓢ

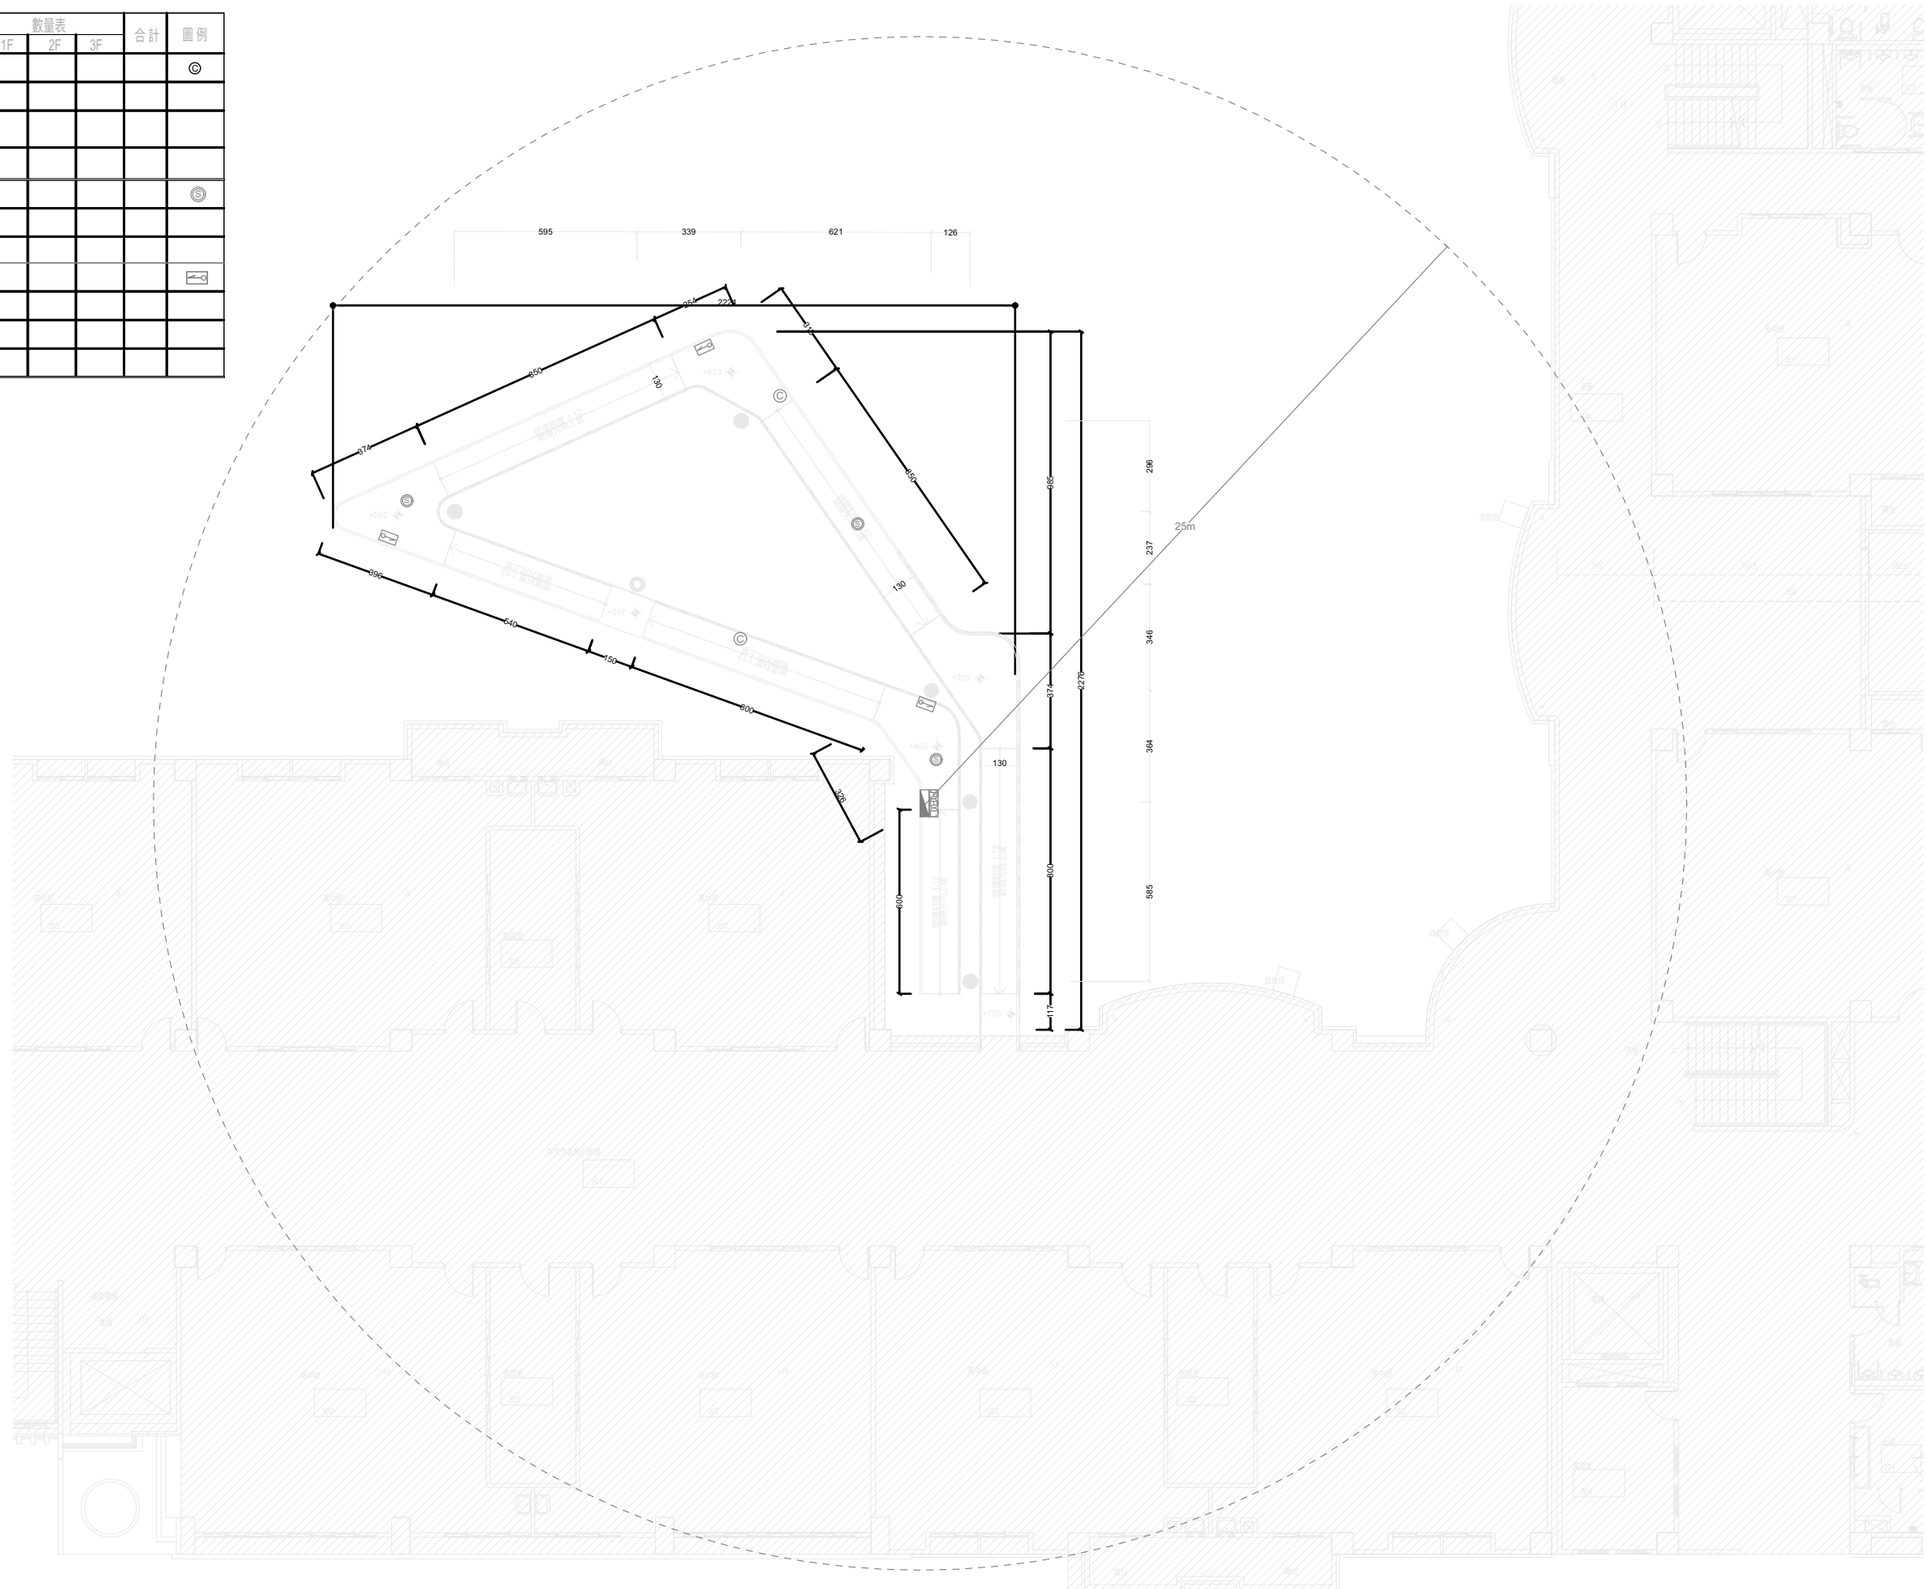


ATELIER	notes 細部設計圖	Project 學校環境設施無障礙逃生坡道增建工程	Scale	Title 參層消防設備平面圖	Layout ID F.3	27/28	Date 2026/10/2

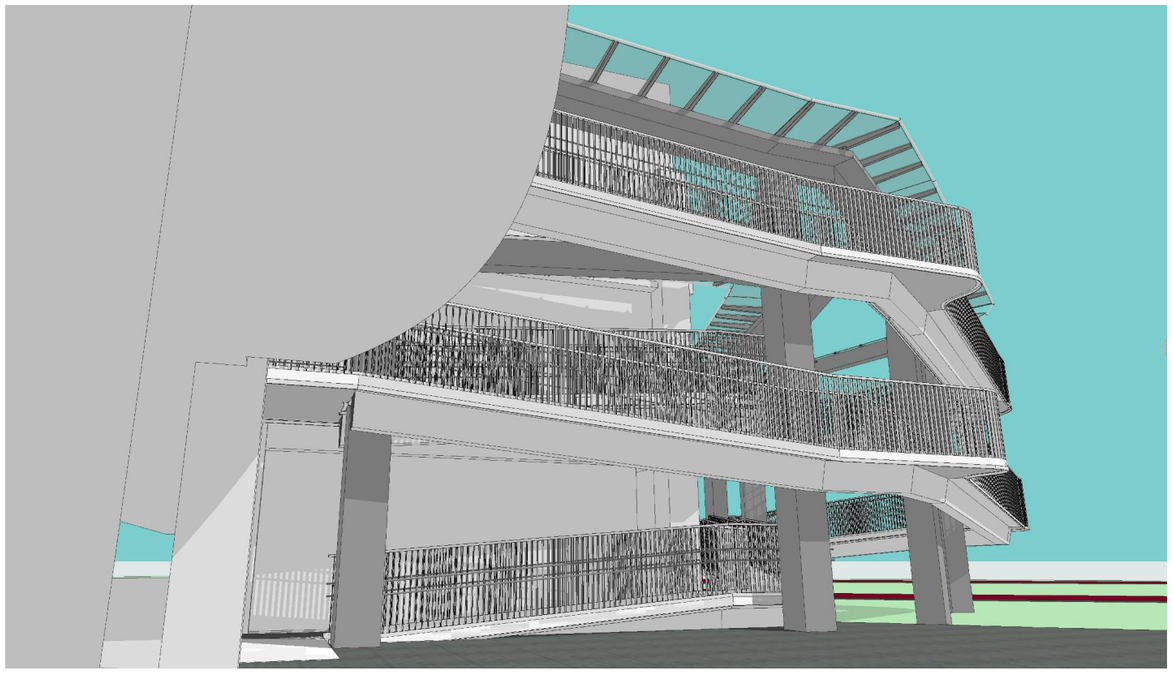

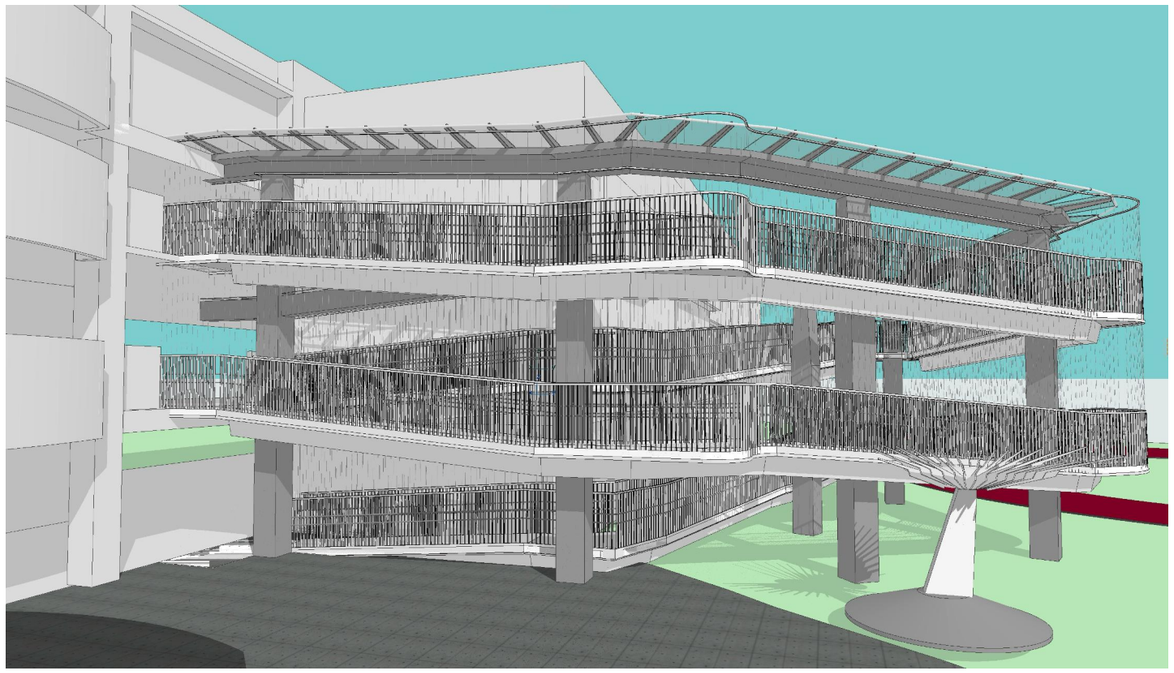

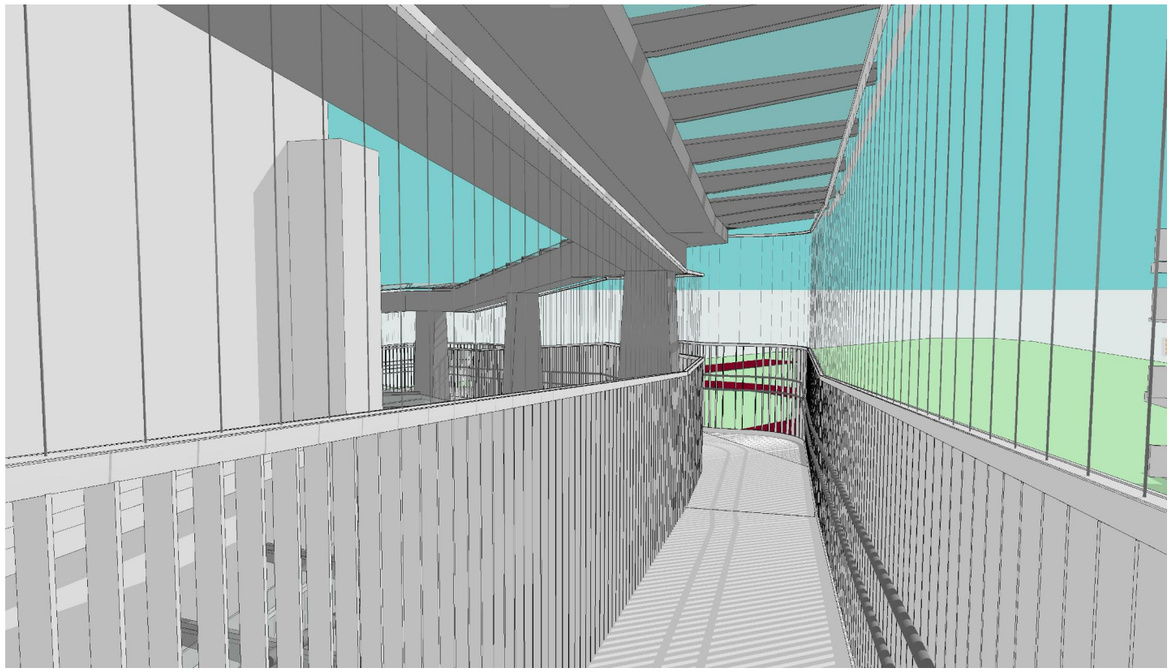

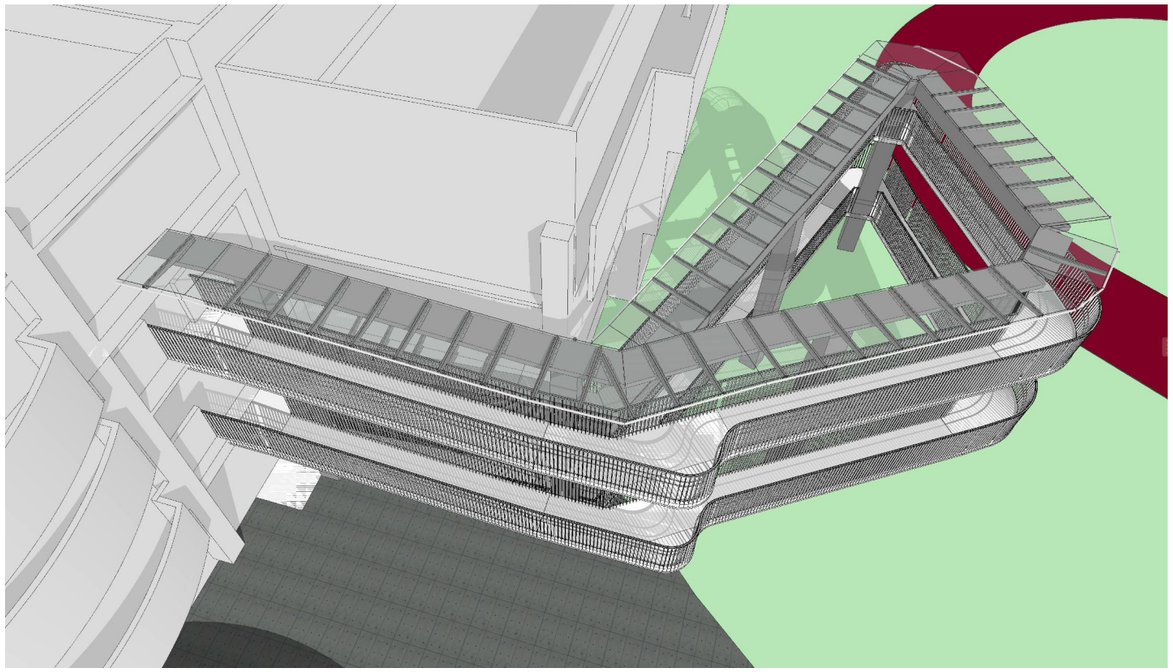

ATELIER	notes 細部設計圖	Project 學校環境設施無障礙逃生坡道增建工程	Scale	Title 透視圖	Layout ID P.1	28/28	Date 2026/10/2