

國立臺南特殊教育學校－學校環境設施無障礙逃生坡道增建工程

變更設計RC結構

黃永健 建築師事務所 2026.09

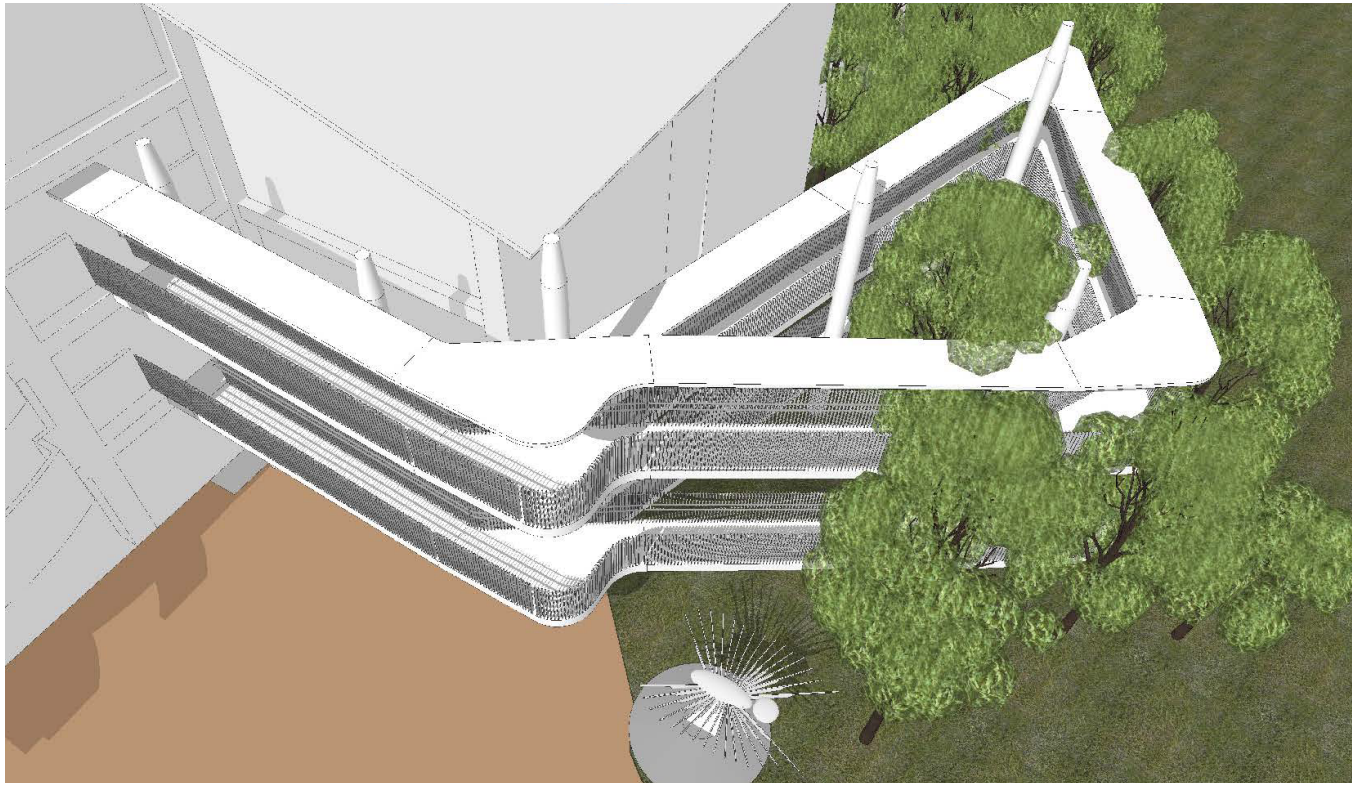

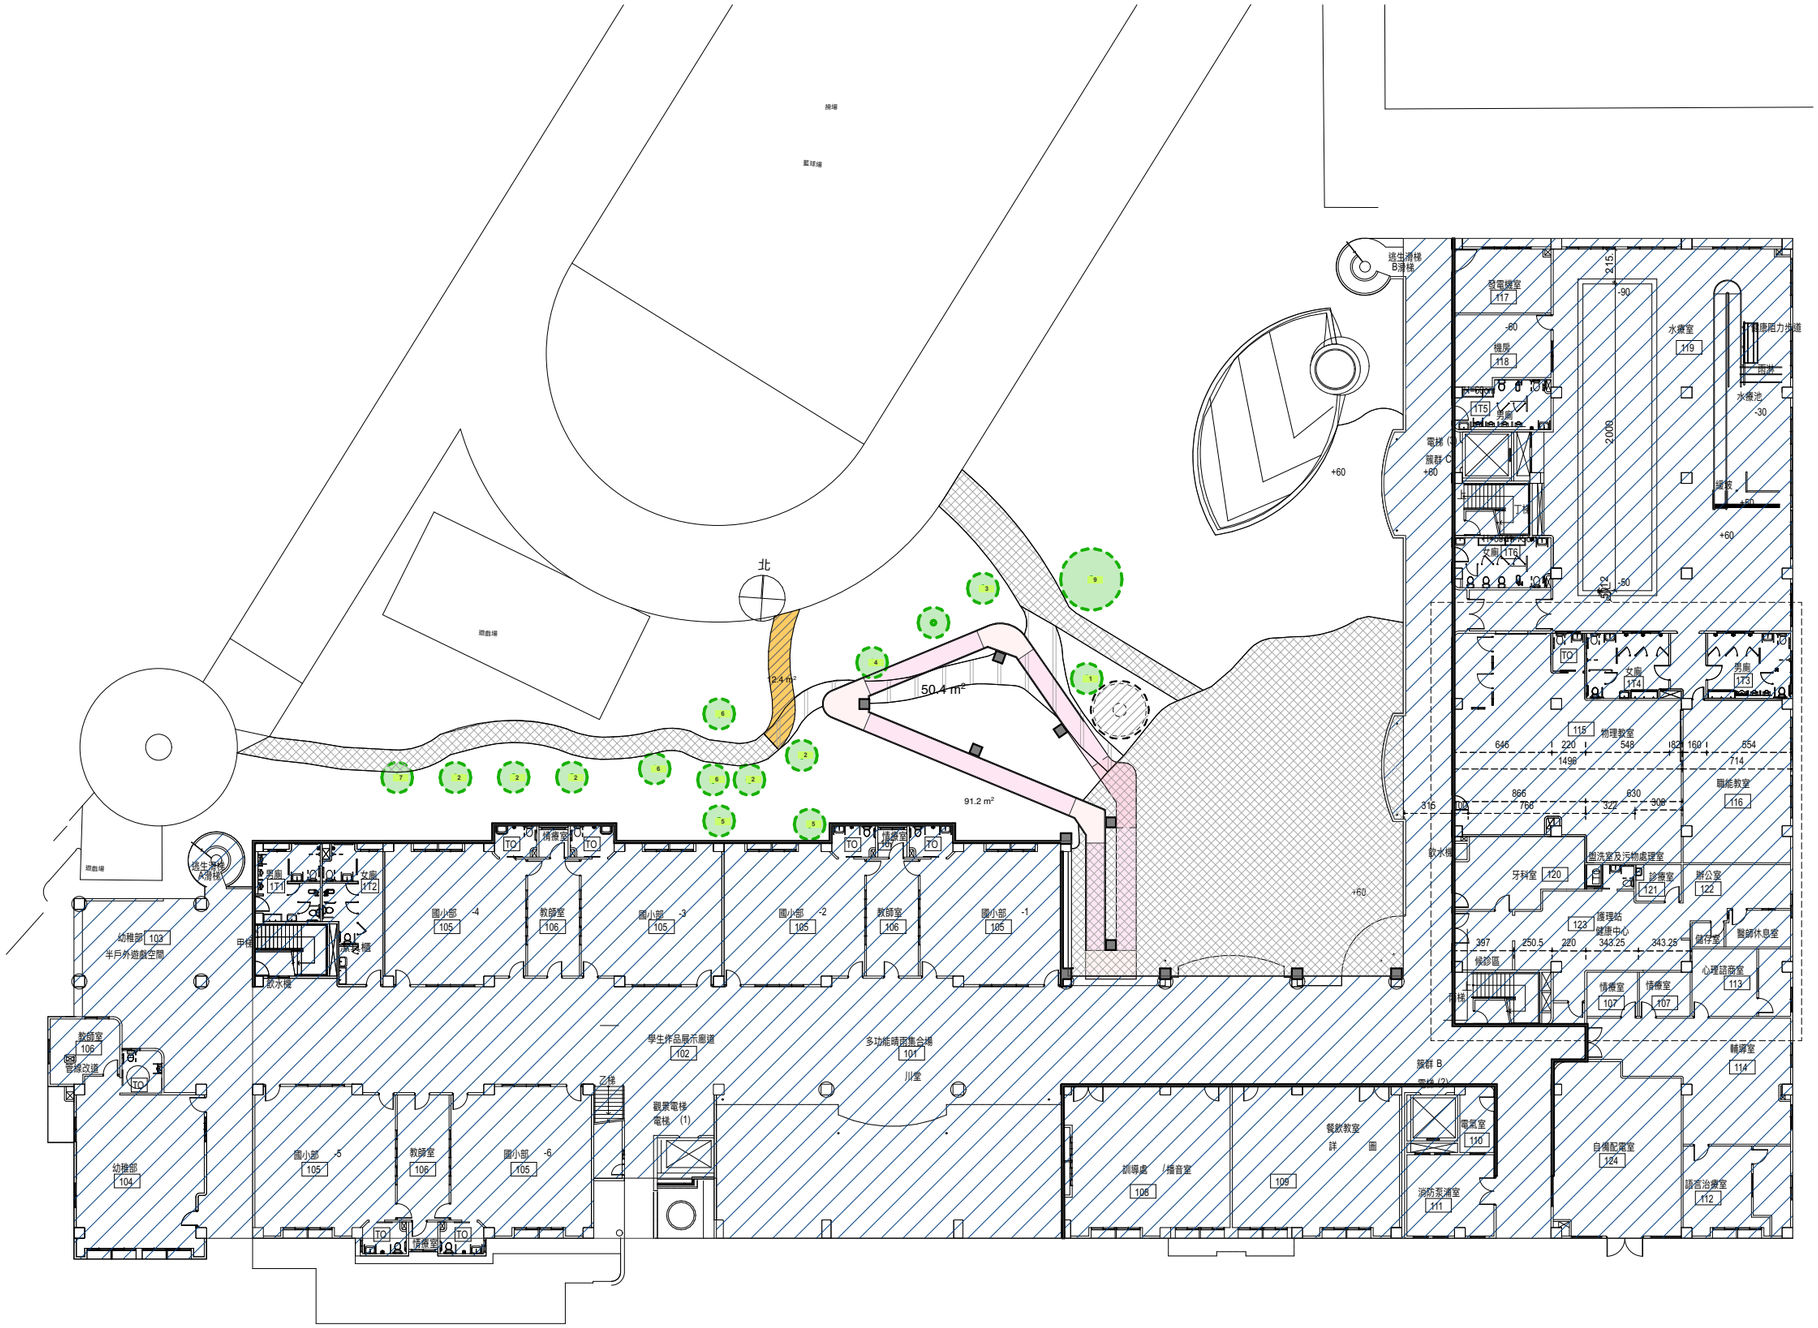

圖例


- 原有連鎖磚轉用鋪設
- 原有連鎖磚保留
- 本期工程新設坡道
- 原有喬木保留

配置平面圖

S=1:400

1

ATELIER	notes 細部設計圖	Project 學校環境設施無障礙逃生坡道增建工程	Scale	Title 配置平面圖	Layout ID A1.2	2/41	Date 2026/4/28

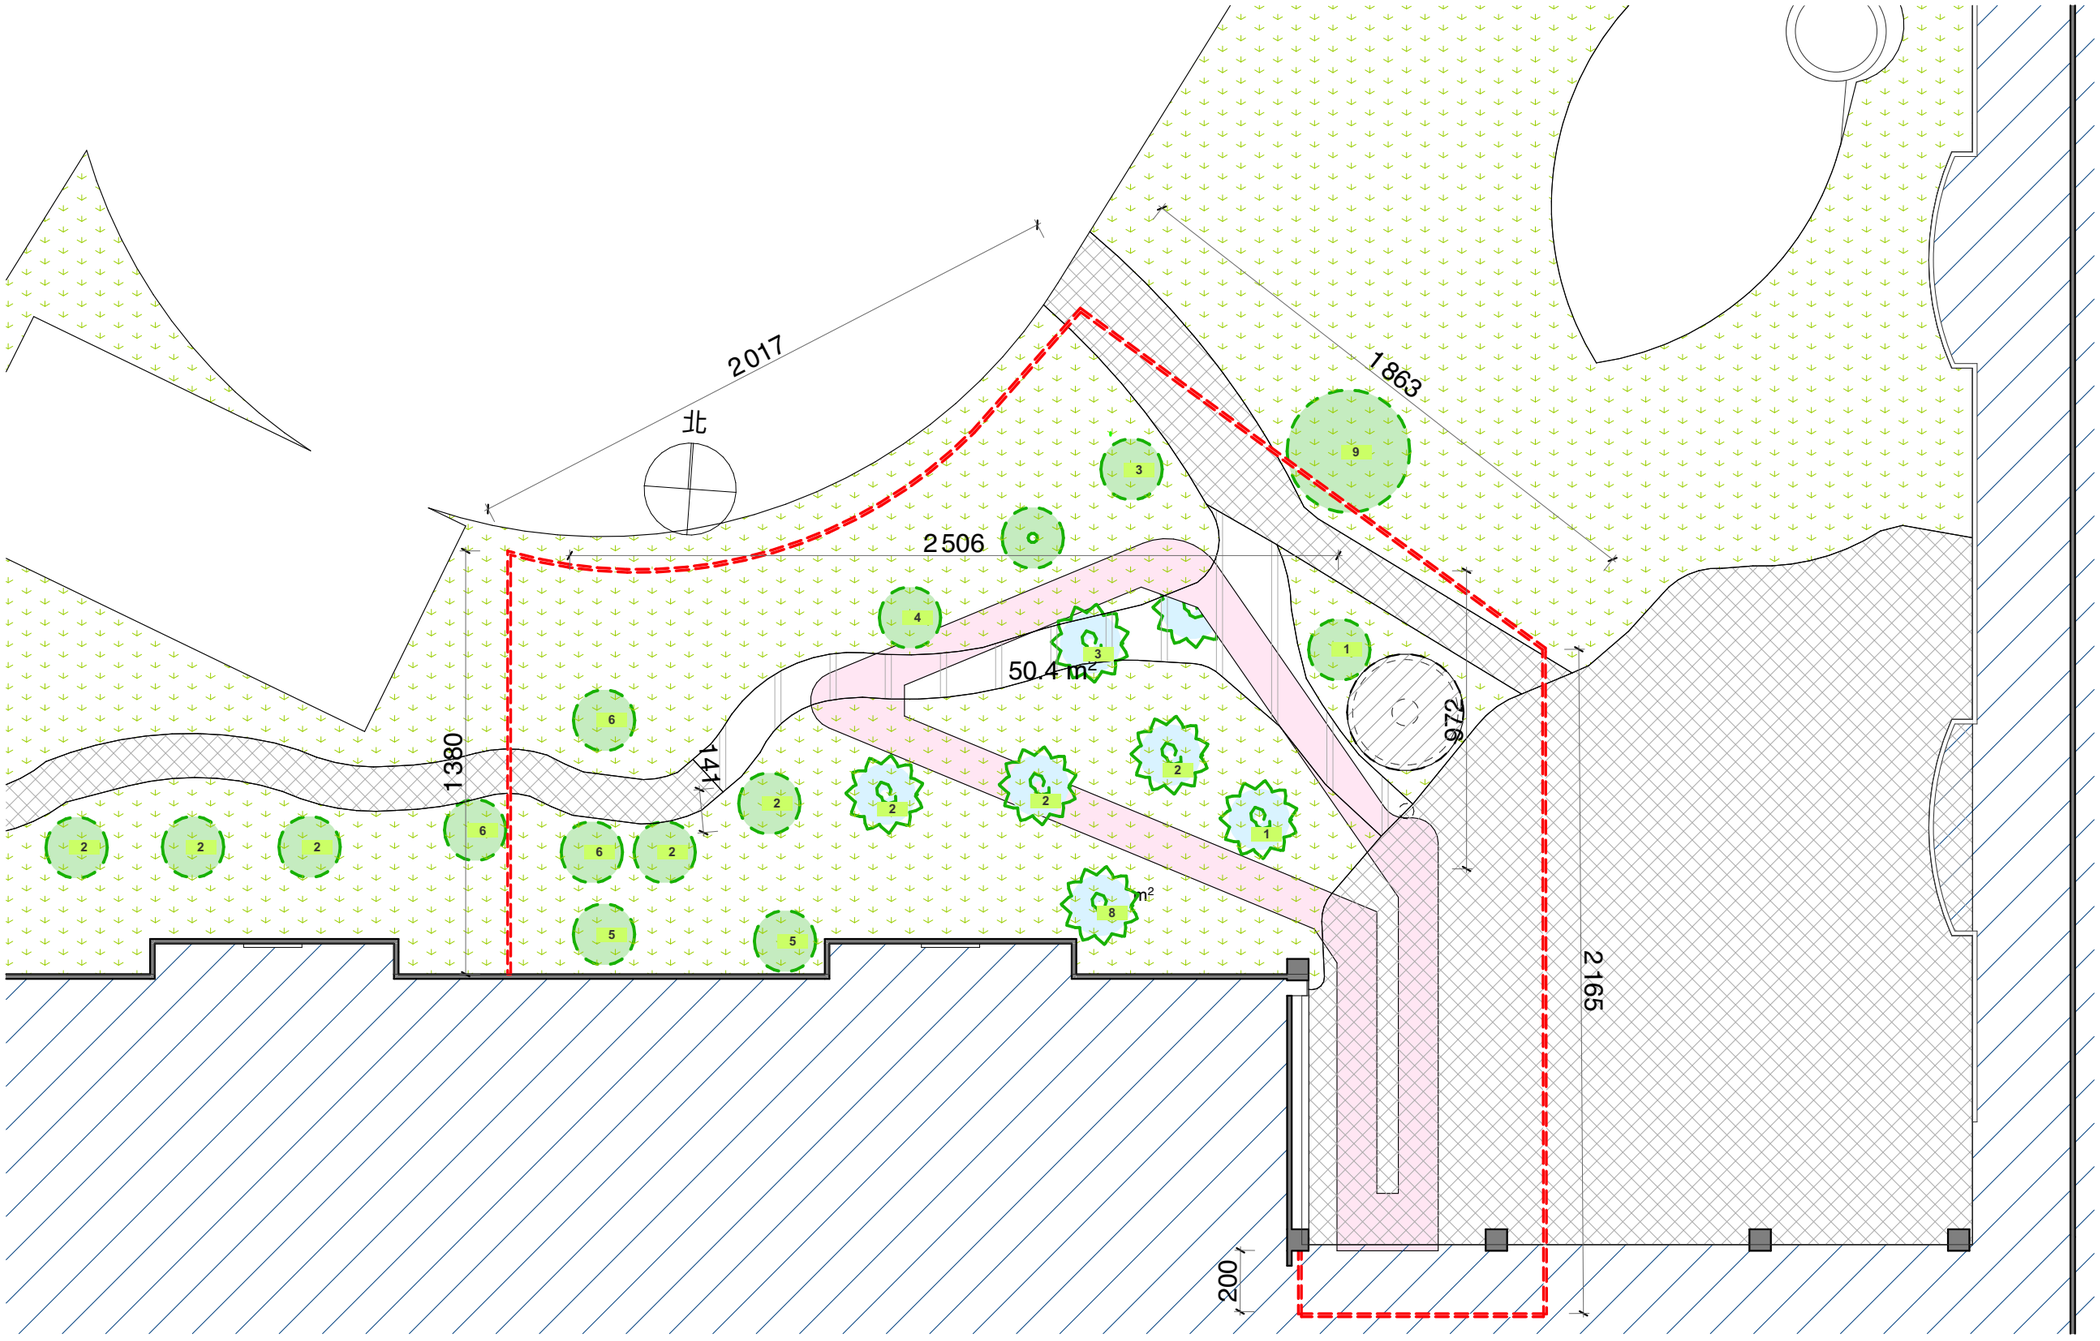

圖例

- 原有連鎖磚挖除轉用補植草皮
- 原有連鎖磚保留
- 原有喬木移植(業主另行處理)
- 原有喬木保留
- 甲種工地圍籬

原有喬木

1. 印度紫檀
2. 水黃皮
3. 黃槿
4. 阿勃勒
5. 台灣山欖
6. 無患子
7. 琴葉榕
8. 大葉山欖
9. 雨豆樹

整備平面圖
S=1:200

1

ATELIER	notes 細部設計圖	Project 學校環境設施無障礙逃生坡道增建工程	Scale	Title 整備平面圖	Layout ID A1.3	3/41	Date 2026/4/28

北

12.422 m²

50.444 m²

91.203 m²

8.000
3.194
1.959
1.006
3.194
14.508
8.500
9.100
2.789
2.057
630
0.392
324
2.181
4.244
23.215
8.000
7.001
871

情療室
107
TO
TO


國小部 -3 105
國小部 -2 105
教師室 106
國小部 -1 105

一層平面圖

S=1:120.00

1

ATELIER	notes 細部設計圖	Project 學校環境設施無障礙逃生坡道增建工程	Scale	Title 一層平面圖	Layout ID A2.1	4/41 Date 2026/4/28

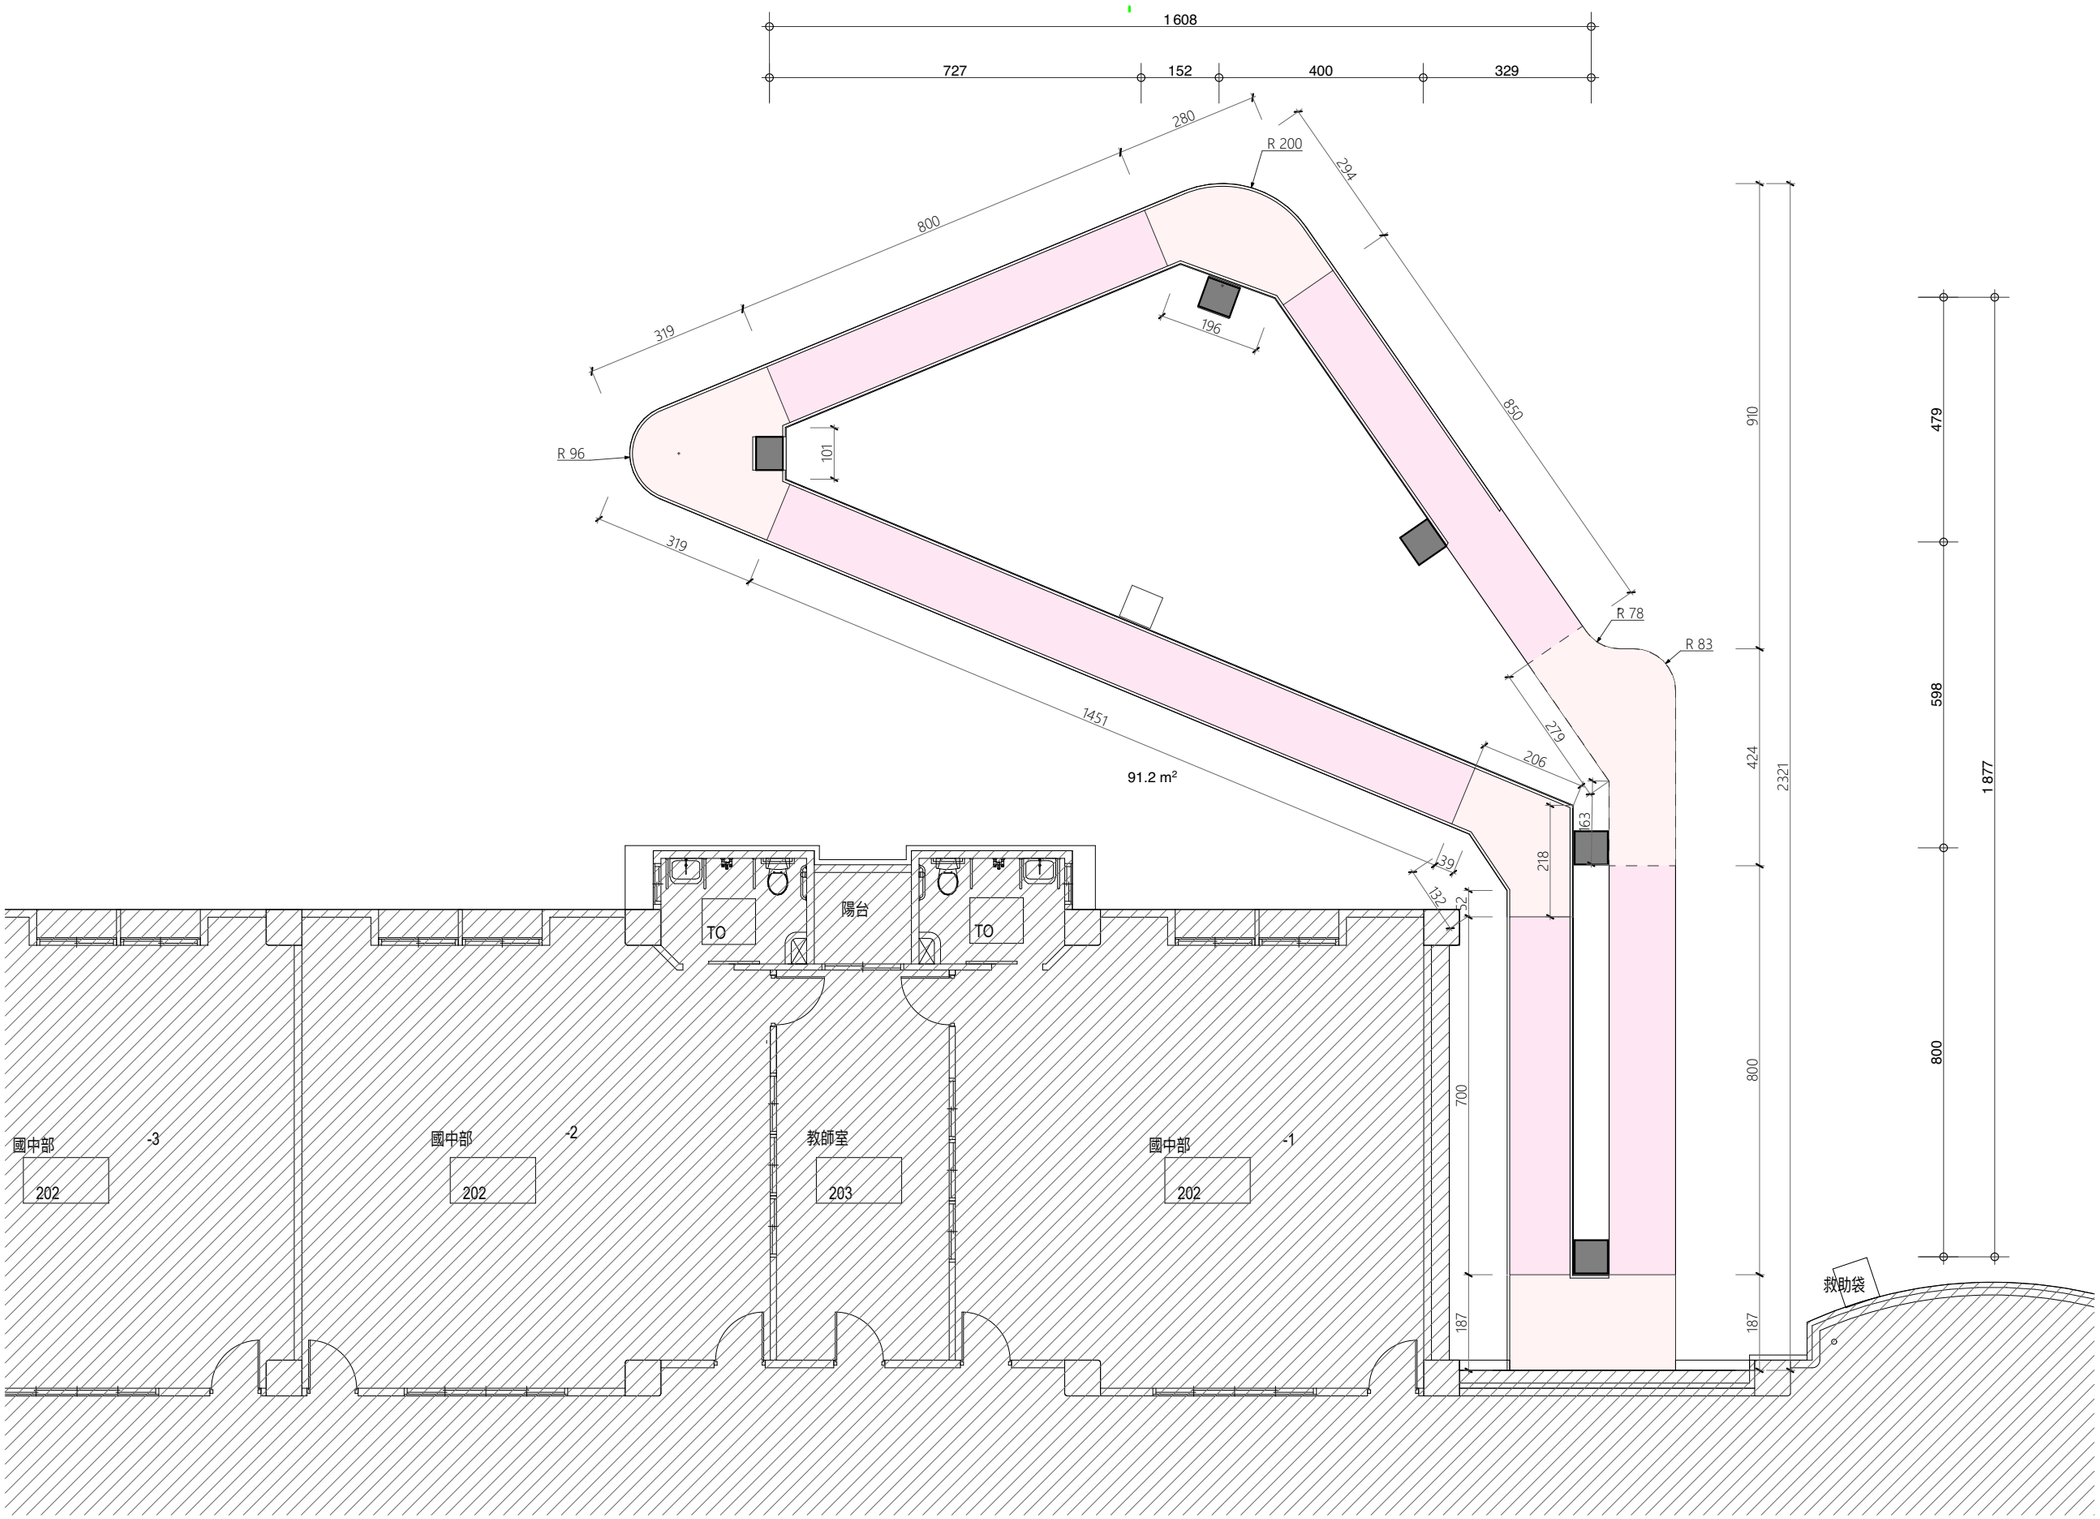


二層平面圖

S=1:120.00

1


ATELIER	notes 細部設計圖	Project 學校環境設施無障礙逃生坡道增建工程	Scale	Title 二層平面圖	Layout ID A2.2	5/41	Date 2026/4/28

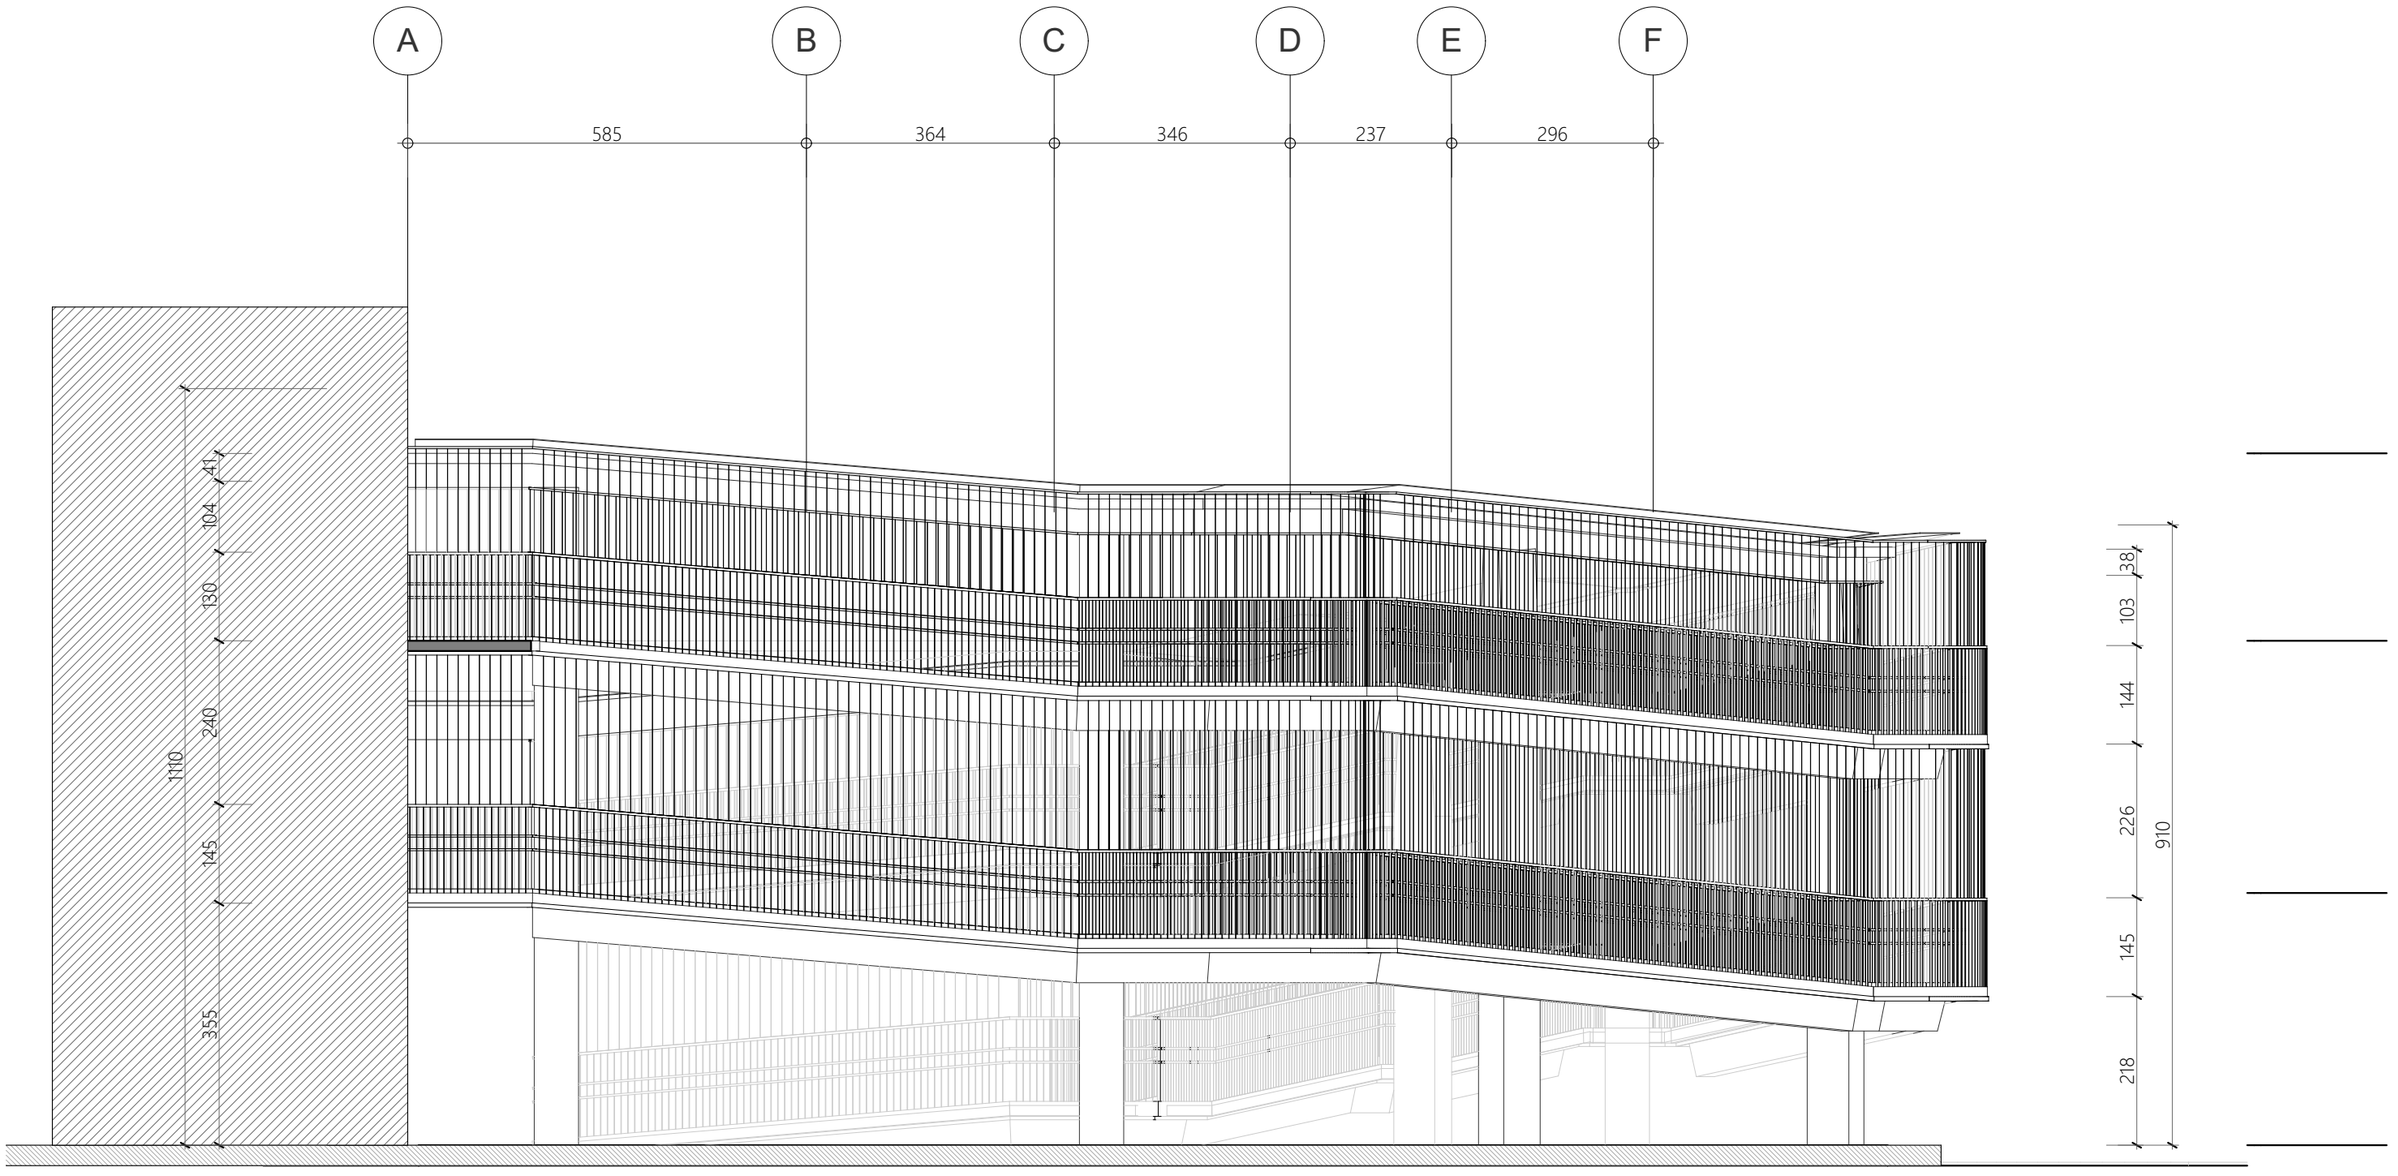



東向立面
S=1:90.00


1

ATELIER	notes 細部設計圖	Project 學校環境設施無障礙逃生坡道增建工程	Scale	Title 東向立面	Layout ID A3.1	8/41	Date 2026/4/28

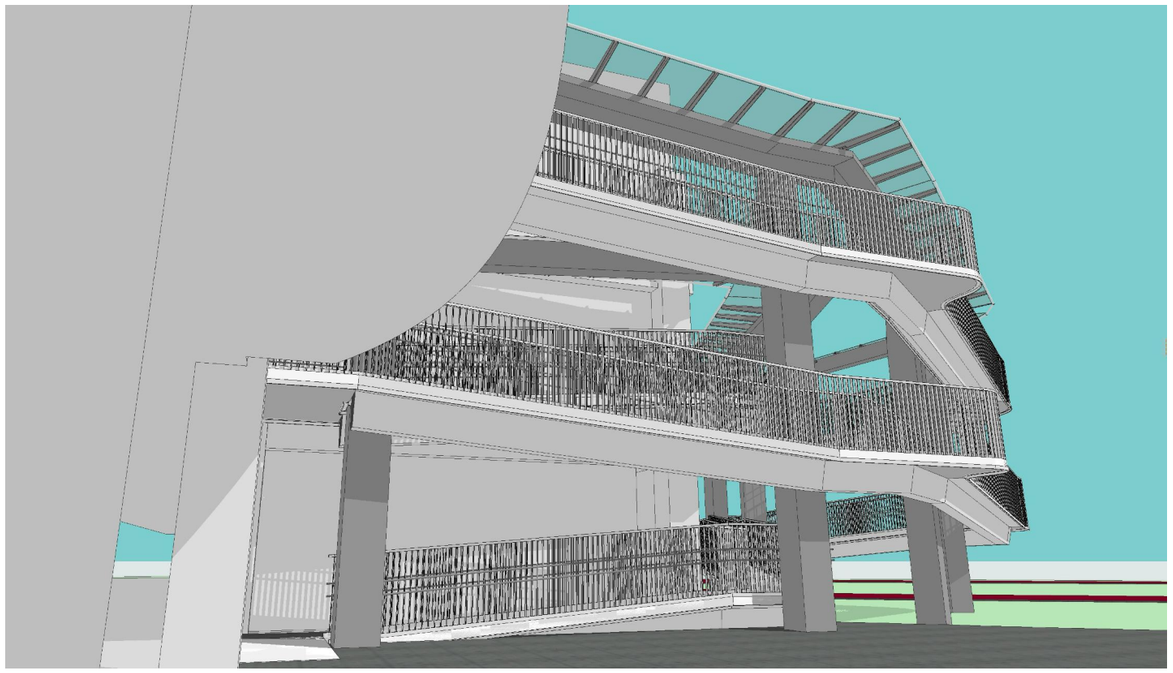

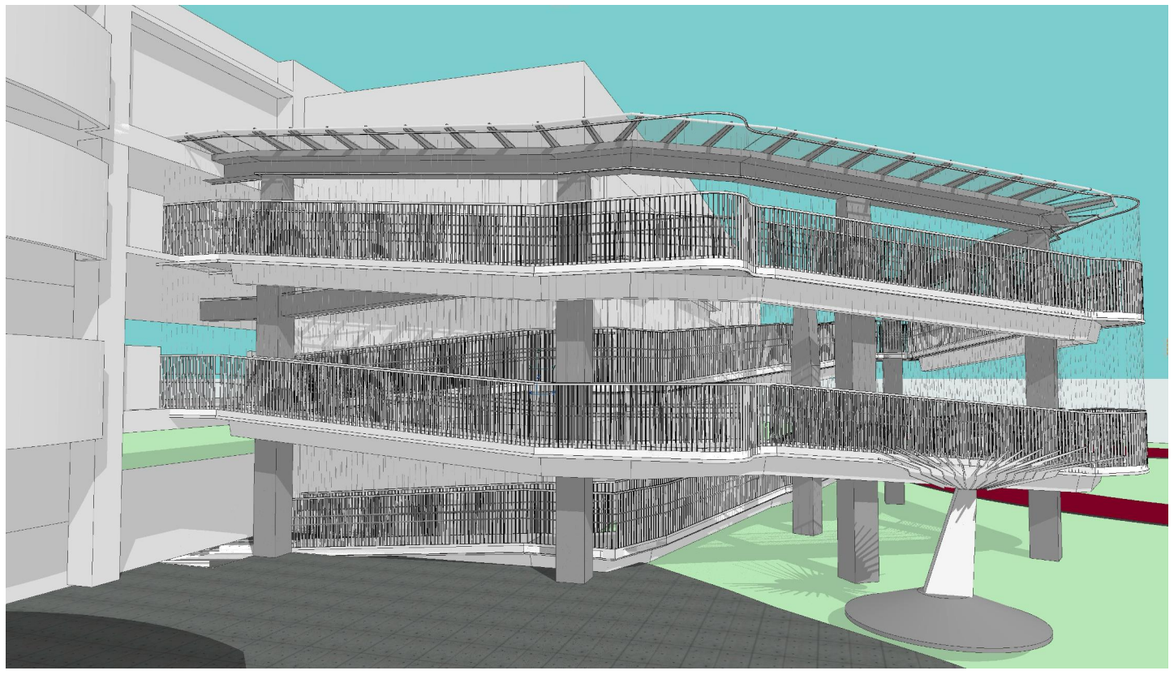

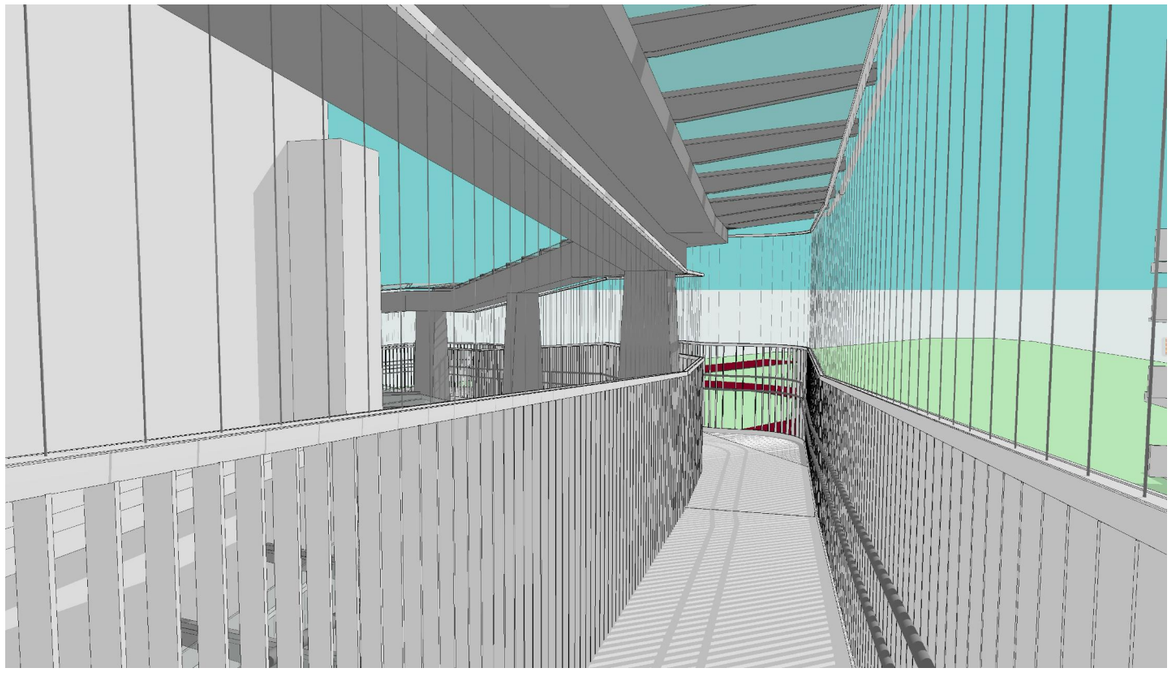

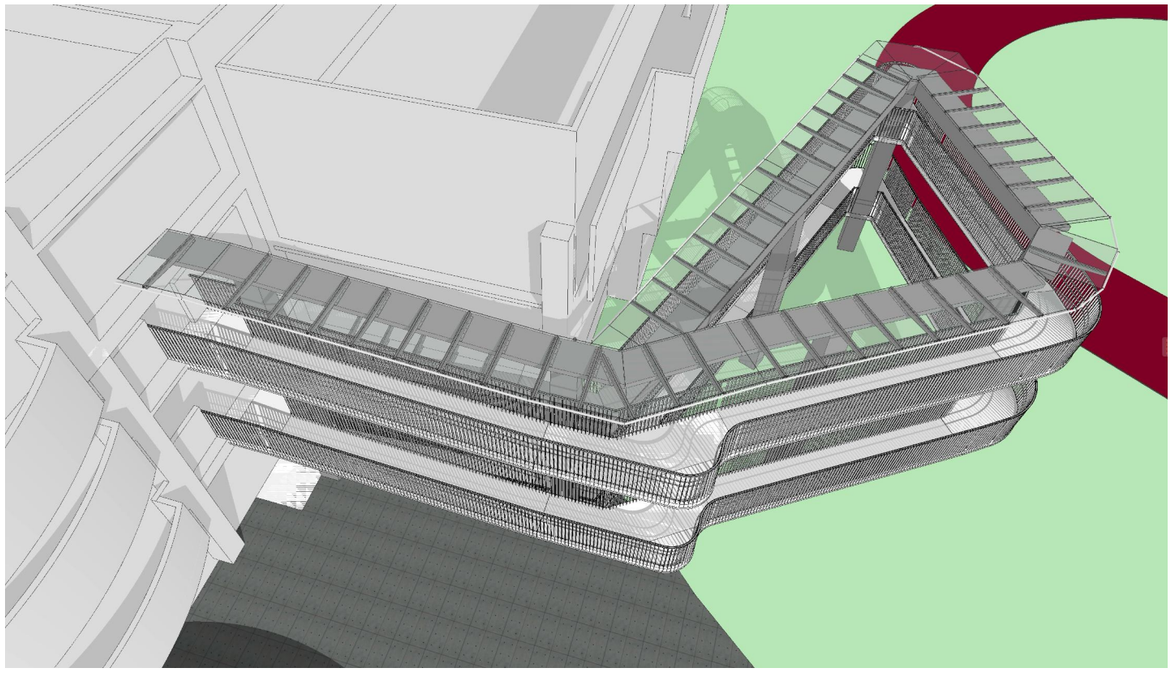

ATELIER	notes 細部設計圖	Project 學校環境設施無障礙逃生坡道增建工程	Scale	Title 透視圖	Layout ID P.1	41/41	Date 2026/4/28